


# Дизайн проект "Дистанционный"




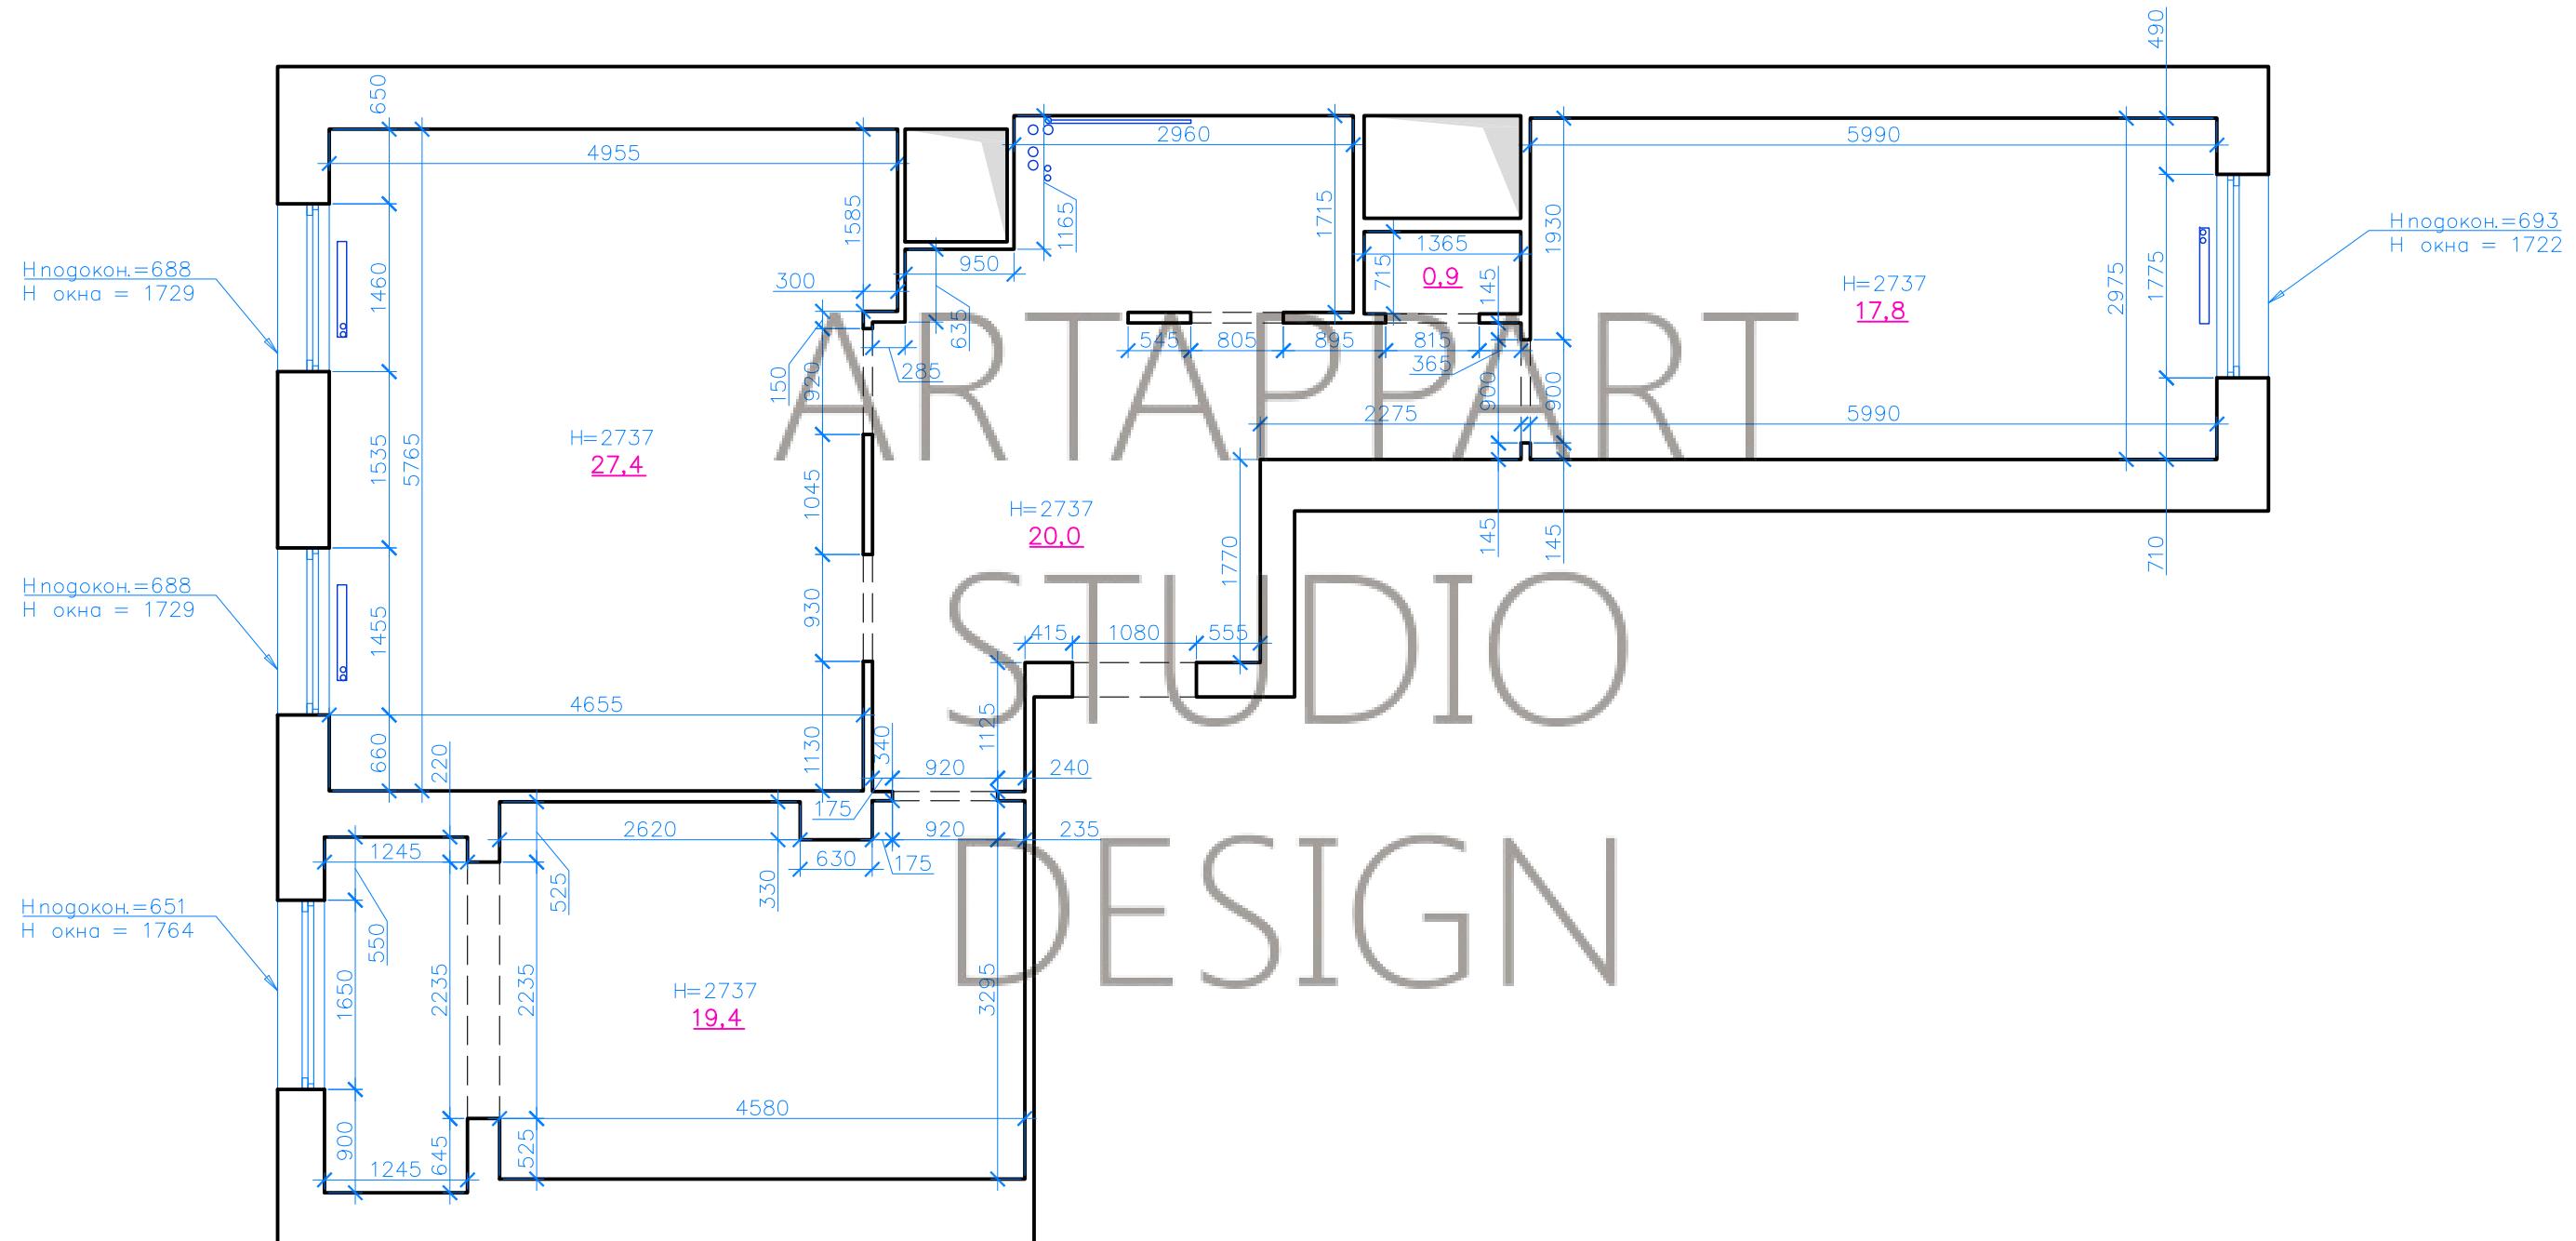

Собщ.=85,5 м<sup>2</sup>

Инв. № подл.	Подп. у дата	Взам. инв.
Согласовано		


Изм.	Кол. уч.	Листм	№ гок	Подп.	Дата	Разработка дизайн-проекта квартиры	Стадия	Листм	Листовъ
Заказчик			2017				P		
Разработ.			2017						
						Обмерный план			
						M 1: 60			
									ARTAPPART DESIGN STUDIO

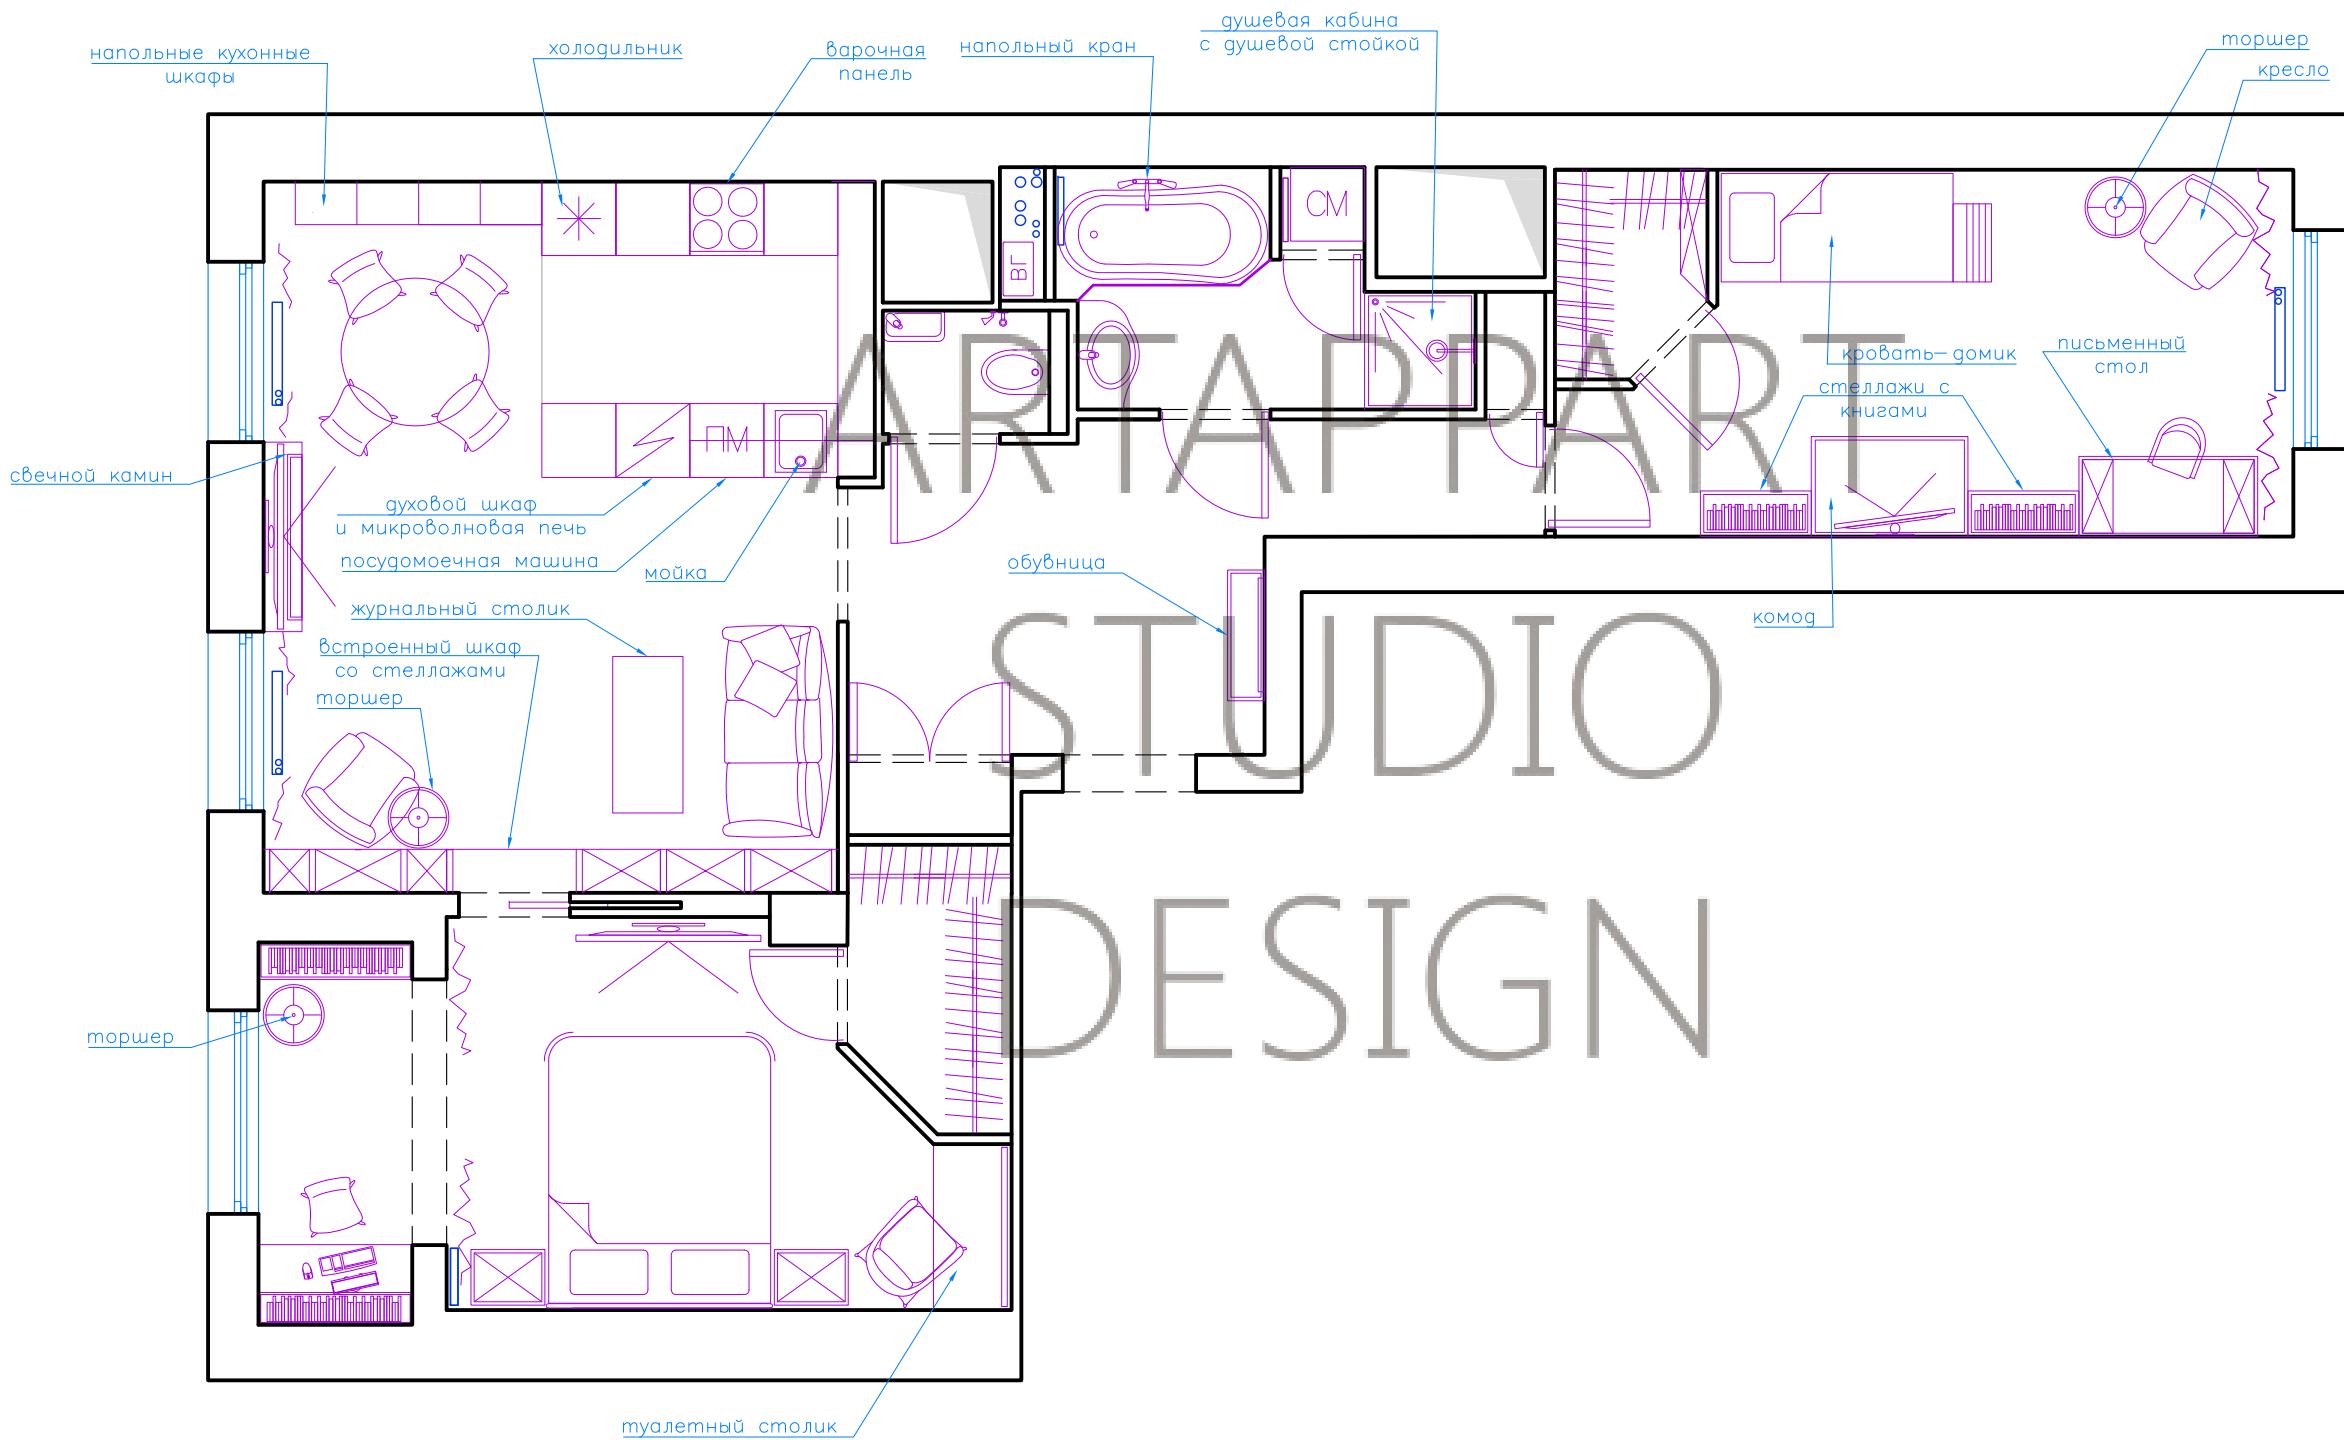

Согласовано

Инв. № подп. Подп. и дата Взам. инв.

Изм.	Кол. уч.	Лист	№ док.	Подп.	Дата	Разработка дизайн-проекта квартиры		
Заказчик						Стадия	Лист	Листов
Разработ.					2017	P		
					2017			
План расположения мебели и оборудования							М 1:60	
							 ARTAPPART DESIGN STUDIO	

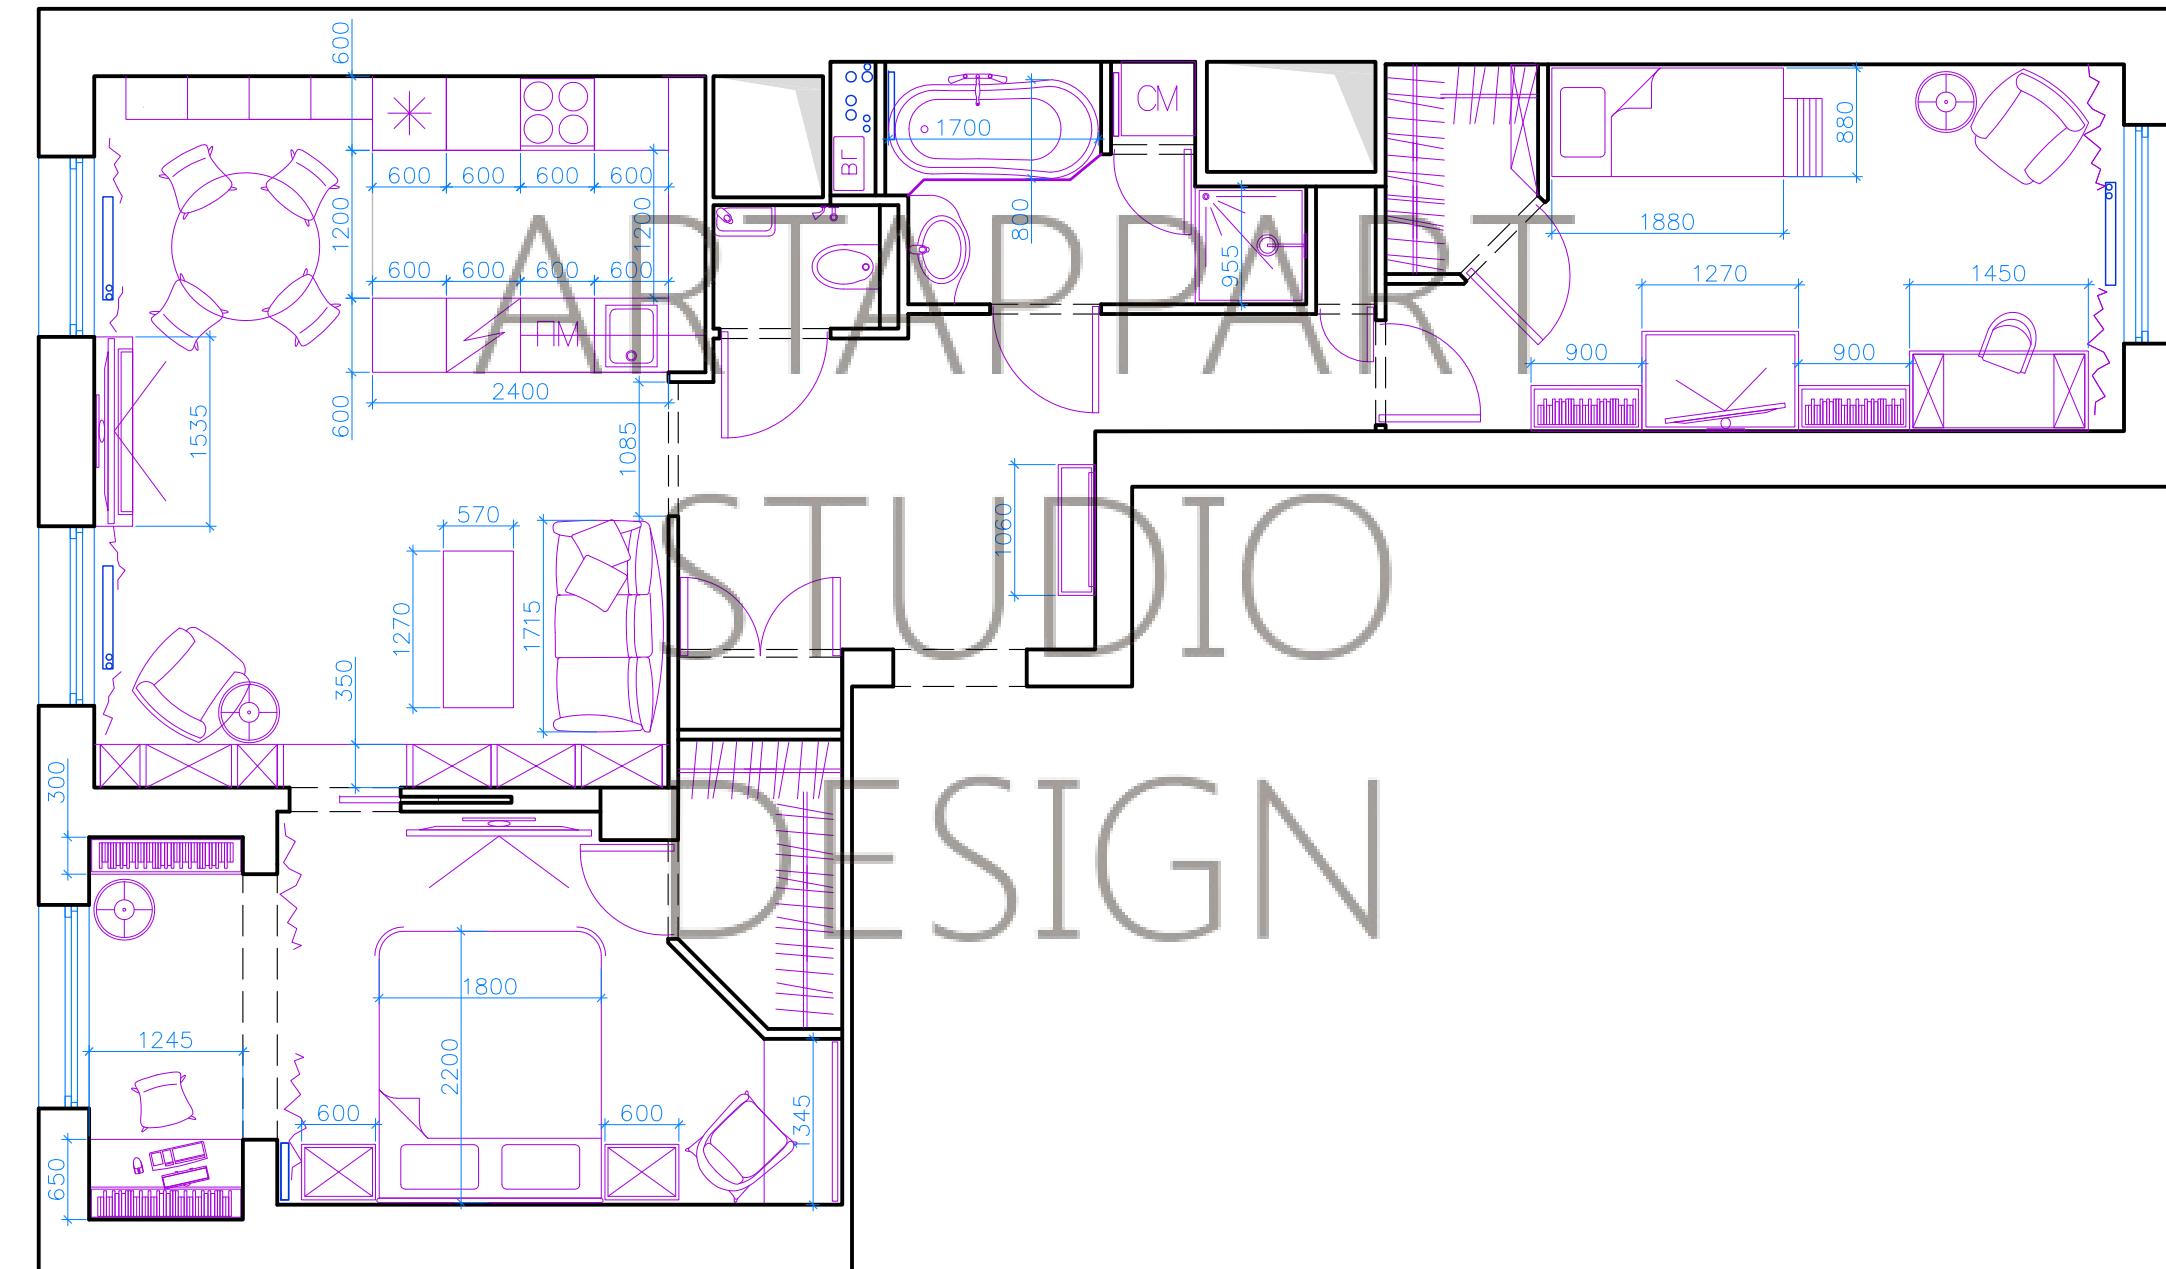

Инф. № подл.	Подп. у зам. инф.	Взам. инф.



Согласовано					
Инв. № подп.	Подп. и дата	Взам. инв.			


Примечание:  
Данные 3D коллажи представлены для примера, не  
относятся к приложенной рабочей документации.

Изм.	Кол. уч.	Листм	№ док.	Подп.	Дата	Разработка дизайн-проекта квартиры	Стадия	Листм	Листов
Заказчик					2017		P		
Разработ.					2017				

Визуализации



ARTAPPART  
DESIGN  
STUDIO

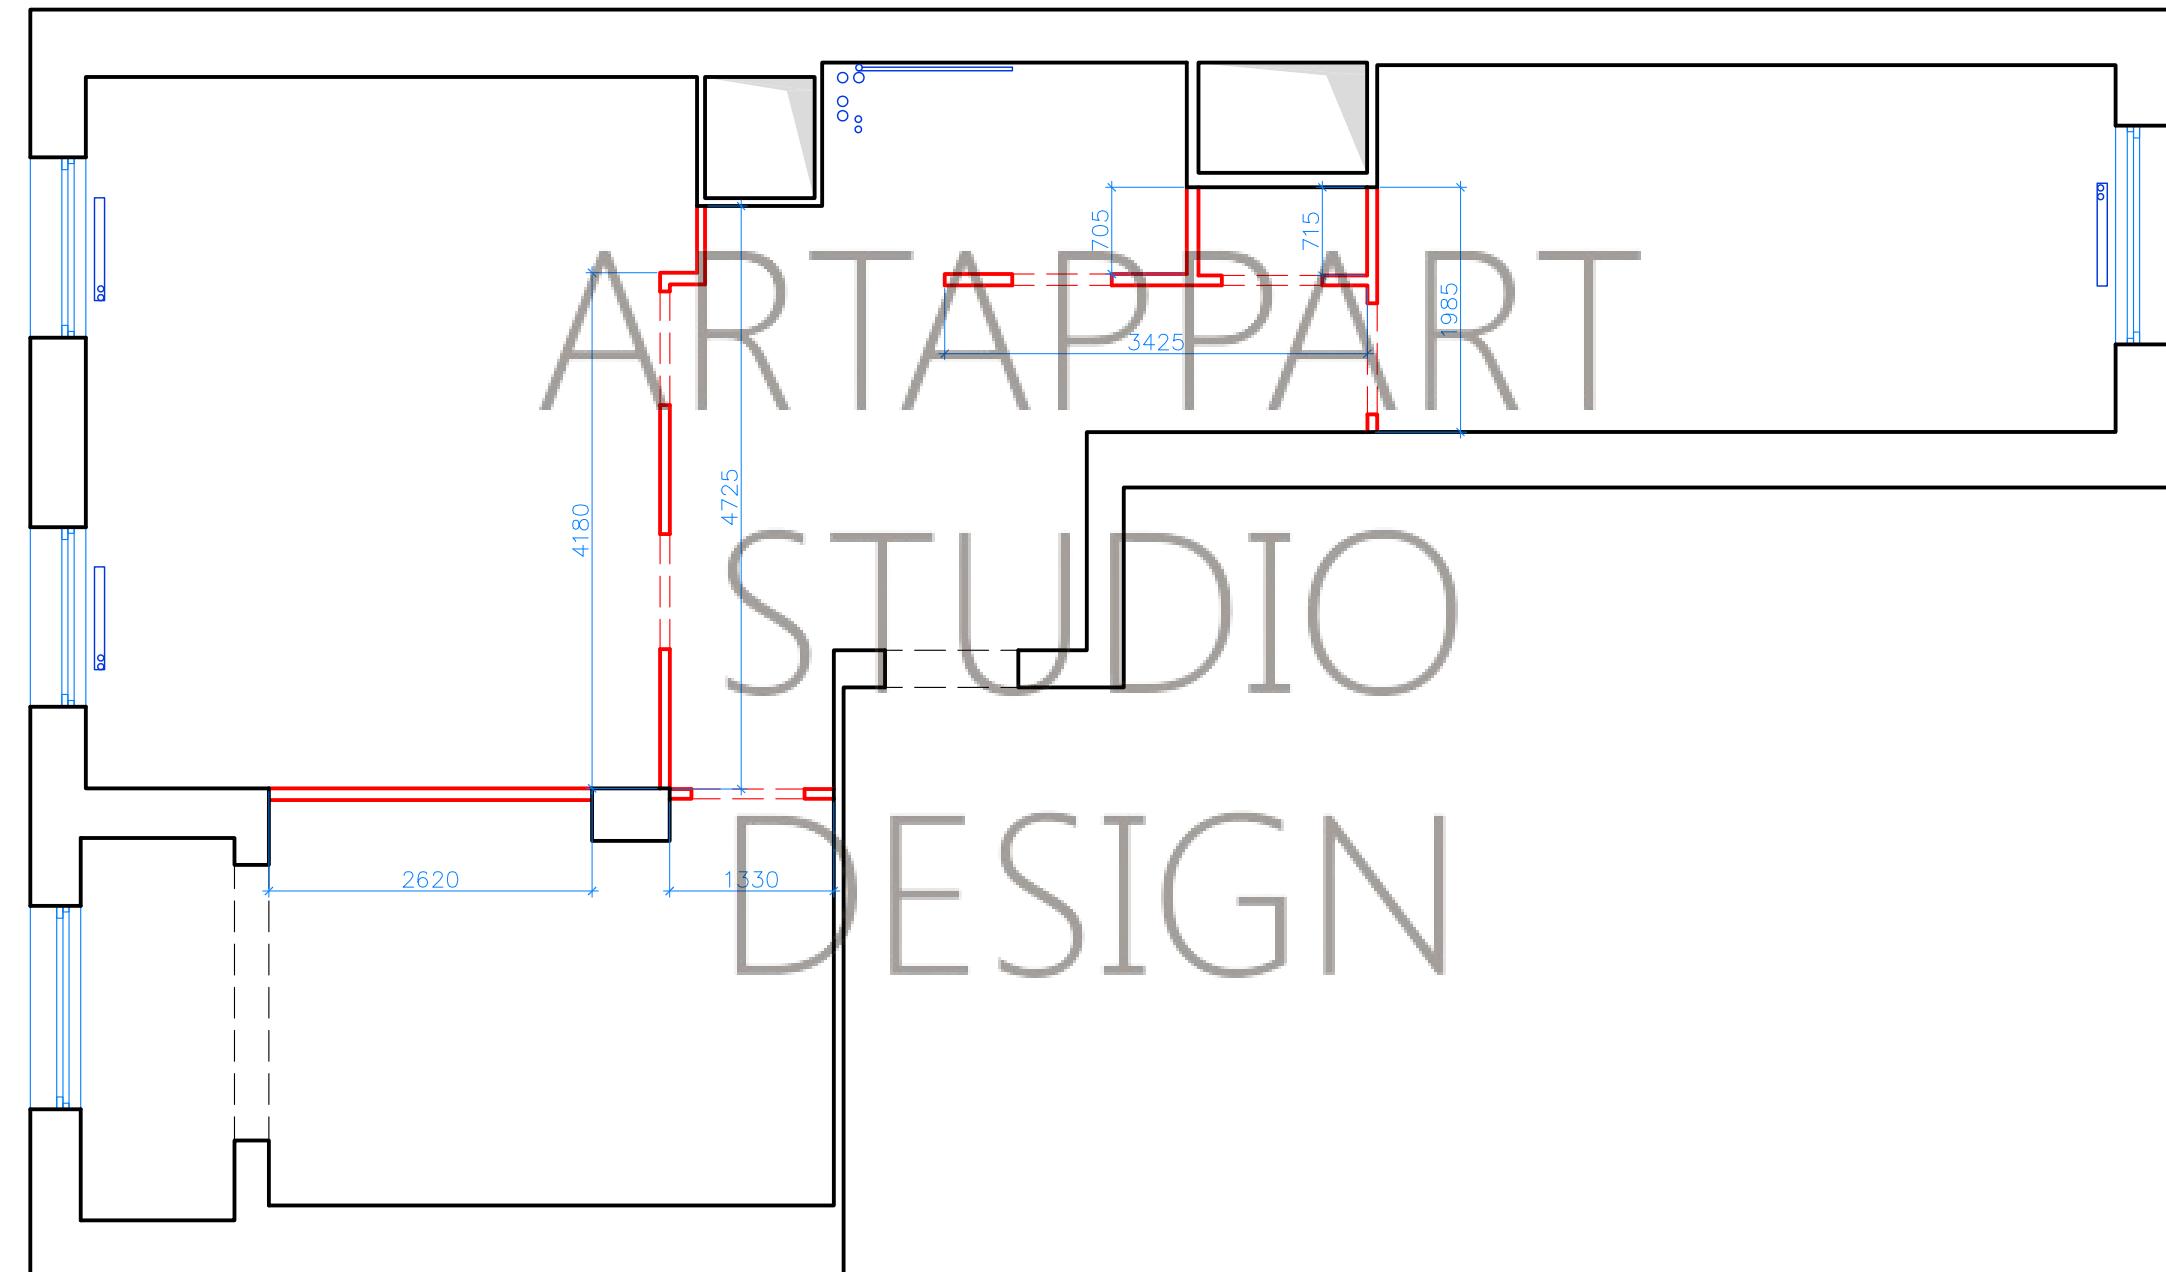


Условные обозначения:  
— — демонтируемые  
 перегородки

Инв. № подп.	Подп. и дата	Взам. инв.

Изм.	Кол. уч.	Лист	№ док.	Подп.	Дата	Разработка дизайн-проекта квартиры	Стадия	Лист	Листов
Заказчик					2017		P		
Разработ.					2017	План демонтажа	M 1:60		



ARTAPPART  
DESIGN  
STUDIO

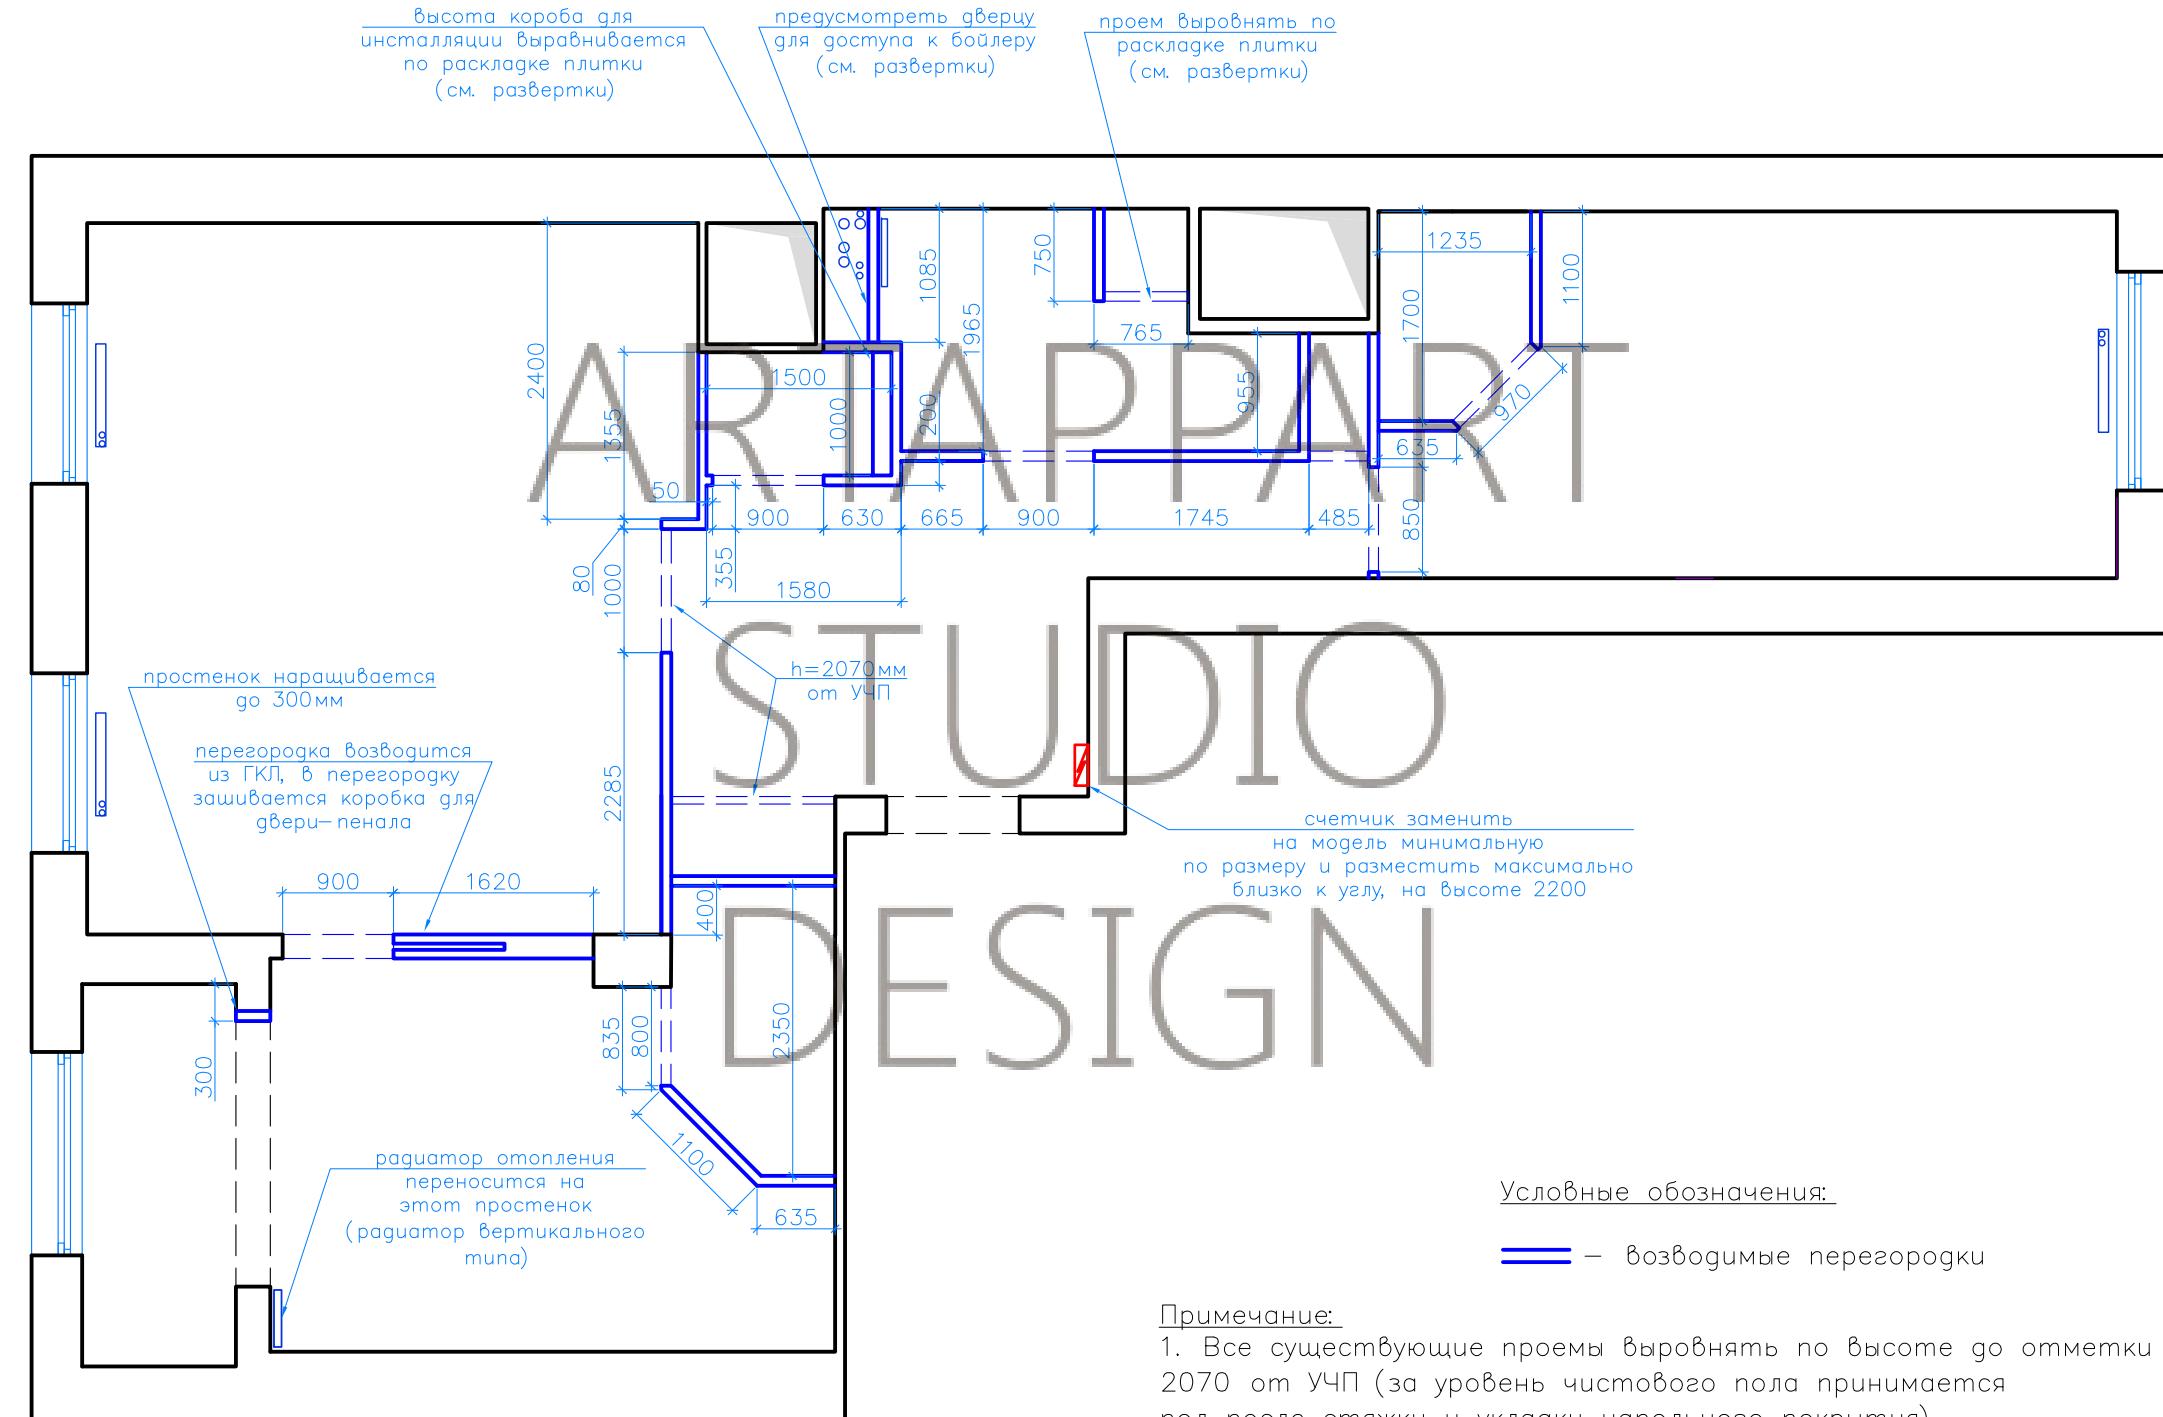

Примечание:

1. Все возводимые перегородки выполнить из пазогребневых плинтусов толщина 80 мм, если не указано иное.
  2. Во влажных помещениях использовать влагостойкий гипрок.

### Условные обозначения:

☰ – Воздушные перегородки


## Примечани

1. Все существующие проемы выровнять по высоте до отметки 2070 от УЧП (за уровень чистового пола принимается пол после стяжки и укладки напольного покрытия)
  2. Предусмотреть установку фильтров водоснабжения и ревизионных люков.
  3. Предусмотреть устройство вентиляции в санузлах.
  4. Разводка коммуникаций для систем кондиционирования выполняется предварительно, по проекту систем кондиционирования.

Изм.	Кол. уч.	Листм	№ док.	Подп.	Дата	Разработка дизайн-проекта квартиры	Стадия	Листм	Листов
Заказчик					2017		P		
Разработ					2017	План возводимых перегородок с маркеровкой двер. проемов М 1: 60			

Инв. № подп.	Подп. и дата	Взам. инв.


Согласовано

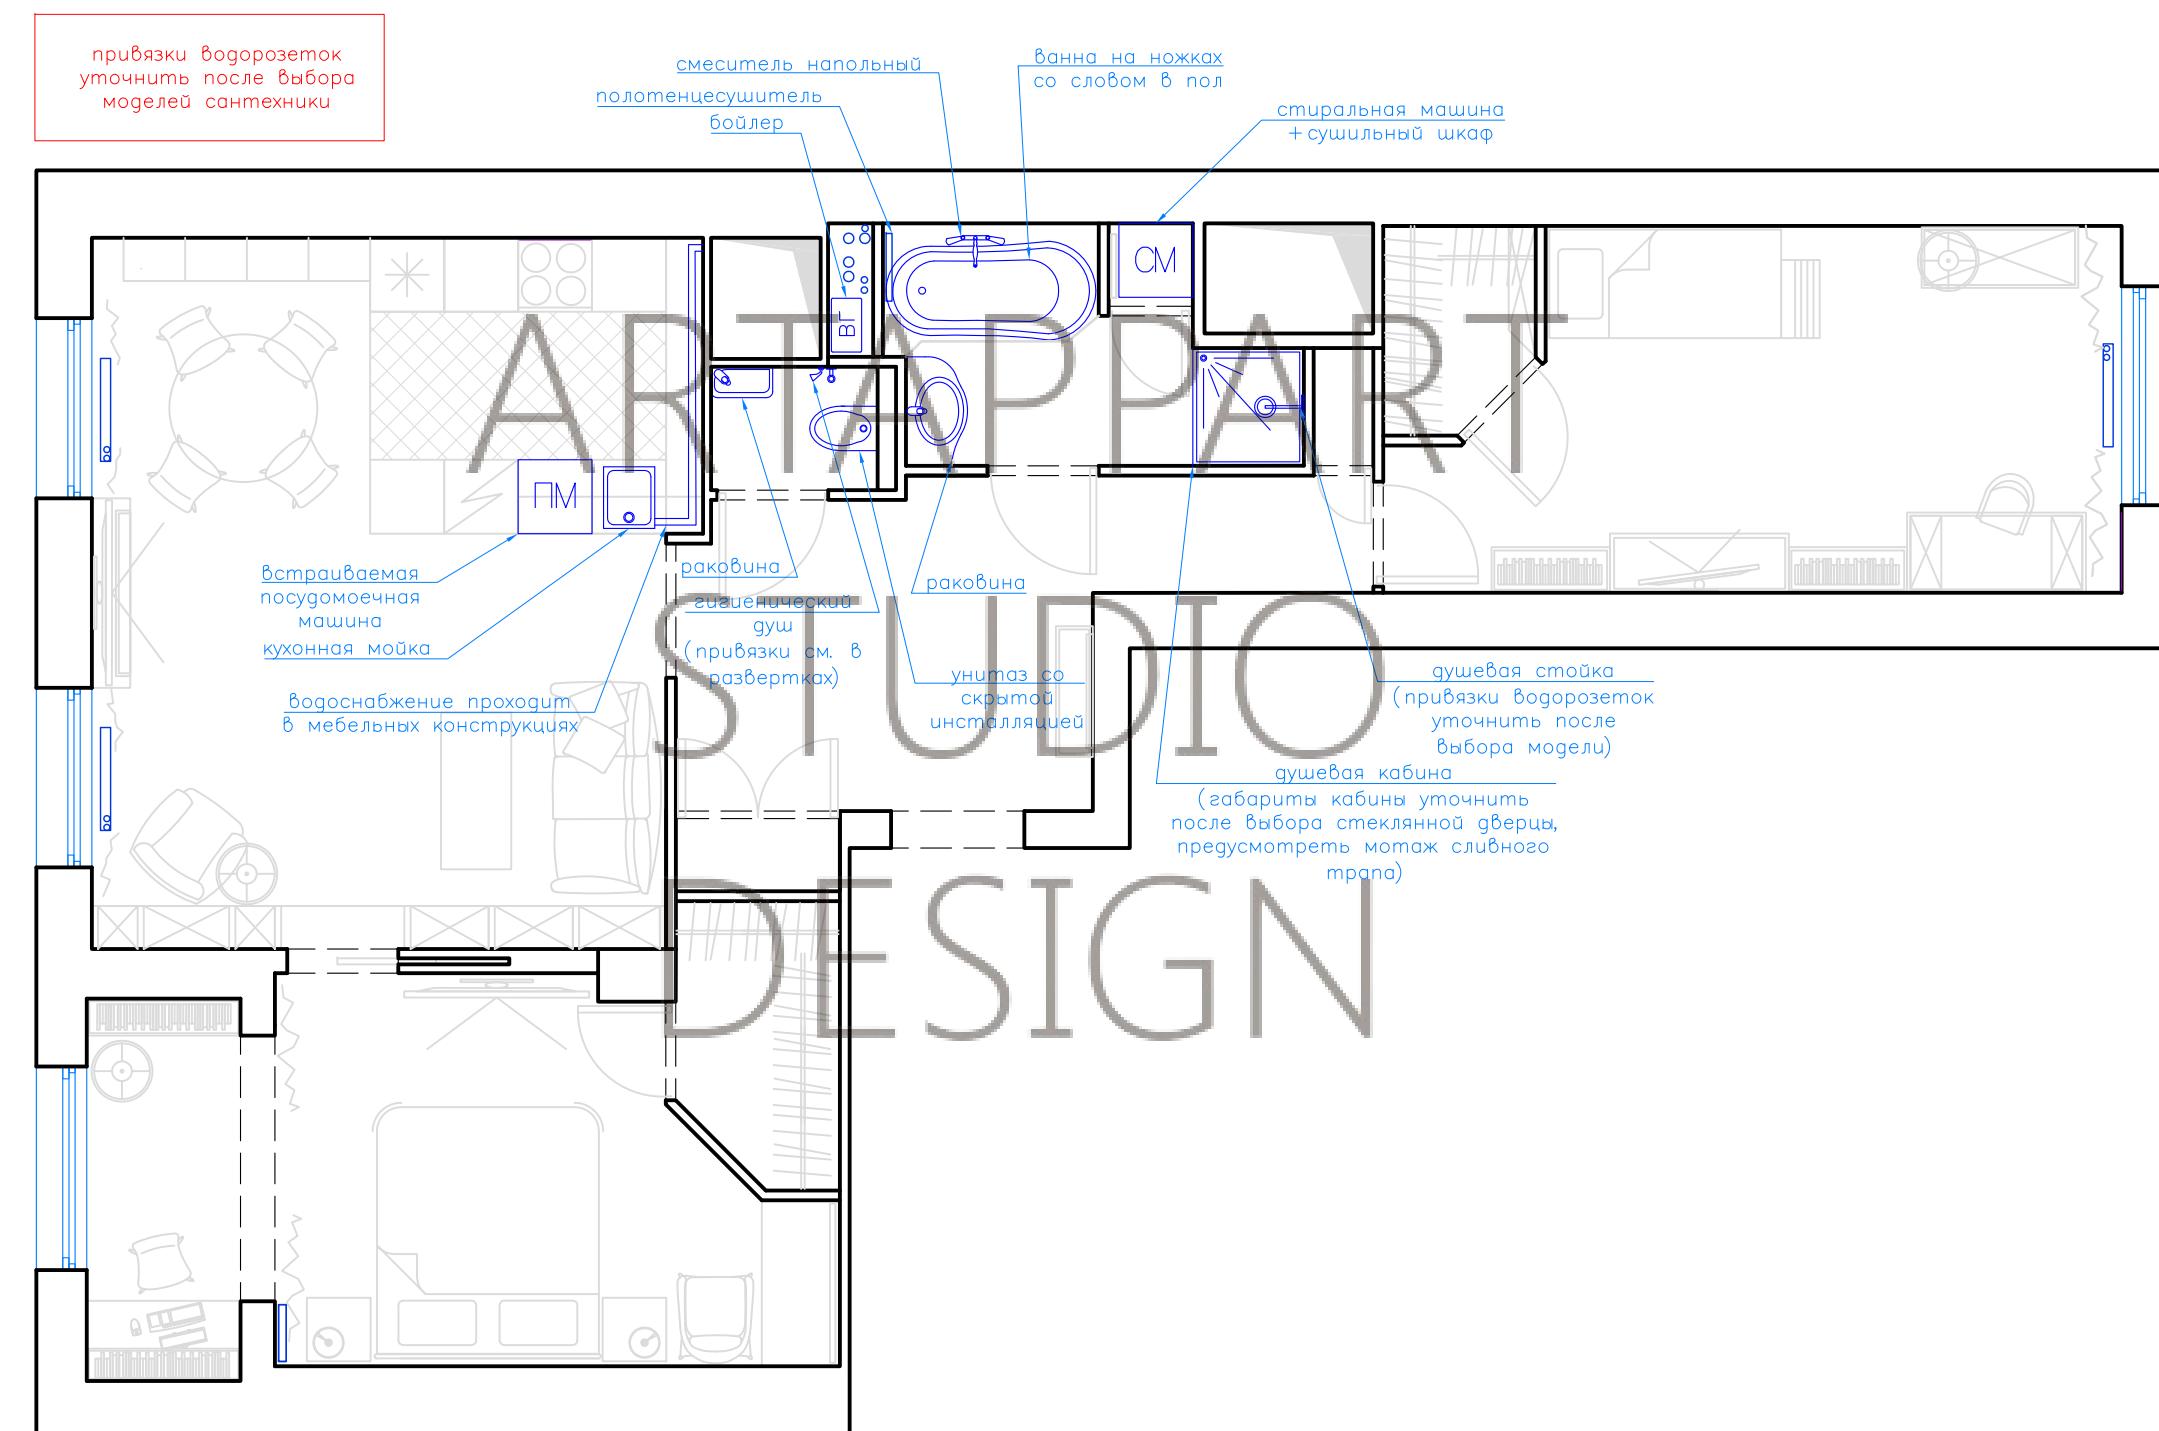

Изм.	Кол. уч.	Листм	№ док.	Подп.	Дата	Разработка дизайн-проекта квартиры	Стадия	Листм	Листов
Заказчик					2017				
Разработ.					2017	План расположения сан.тех оборудования	P		
						M 1:60			




ARTAPPART  
DESIGN  
STUDIO

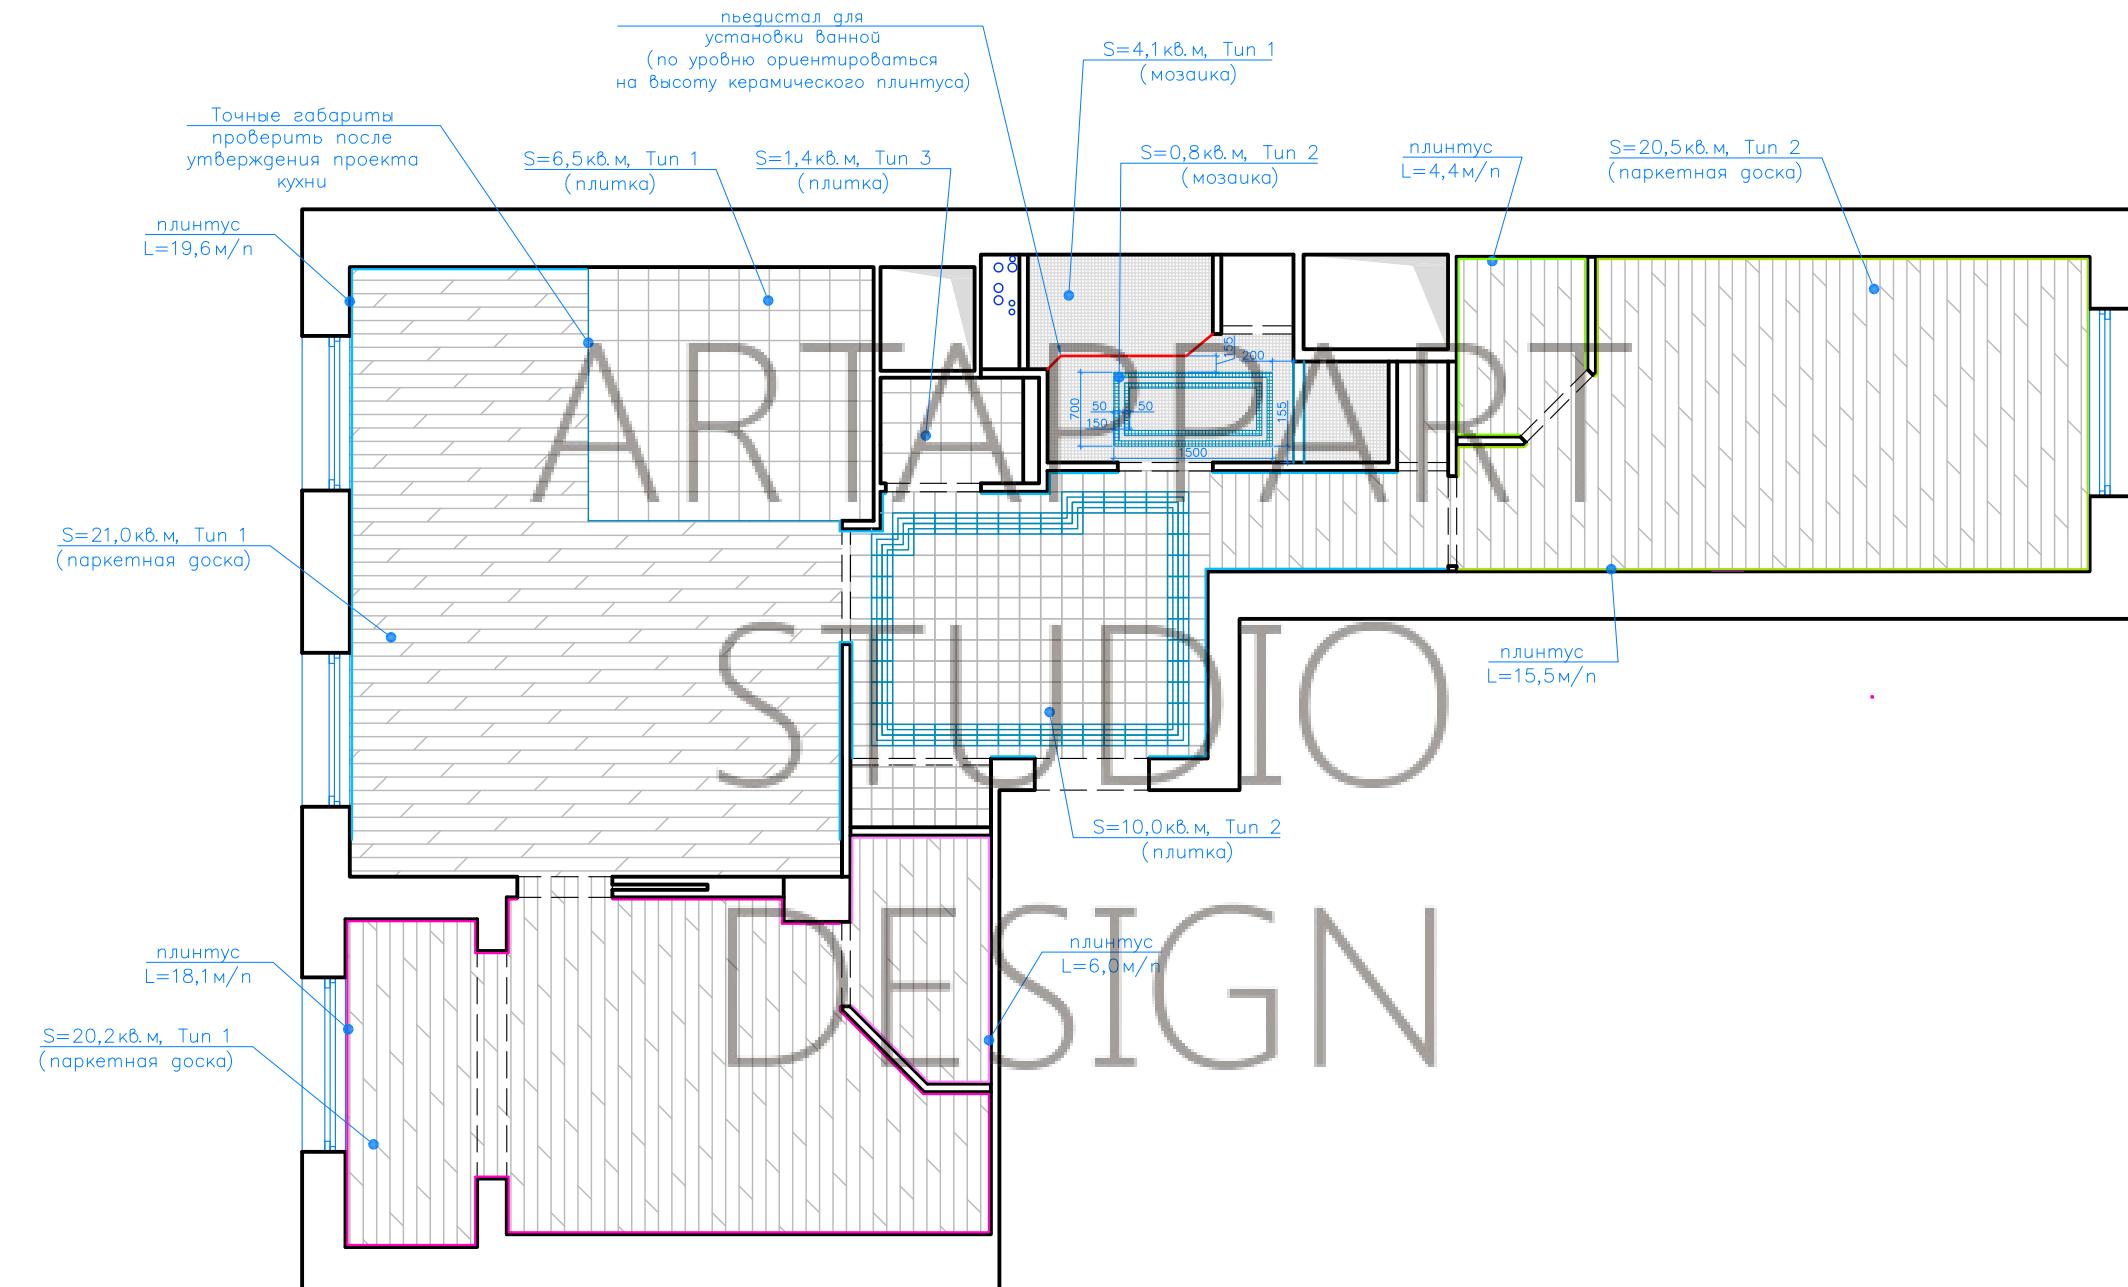

### Примечание:

Площади покрытий даны без учета запасов

Изм.	Кол. уч.	Листм	№ док.	Подп.	Дата	Разработка дизайн-проекта квартиры	Статус	Листм	Листов
Заказчик					2017		P		
Разработ.					2017	План полов и напольных покрытий М 1:60		ARTAPPART DESIGN STUDIO	

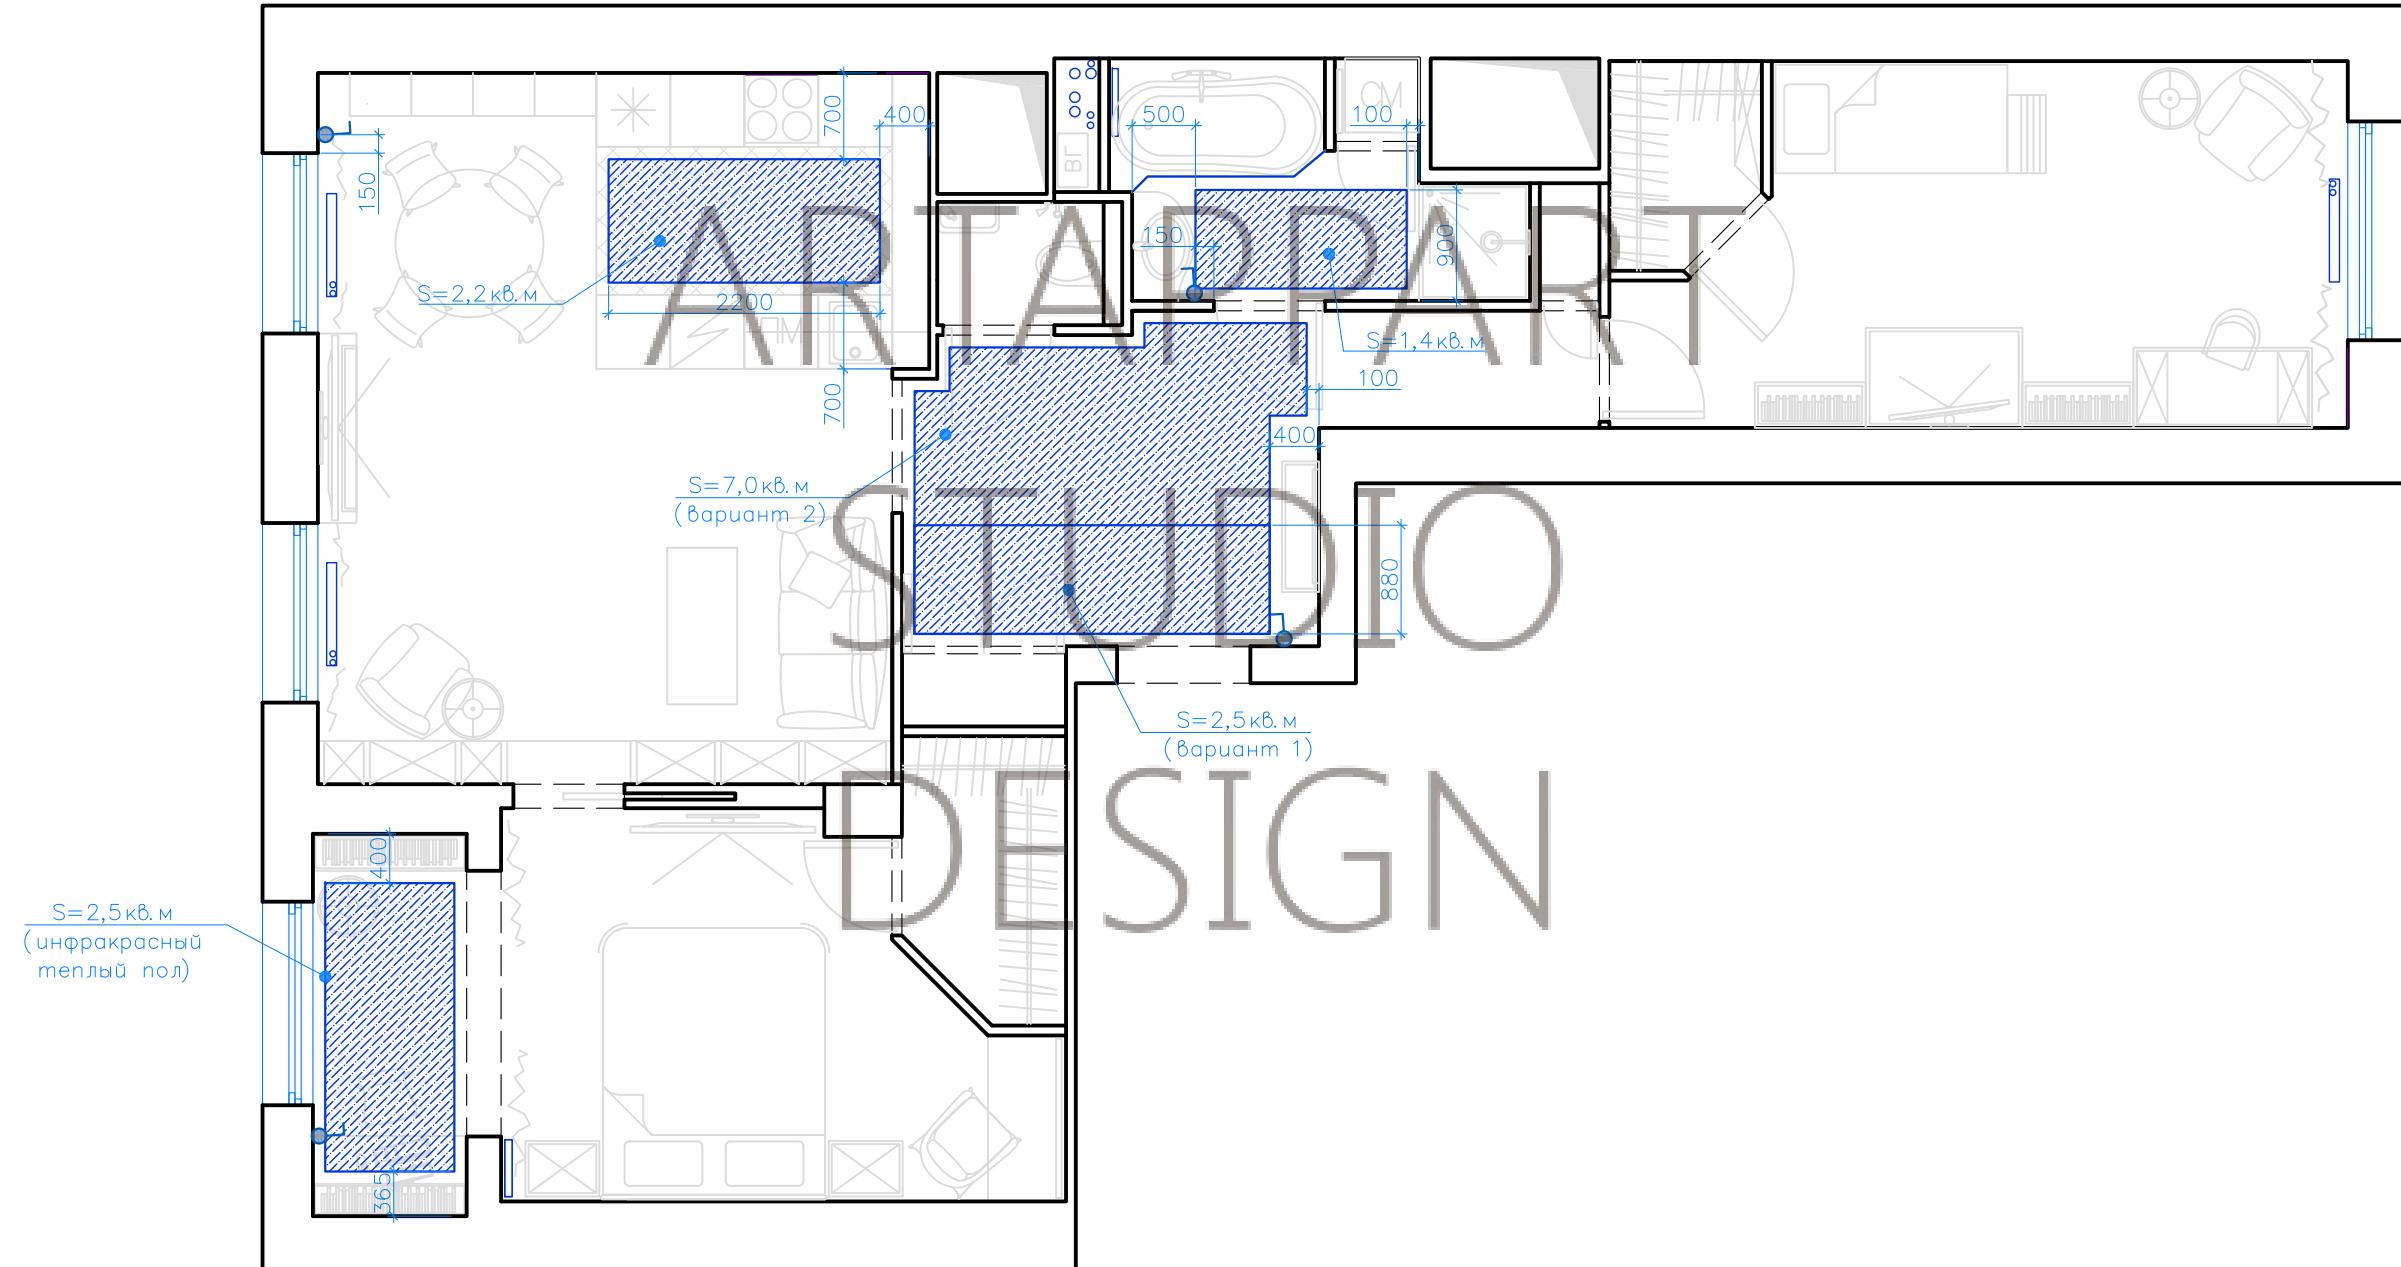

Условные обозначения:

— регулятор электрического теплого пола

Примечание:

- Границы расположения теплого пола удалены от напольных элементов мебели, стен и прочих конструкций на 100мм, если не указано иное.
- Терморегуляторы расположить на высоте 400мм на оси электроустановочного оборудования, если не указано иное.
- Все терморегуляторы установить посередине простенка, либо на расстоянии 250 мм от угла, если не указано иное.

Изм.	Кол. уч.	Лист	№ док.	Подп.	Дата	Разработка дизайн-проекта квартиры	Стадия	Лист	Листов
Заказчик					2017				
Разработ.					2017				
						План "теплых полов"			
						M 1: 60			



ARTAPPART  
DESIGN  
STUDIO

Согласовано

Инф. № подл.	Погр. и зата	Взам. инф.
--------------	--------------	------------

## ловные обозначения


— подшивной потолок ГК

— натяжной потолок

### Примечание:

1. Все покрытия белого цвета, если не указано иное
  2. За исходный уровень принят уровень потолка с учетом проведенных мероприятий по выравниванию и звукоизоляции
  3. Натяжные потолки монтируются на минимально возможном расстоянии от перекрытия, если не указано иное.

Изм.	Кол. уч.	Листм	№ док.	Погр.	Дата	
Заказчик			2017		Разработка дизайн-проекта квартиры	Стадия
Разработ.			2017			Листм
					План потолков М 1: 60	Листов
						ARTAPPART DESIGN STUDIO

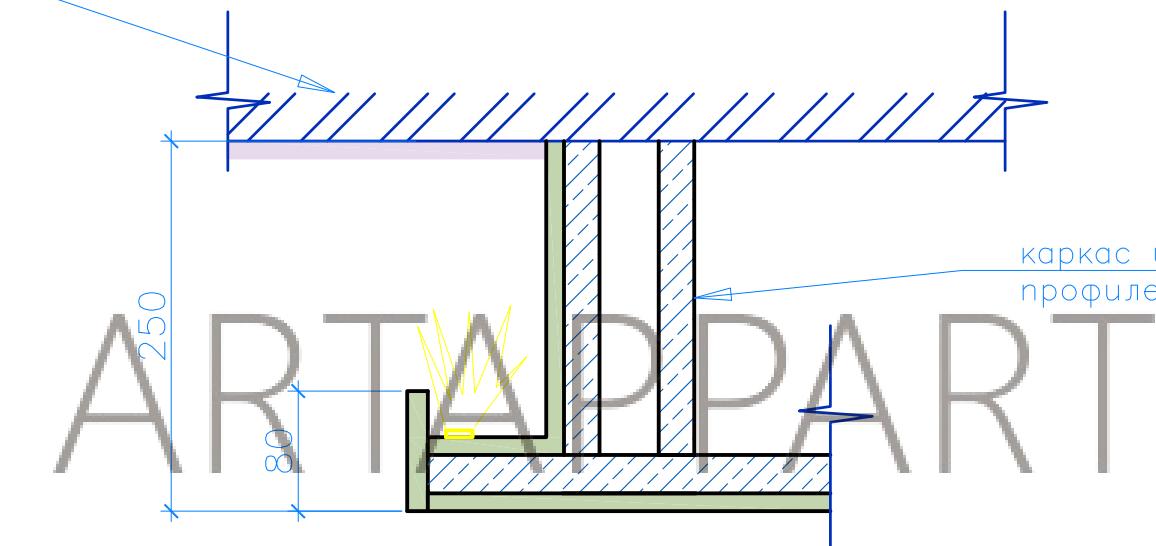

# STUDIO


# DESIGN

## Условные обозначени




— окраска

## Устройство паза для светоизодной ленты:

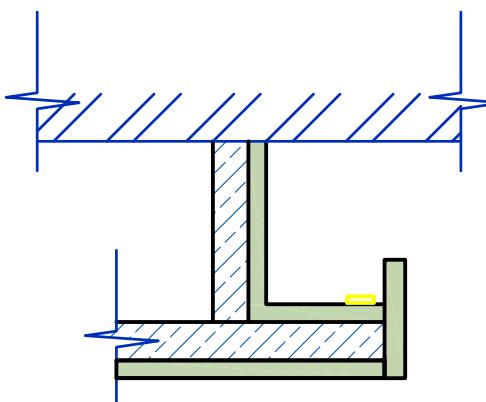

Примечание: за исходный уровень принять уровень перекрытия потолика после проведенных мероприятий по звукоизоляции и пр.

Изм.	Кол. уч.	Листм	№ док.	Подп.	Дата	
Заказчик			2017			
Разработ.			2017			

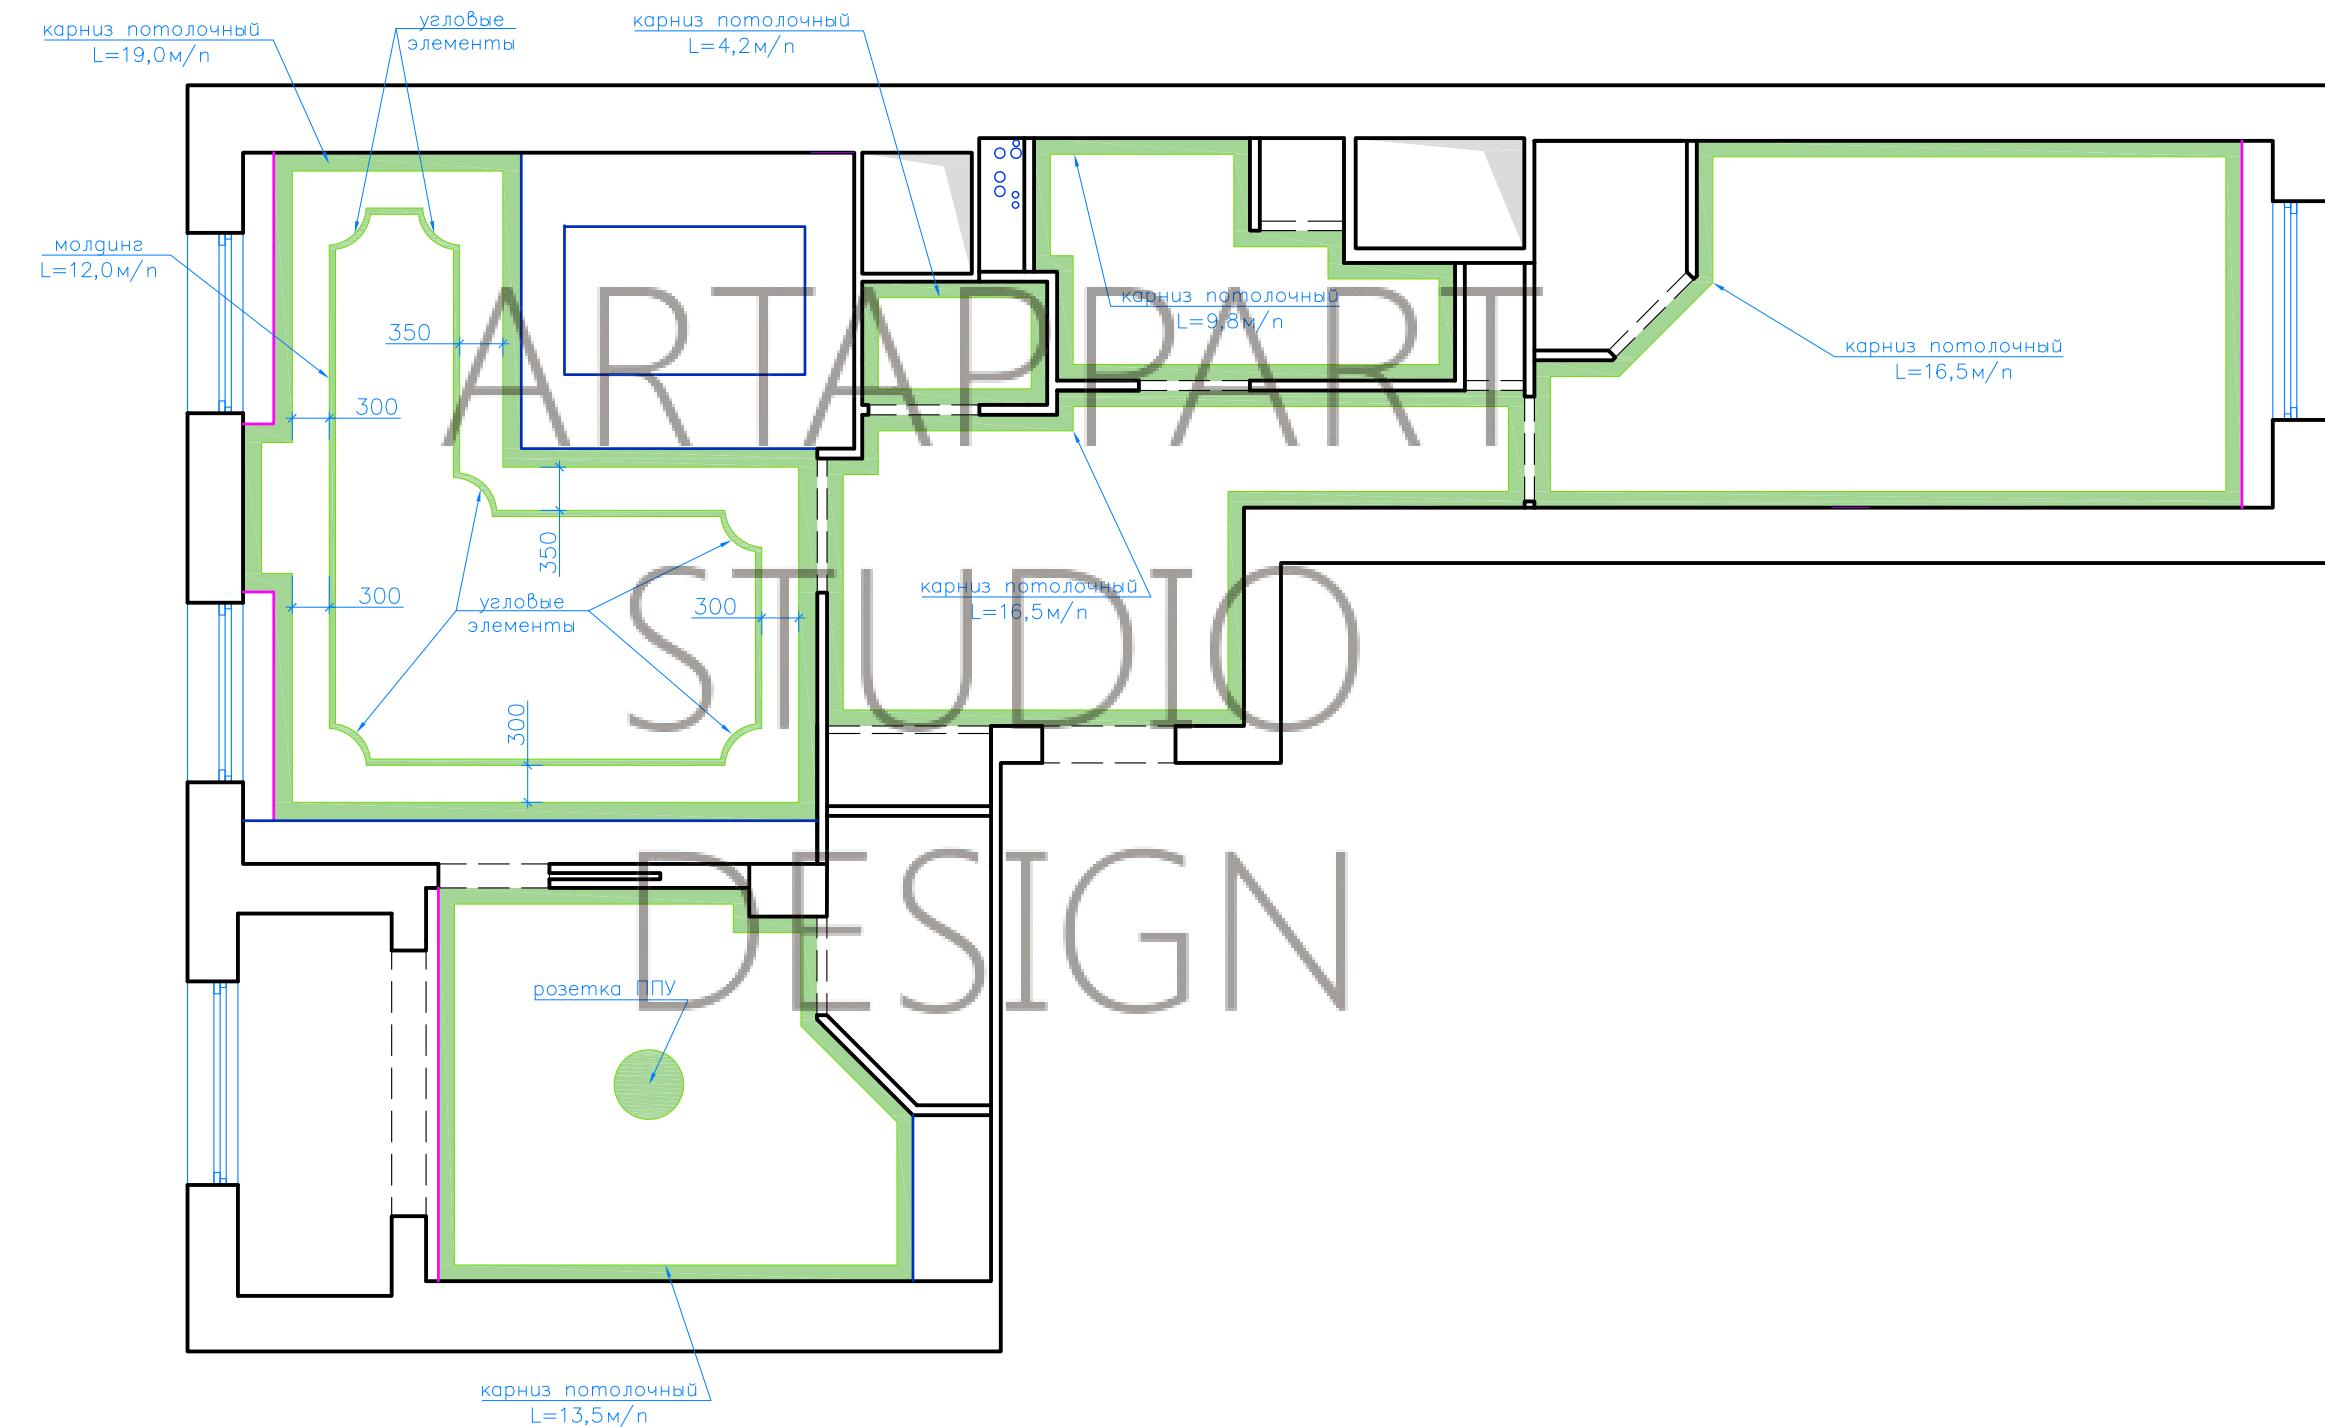


## Условные обозначения

## – ППУ декор

Примечание: весь пенополиуретановый декор белого цвета, если не указано иное


Изм.	Кол. уч.	Листм	№ док.	Подп.	Дата	
Заказчик				2017	Разработка дизайн-проекта квартиры	Стадия
Разработ.				2017		Листм
					План размещения ППУ декора М 1:60	Листовъ

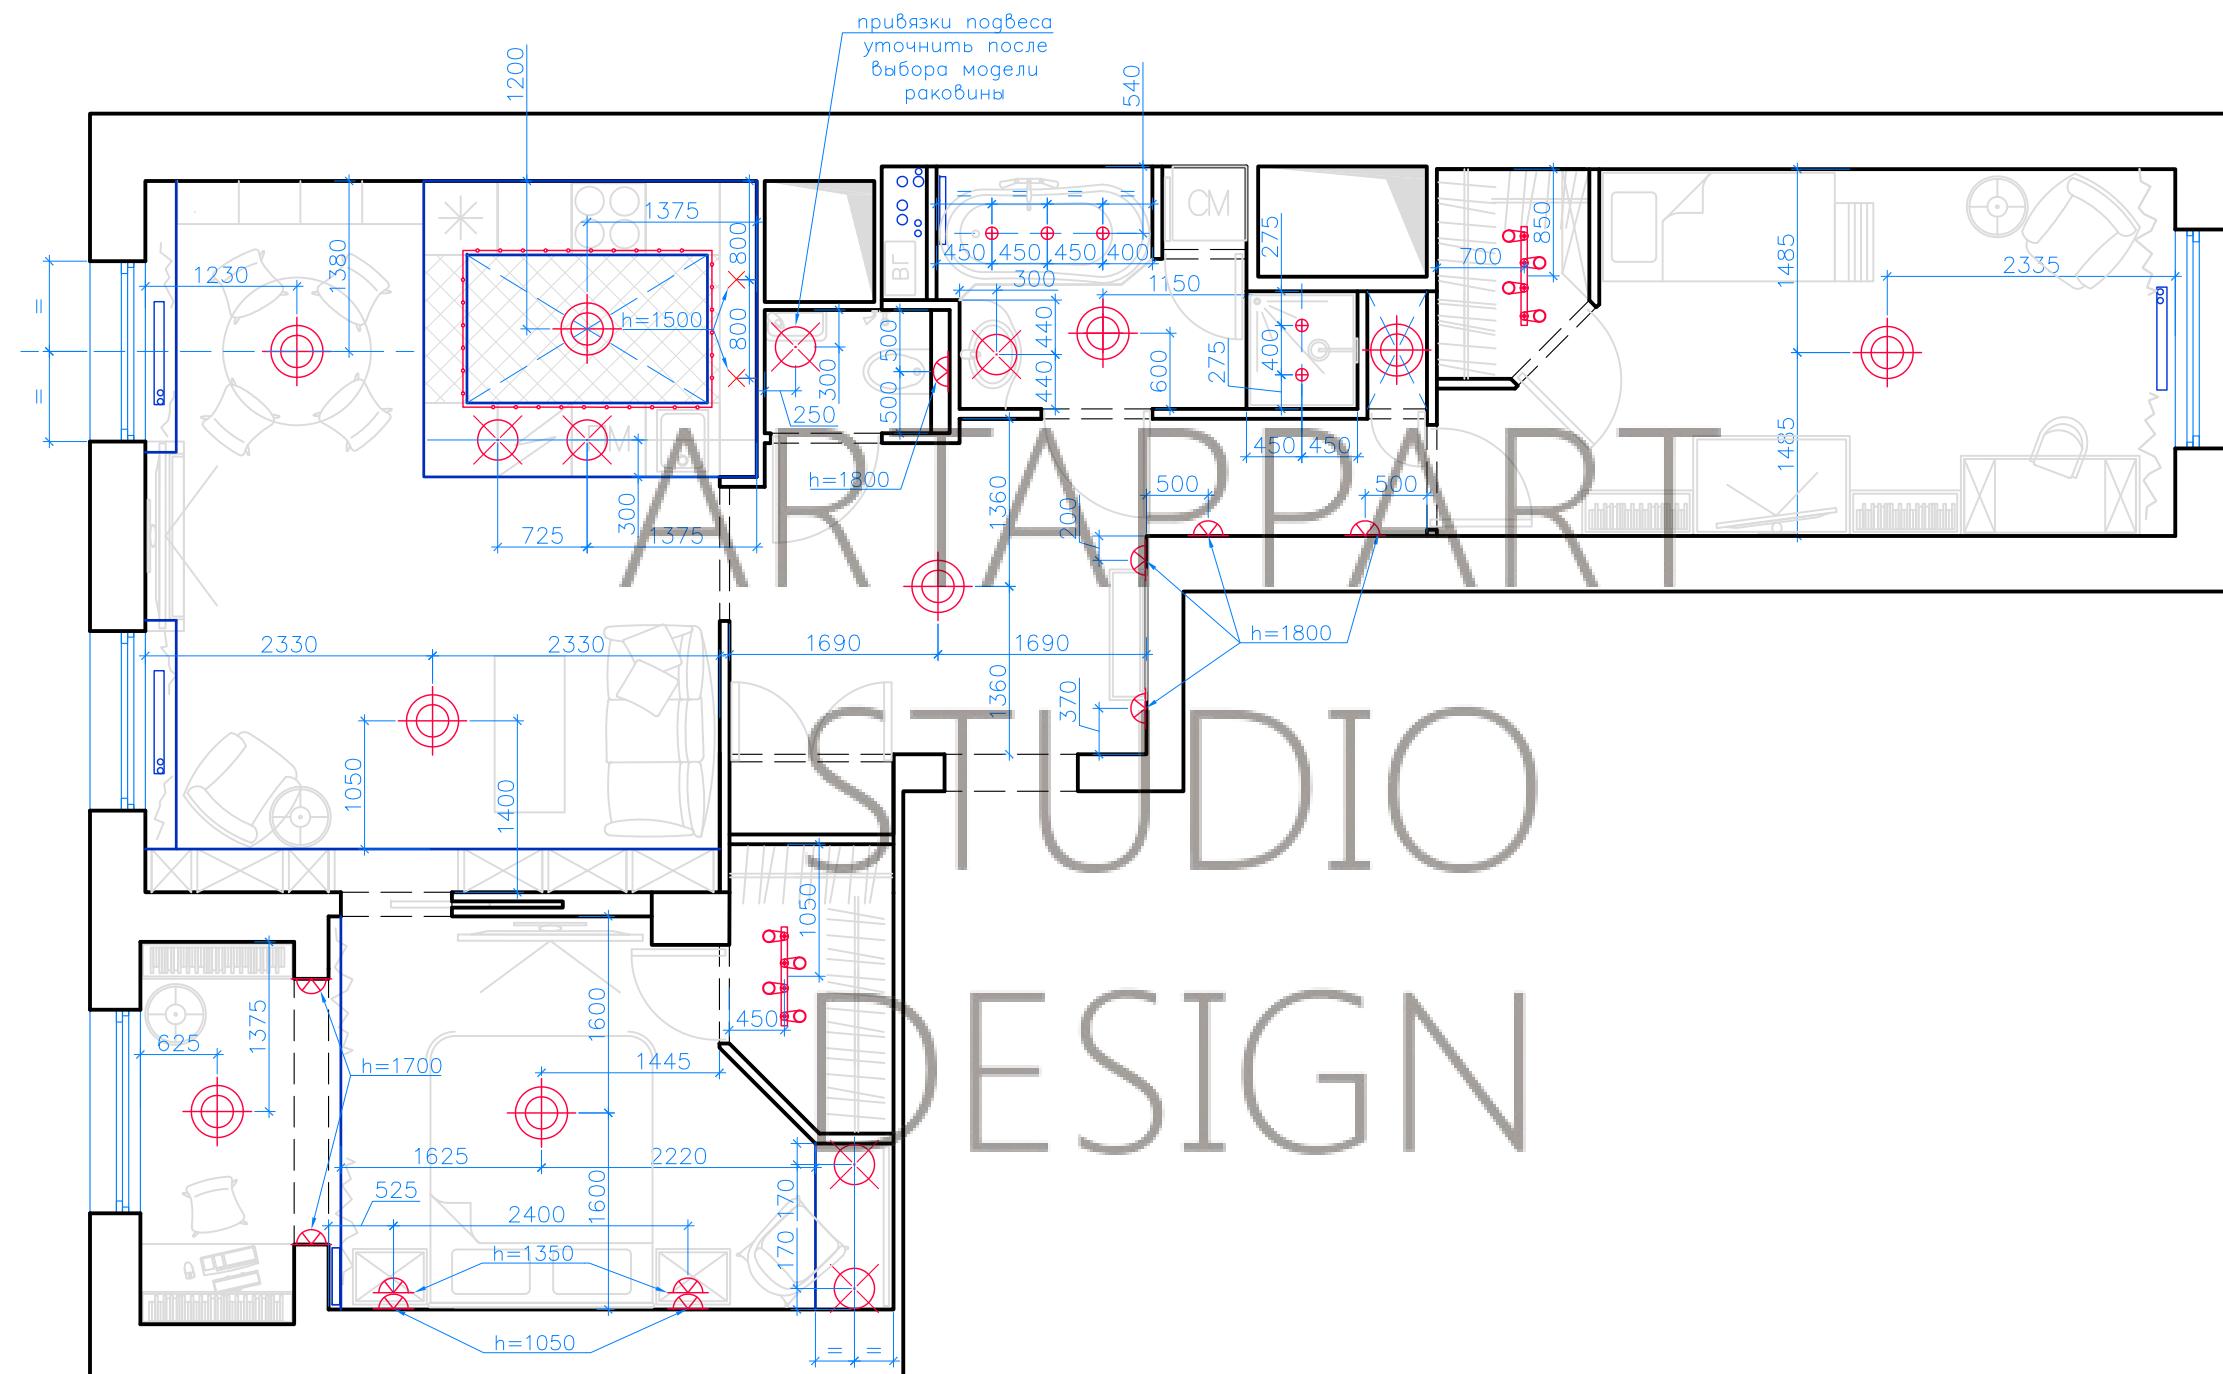

Изм.	Кол. уч.	Лист	№ док.	Подп.	Дата	Разработка дизайн-проекта квартиры	Стадия	Лист	Листов
Заказчик					2017		P		
Разработ.					2017	План привязки осветительных приборов			
						M 1:60			



ARTAPPART  
DESIGN  
STUDIO

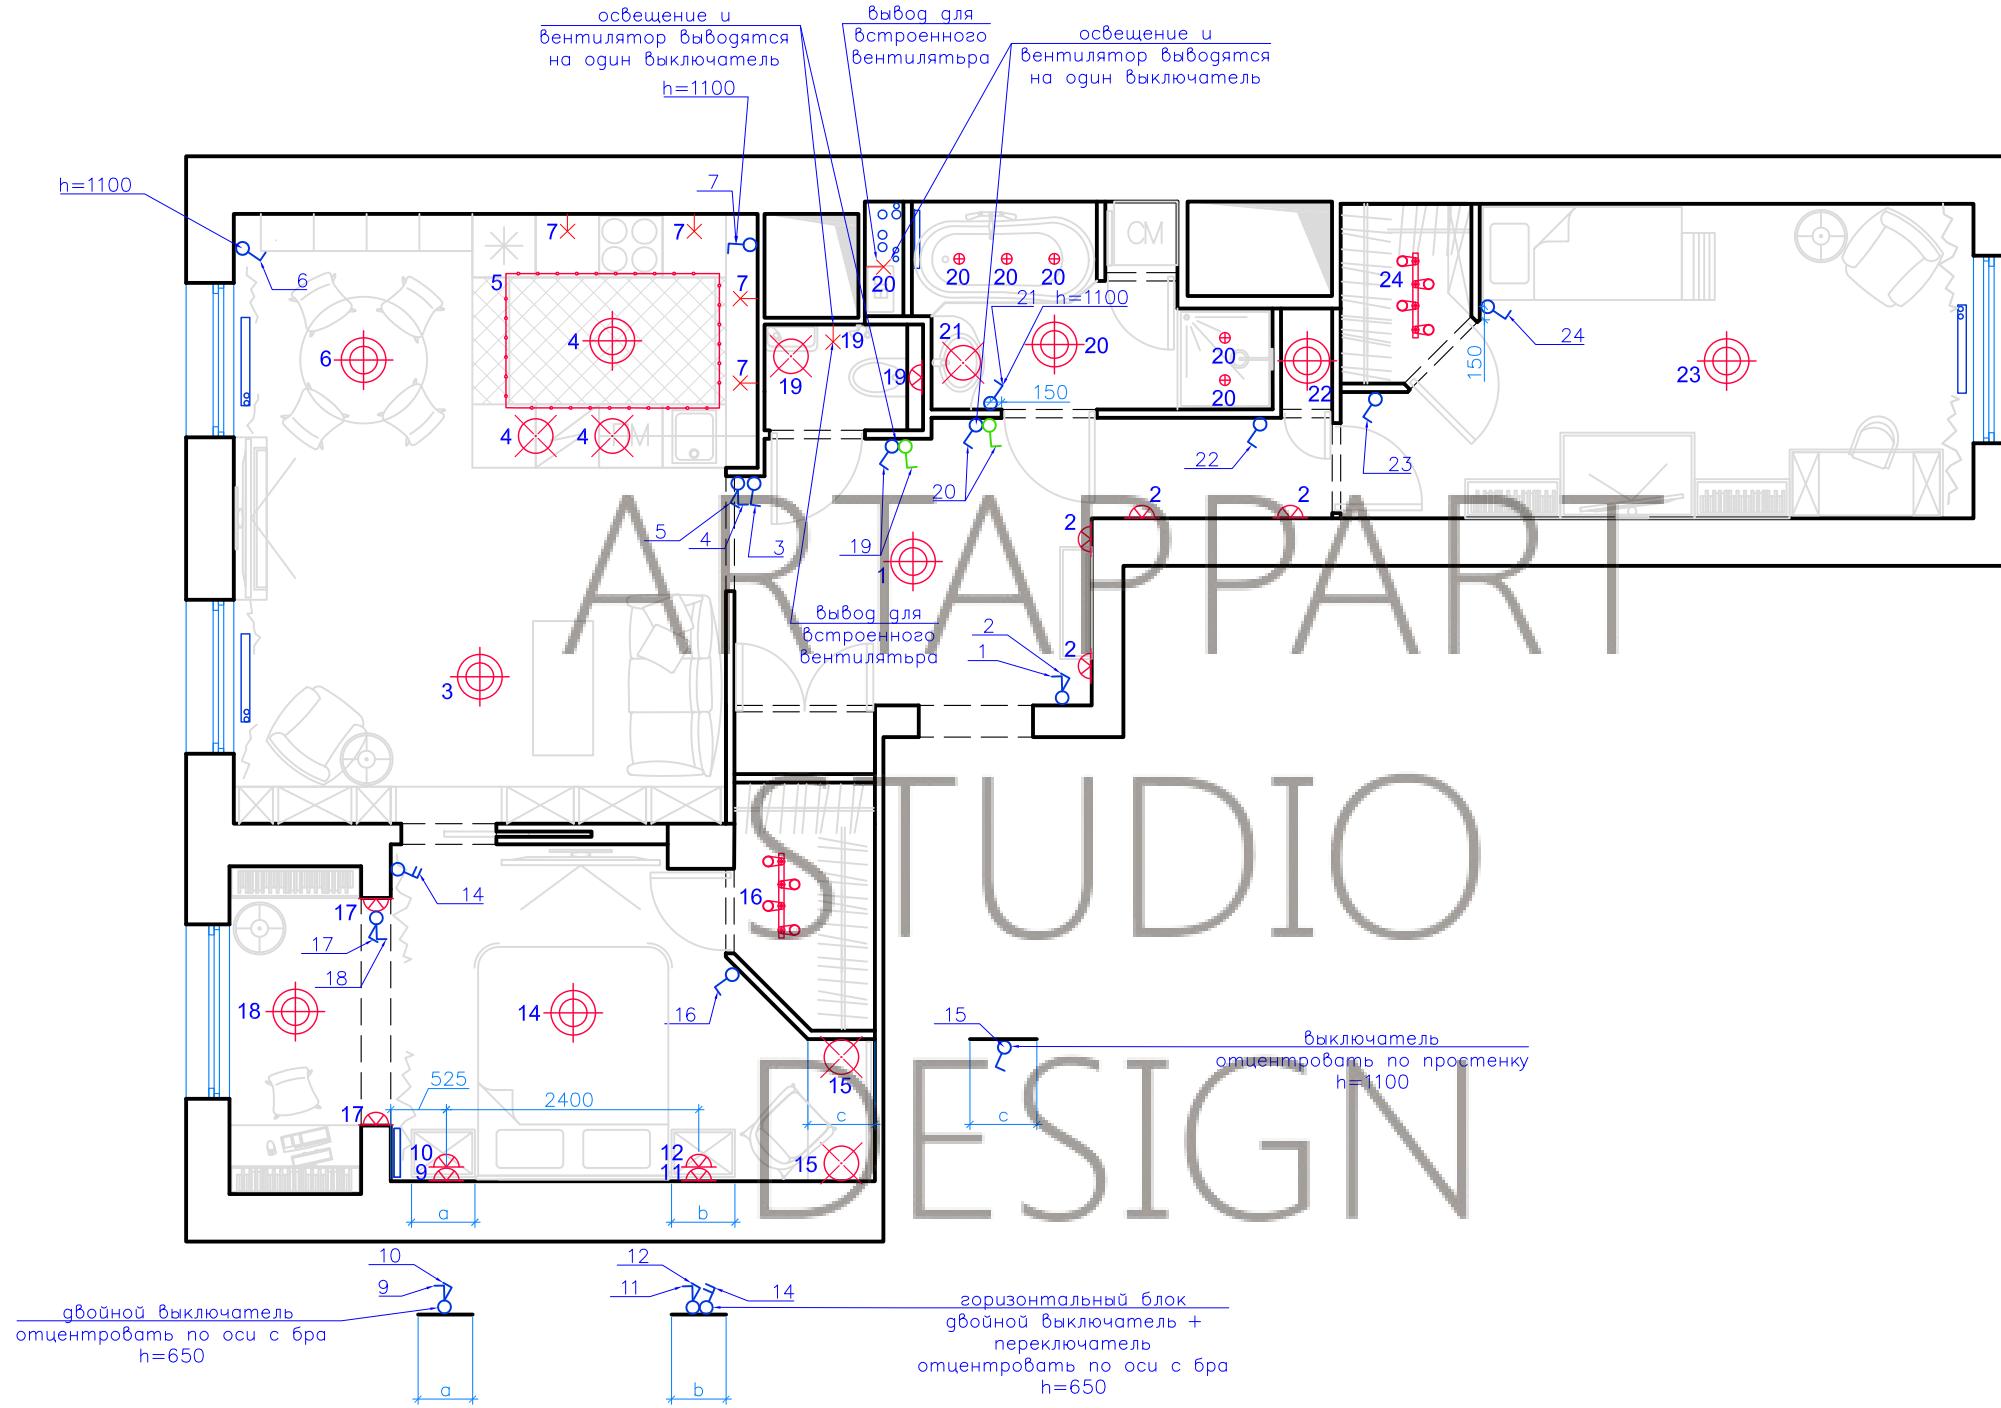

Условные обозначения:


- выключатель (1-но клавишный)
- выключатель (2-ух клавишный)
- диммер
- вкл. Вентиляции

Примечание:

1. Все выключатели установить посередине просенка либо на расстоянии 250мм от угла, если не указано иное;
2. Высота до оси выключателя(—лей) 900мм от УЧП, если не указано иное;
3. Количество номеров групп светильников у выключателя определяет его тип: 1-но / 2-ух клавишный;
4. Привязки даны в мм от УЧП до осей приборов.
5. Для возможности редактирования рекомендуется оставлять выводы достаточной длины.

Изм.	Кол. уч.	Листм	№ док.	Подп.	Дата	Разработка дизайн-проекта квартиры	Стадия	Листм	Листов
Заказчик					2017				
Разработ.					2017				
						План разводки осветительных приборов на выключатели			

ARTAPPART DESIGN STUDIO

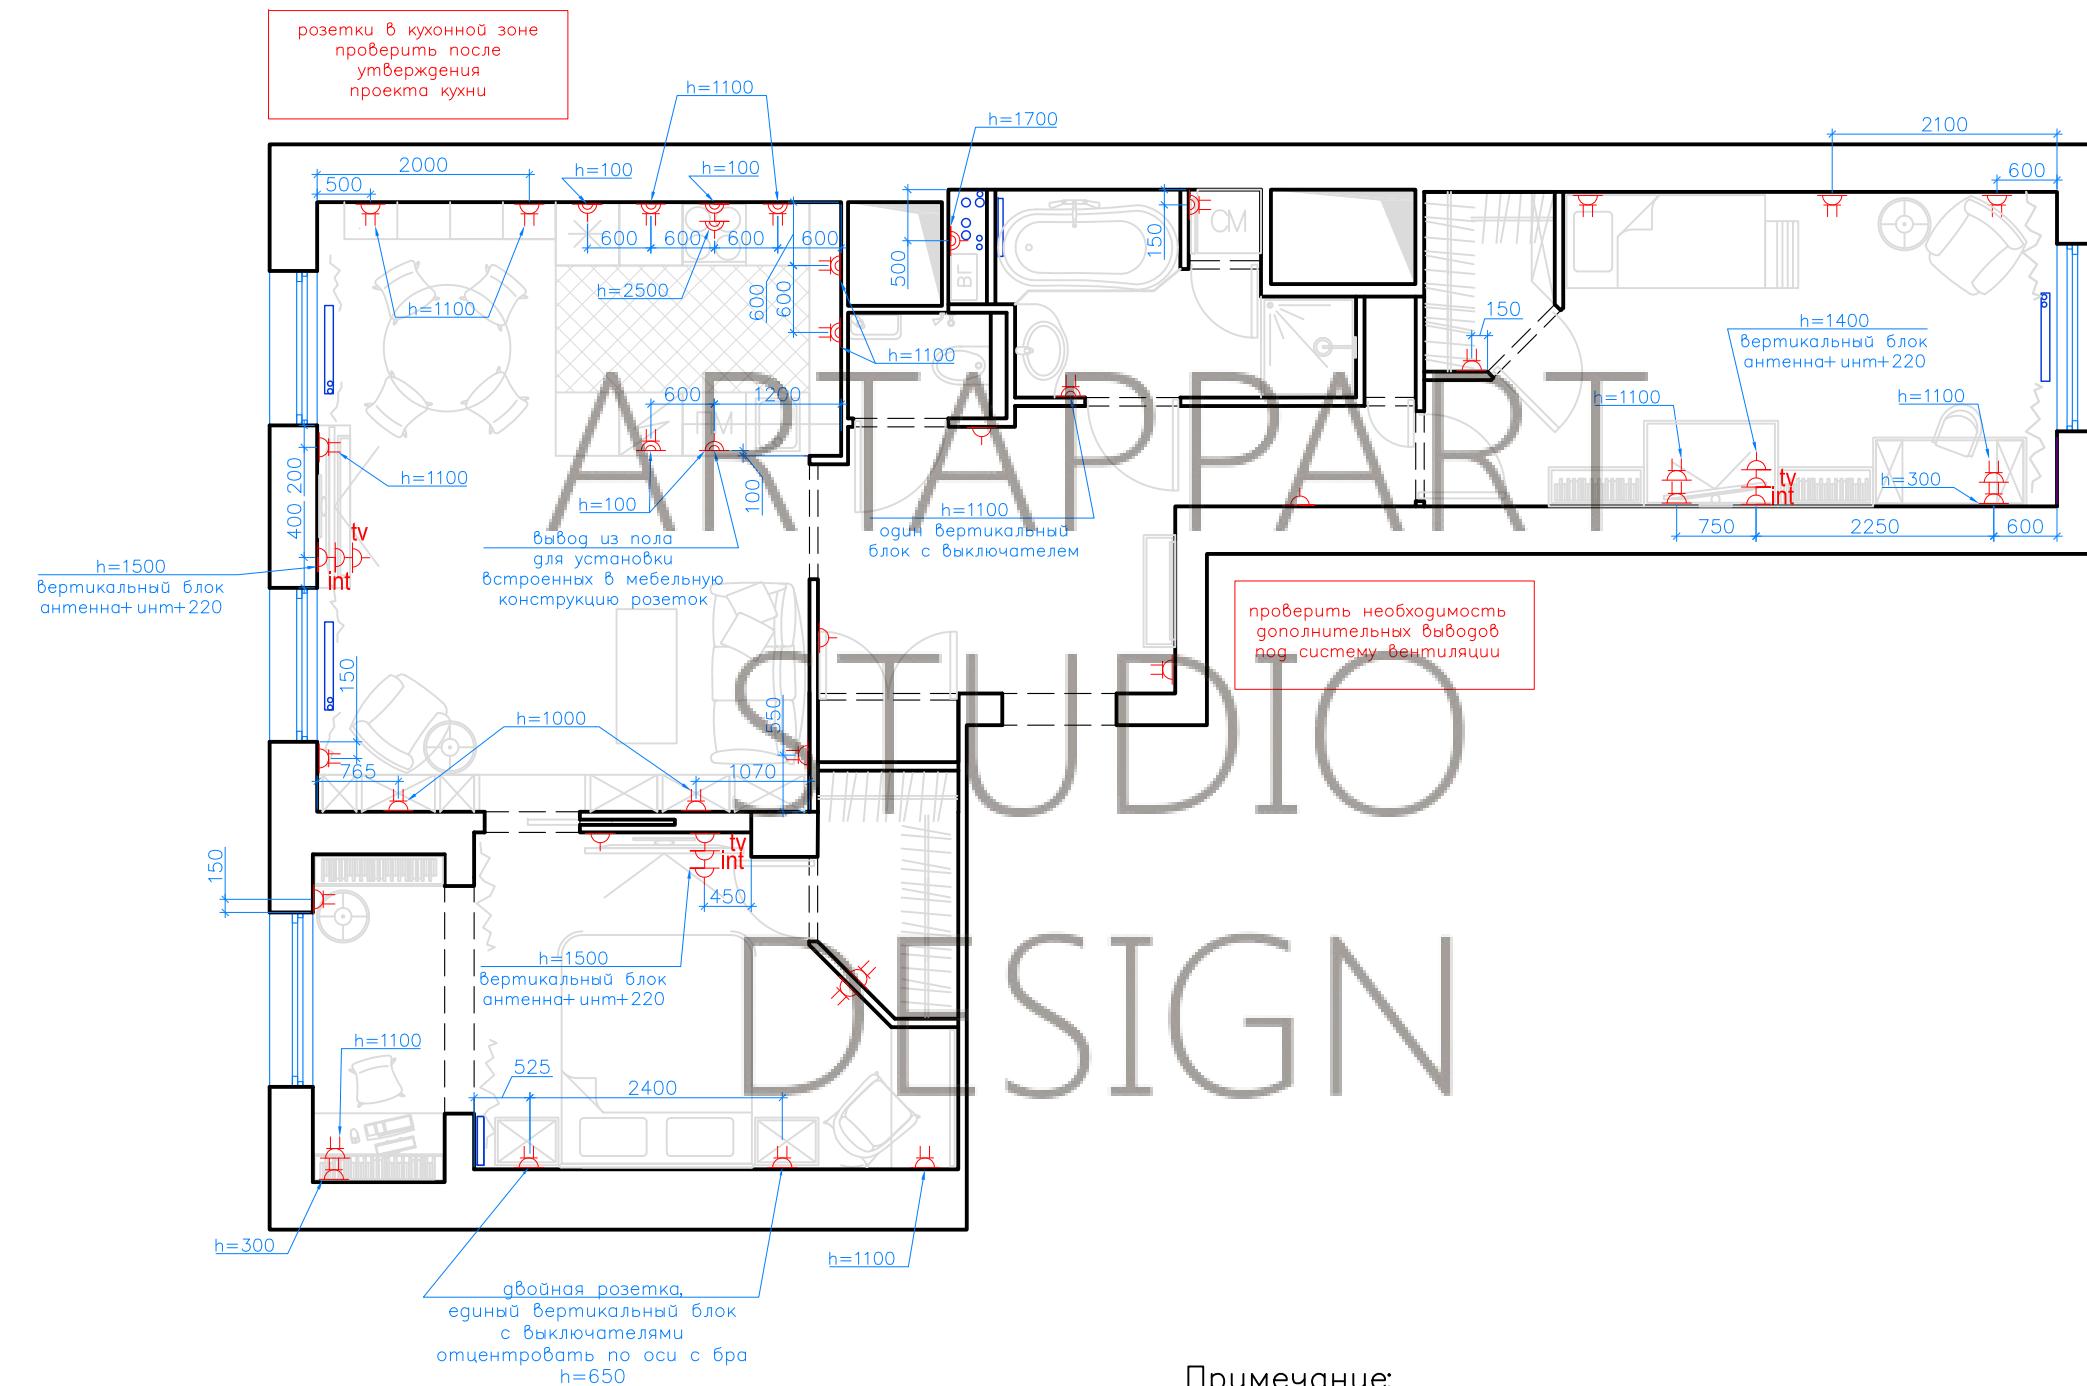


Примечание:

1. Все розетки, кроме обозначенных, установить на высоте 300 мм от УЧП;
2. Розетки располагать посередине просянка либо на расстоянии 250мм от угла, если привязки не указаны;
3. Привязки даны в мм от УЧП до осей приборов.
4. Для возможности редактирования рекомендуется оставлять выводы достаточной длины.



Изм.	Кол. уч.	Лист	№ док.	Подп.	Дата	Разработка дизайн-проекта квартиры	Стадия	Лист	Листов
Заказчик					2017				
Разработ.					2017				
						План электрики и электропроводов М 1:60	Р		

ARTAPPART DESIGN STUDIO

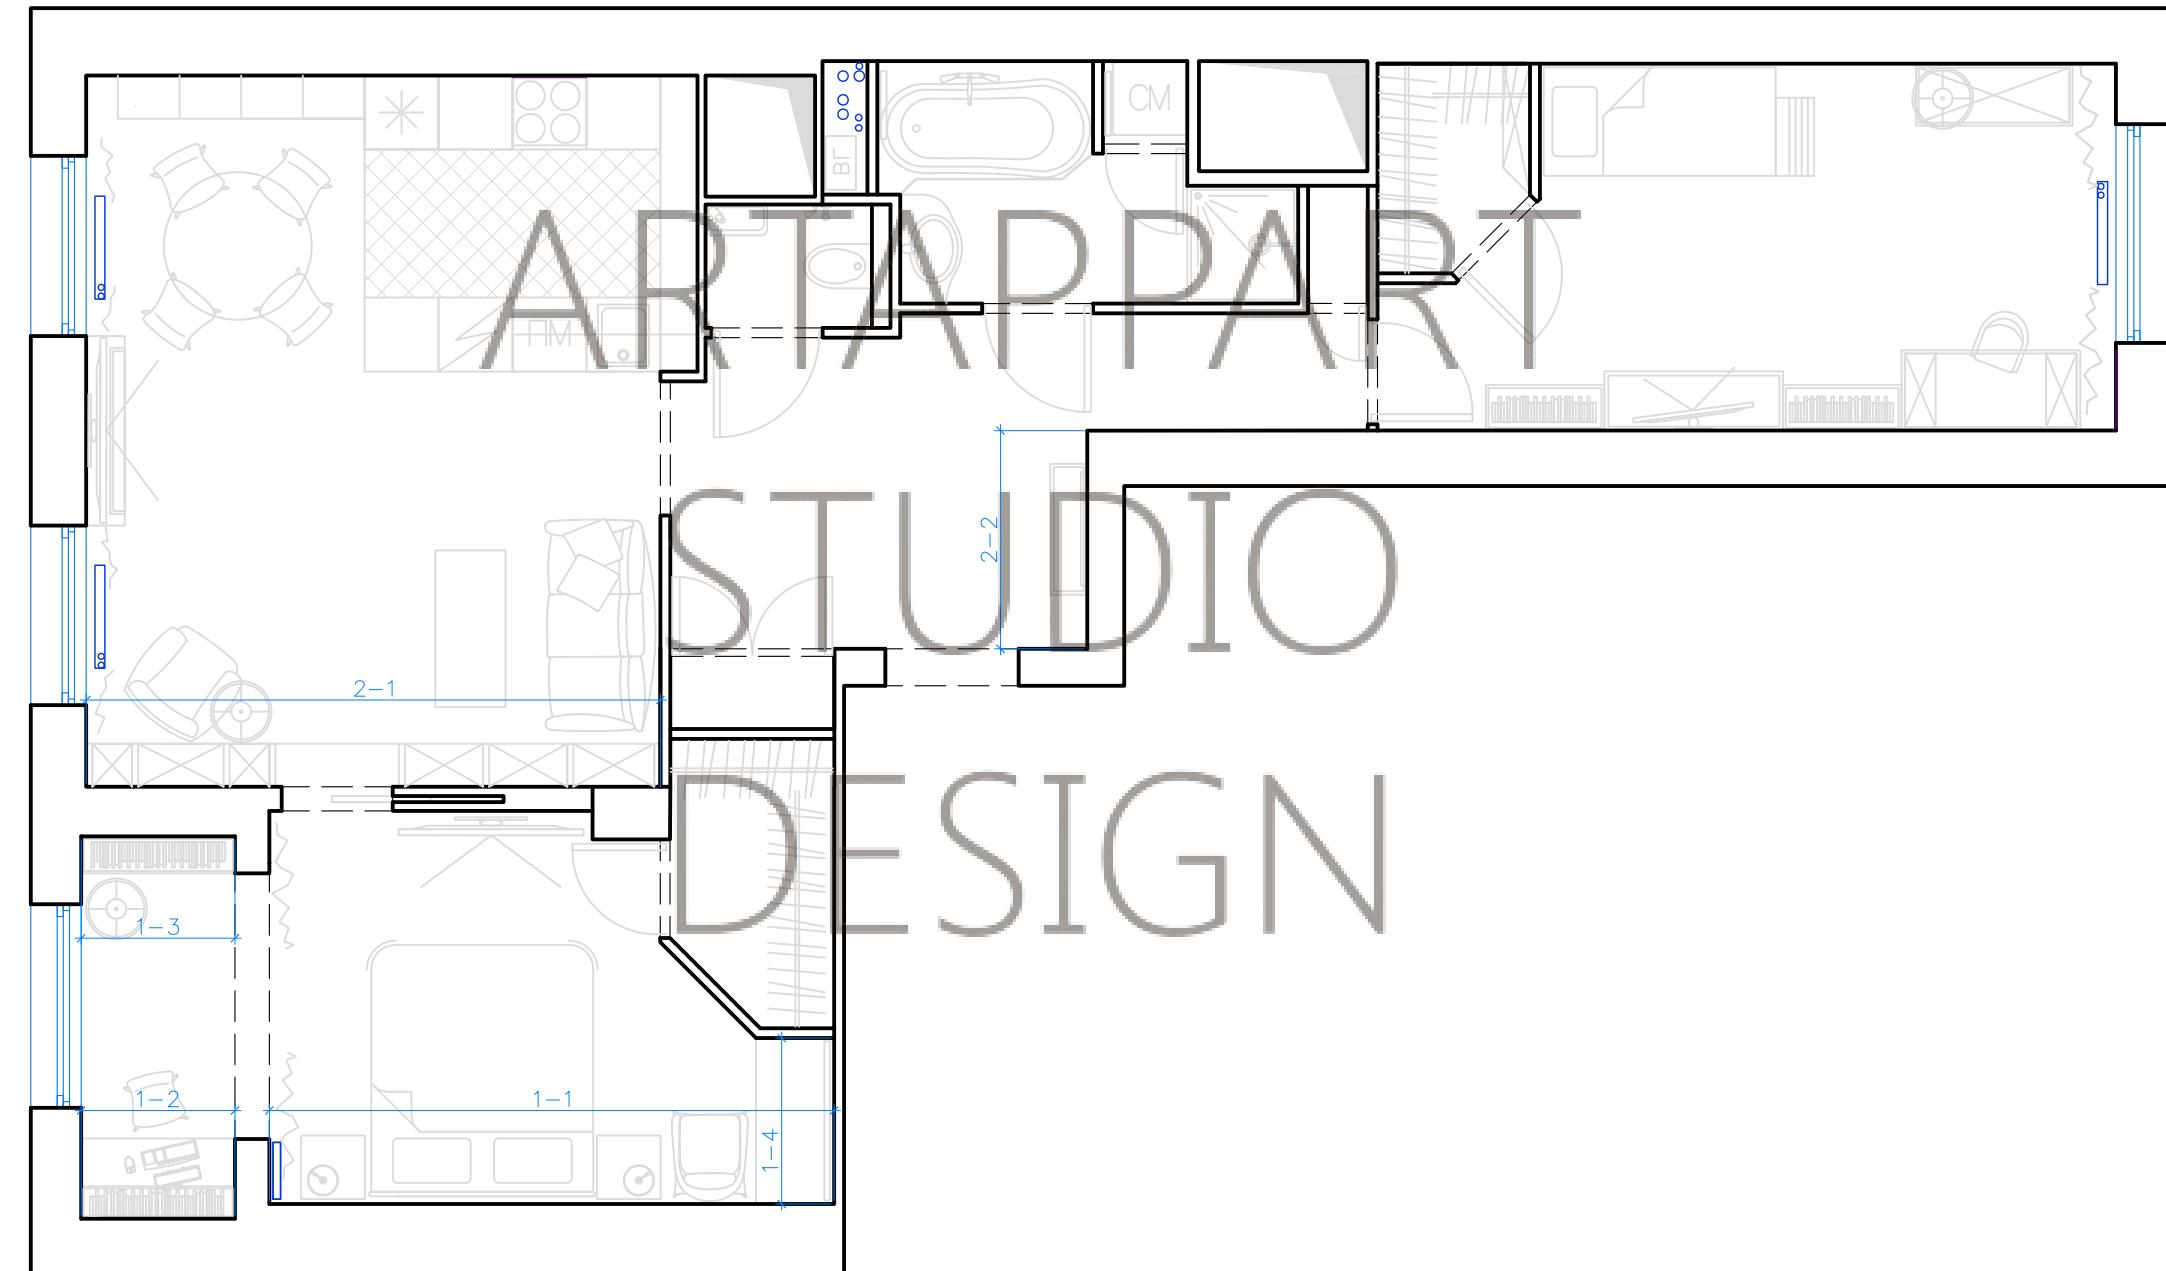


Инв. № подп.	Подп. и дата	Взам. инв.

Изм.	Кол. уч.	Листм	№ док.	Подп.	Дата	Разработка дизайн-проекта квартиры	Стадия	Листм	Листов
Заказчик					2017		P		
Разработ.					2017	Схема обозначения разверток	M 1:60		
						ARTAPPART DESIGN STUDIO			

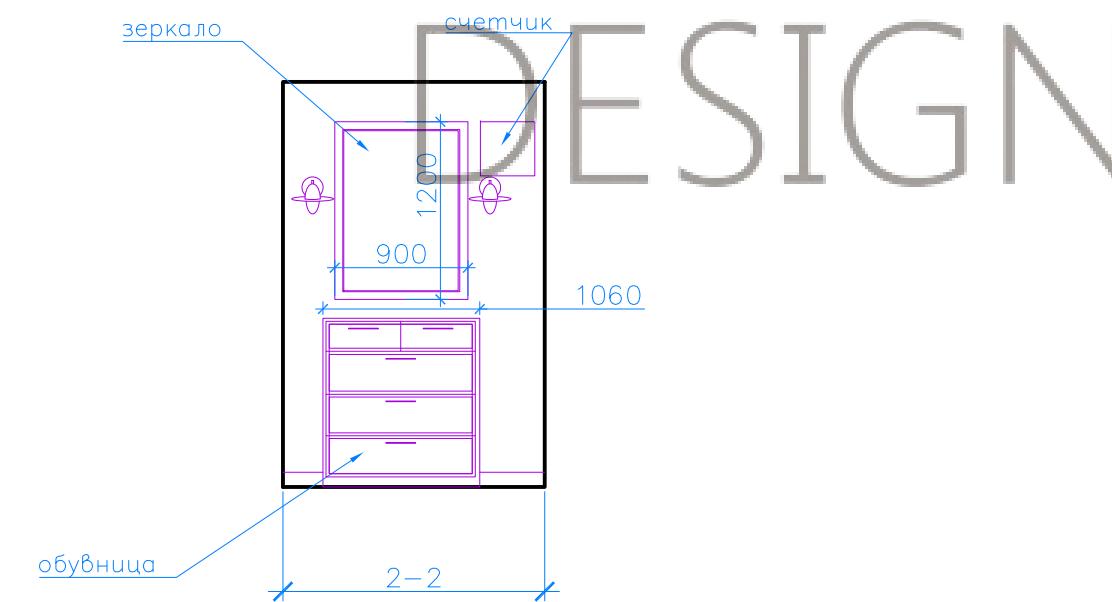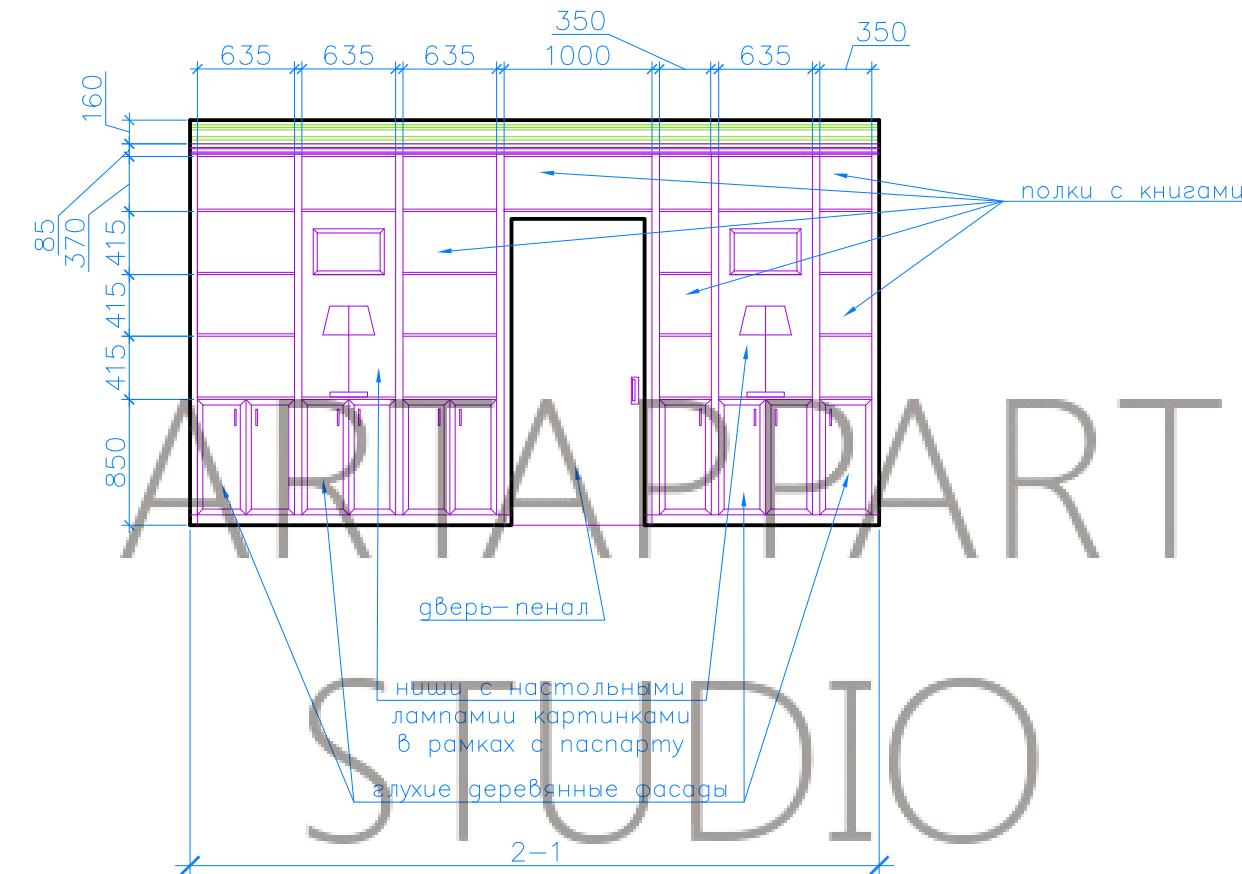


Изм.	Кол. уч.	Листм	№ док.	Подп.	Дата	Разработка дизайн-проекта квартиры		
Заказчик						Стадия	Листм	Листов
Разработ.					2017	P		
					2017			
Развертки по стенам М 1:50								ARTAPPART DESIGN STUDIO

Инв. № подп.	Подп. и дата	Взам. инв.	Согласовано

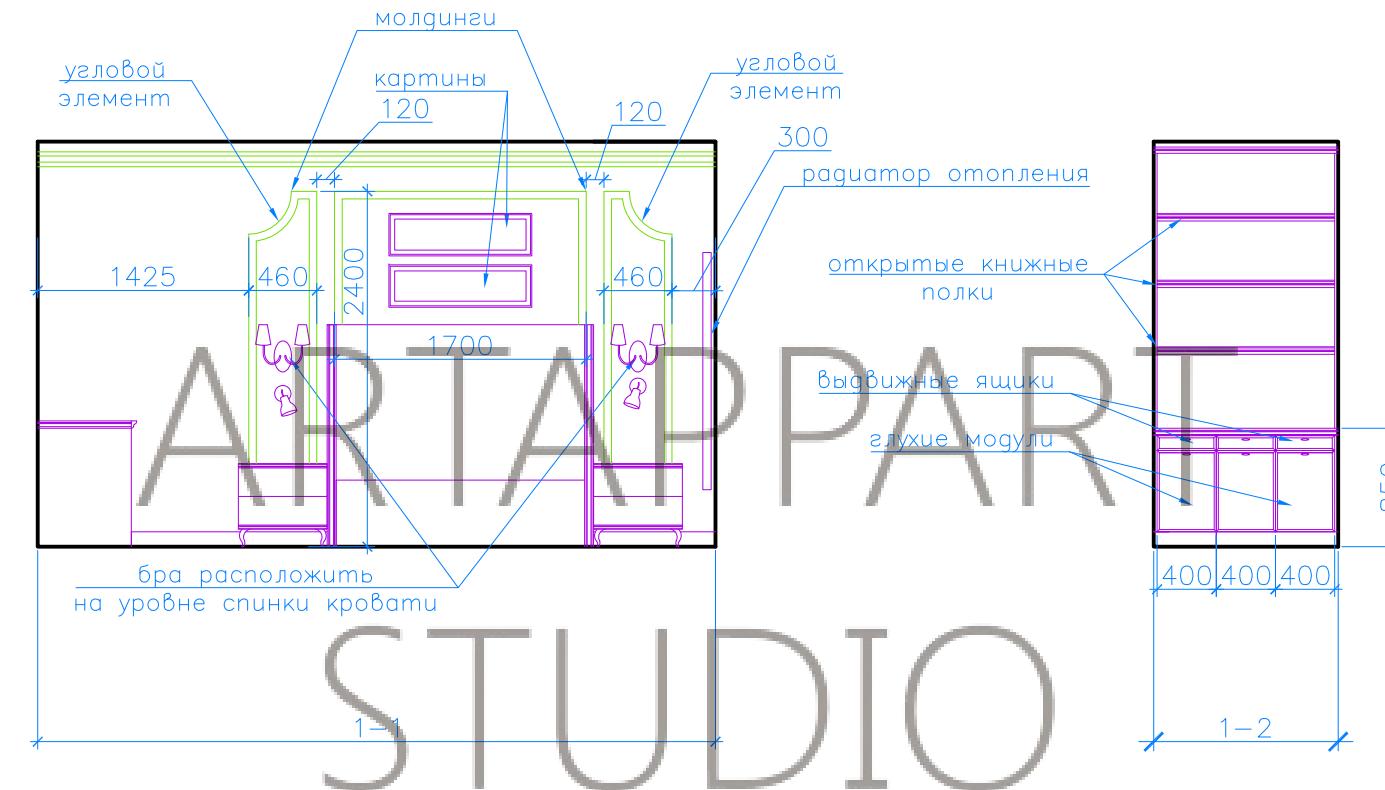

ARTAPPART STUDIO

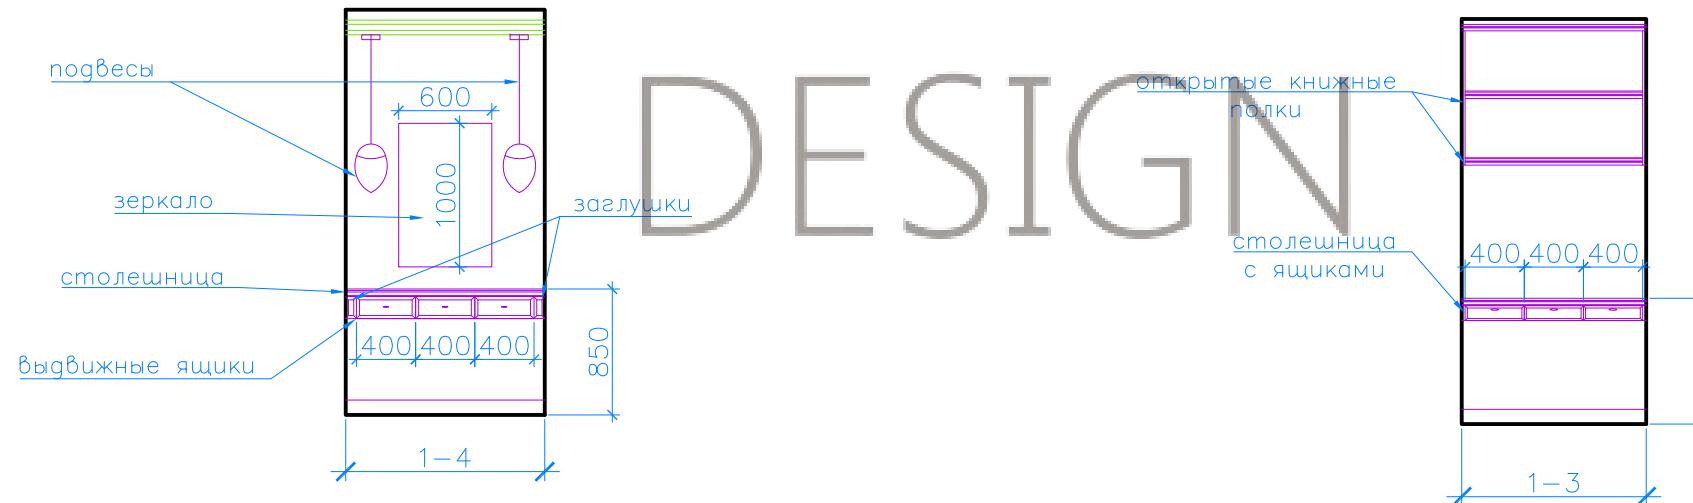

Согласовано
-------------



Инв. № подп.	Подп. и дата	Взам. инв.
--------------	--------------	------------

Изм.	Кол. уч.	Листм.	№ док.	Подп.	Дата	Разработка дизайн-проекта квартиры	Стадия	Листм.	Листов
Заказчик					2017		P		
Разработ.					2017				


Развертки по стенам  
М 1:50



ARTAPPART  
DESIGN  
STUDIO

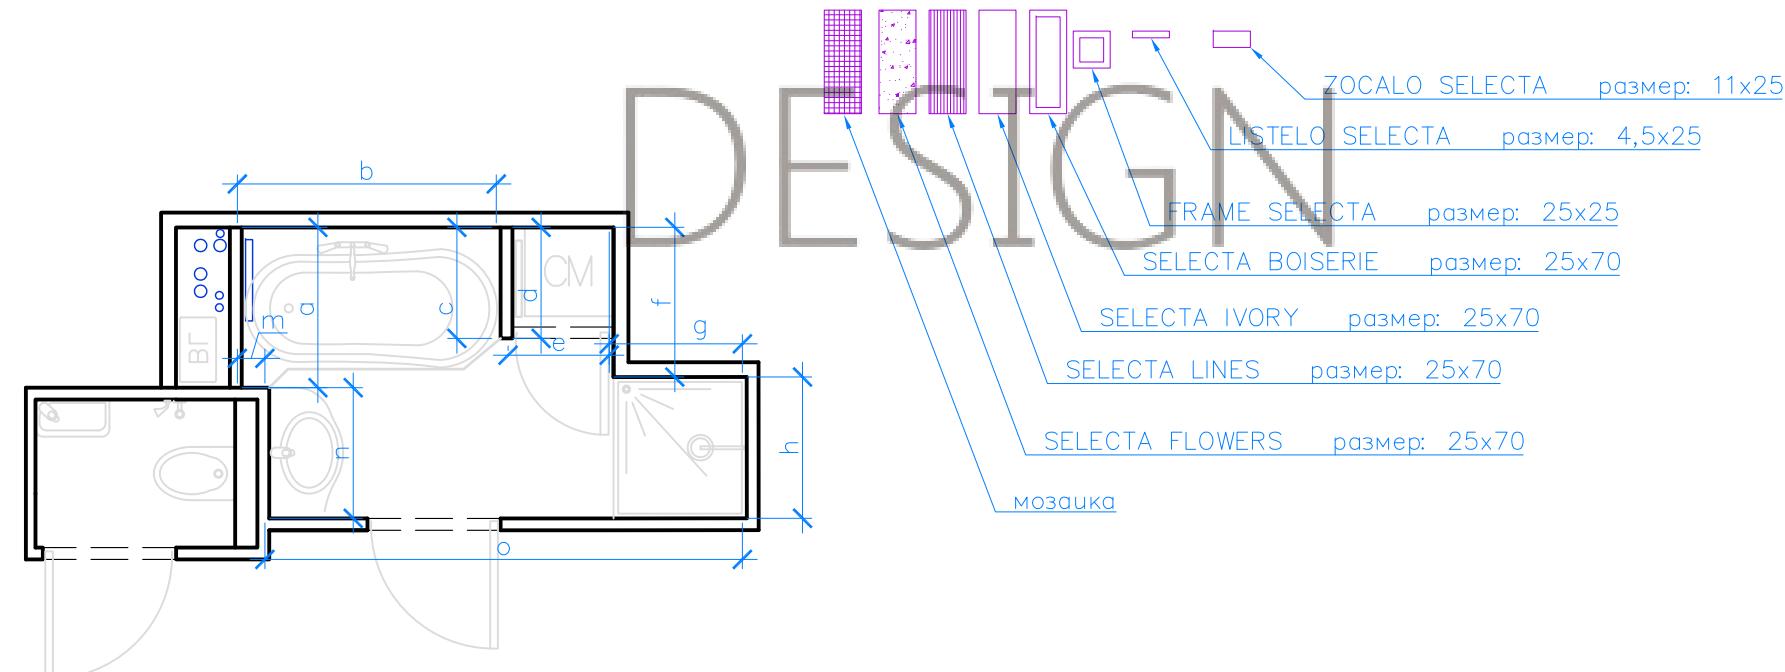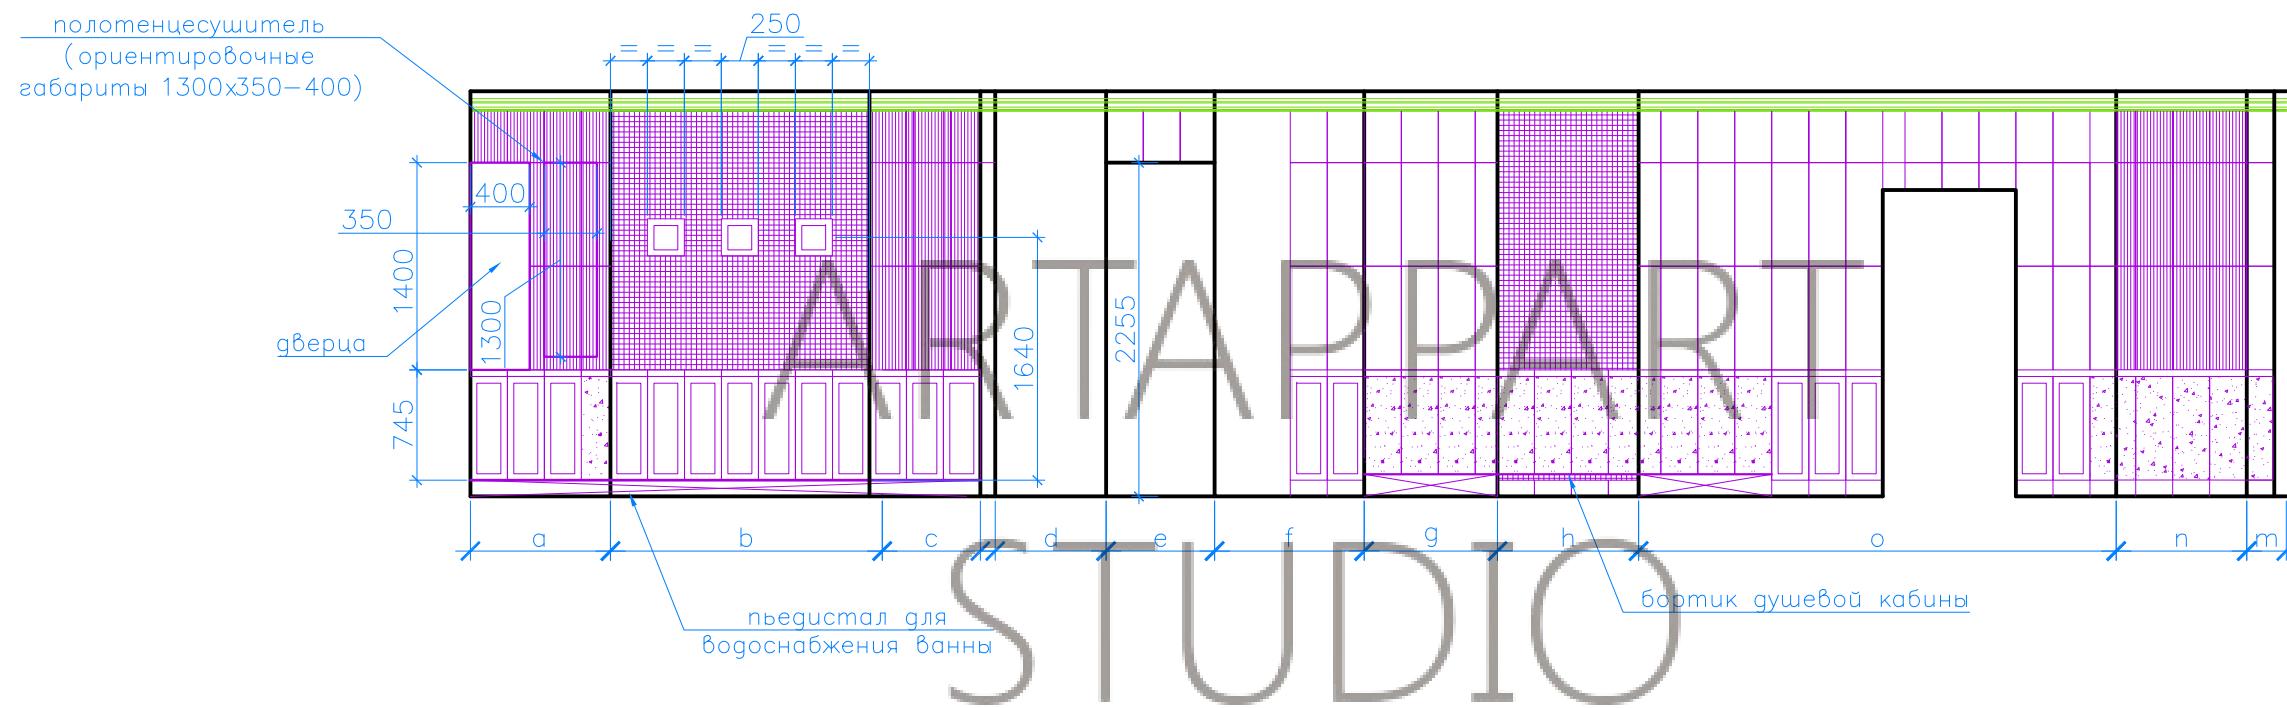

Изм.	Кол. уч.	Листм.	№ док.	Подп.	Дата	Разработка дизайн-проекта квартиры			Стадия	Листм.	Листов
Заказчик					2017				P		
Разработ.					2017						
Развертки по стенам М 1:50						ARTAPPART DESIGN STUDIO					

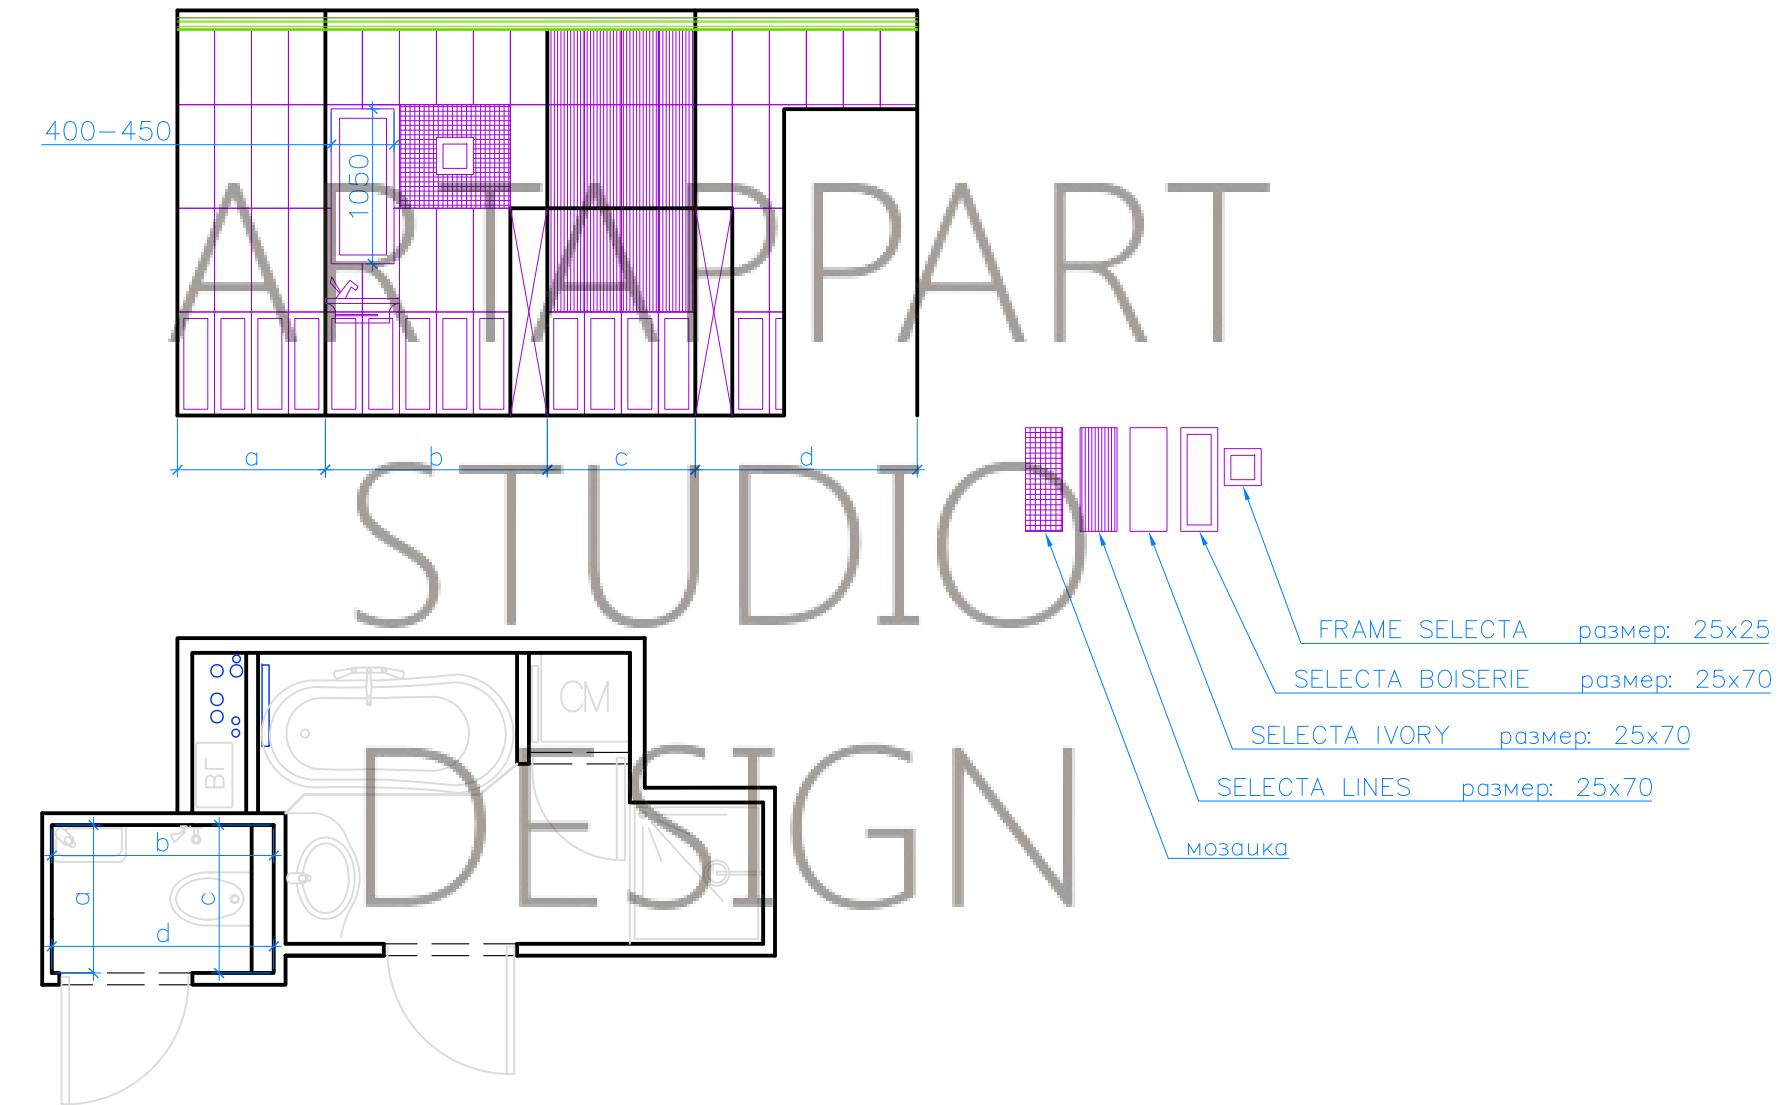

Инв. № подп.	Подп. и дата	Взам. инв.

Изм.	Кол. уч.	Листм	№ док.	Подп.	Дата	Разработка дизайн-проекта квартиры	Стадия	Листм	Листмов
Заказчик					2017		P		
Разработ.					2017				

Развертки по стенам  
М 1:50

ARTAPPART  
DESIGN  
STUDIO