




## Дизайн проект "Премиум"



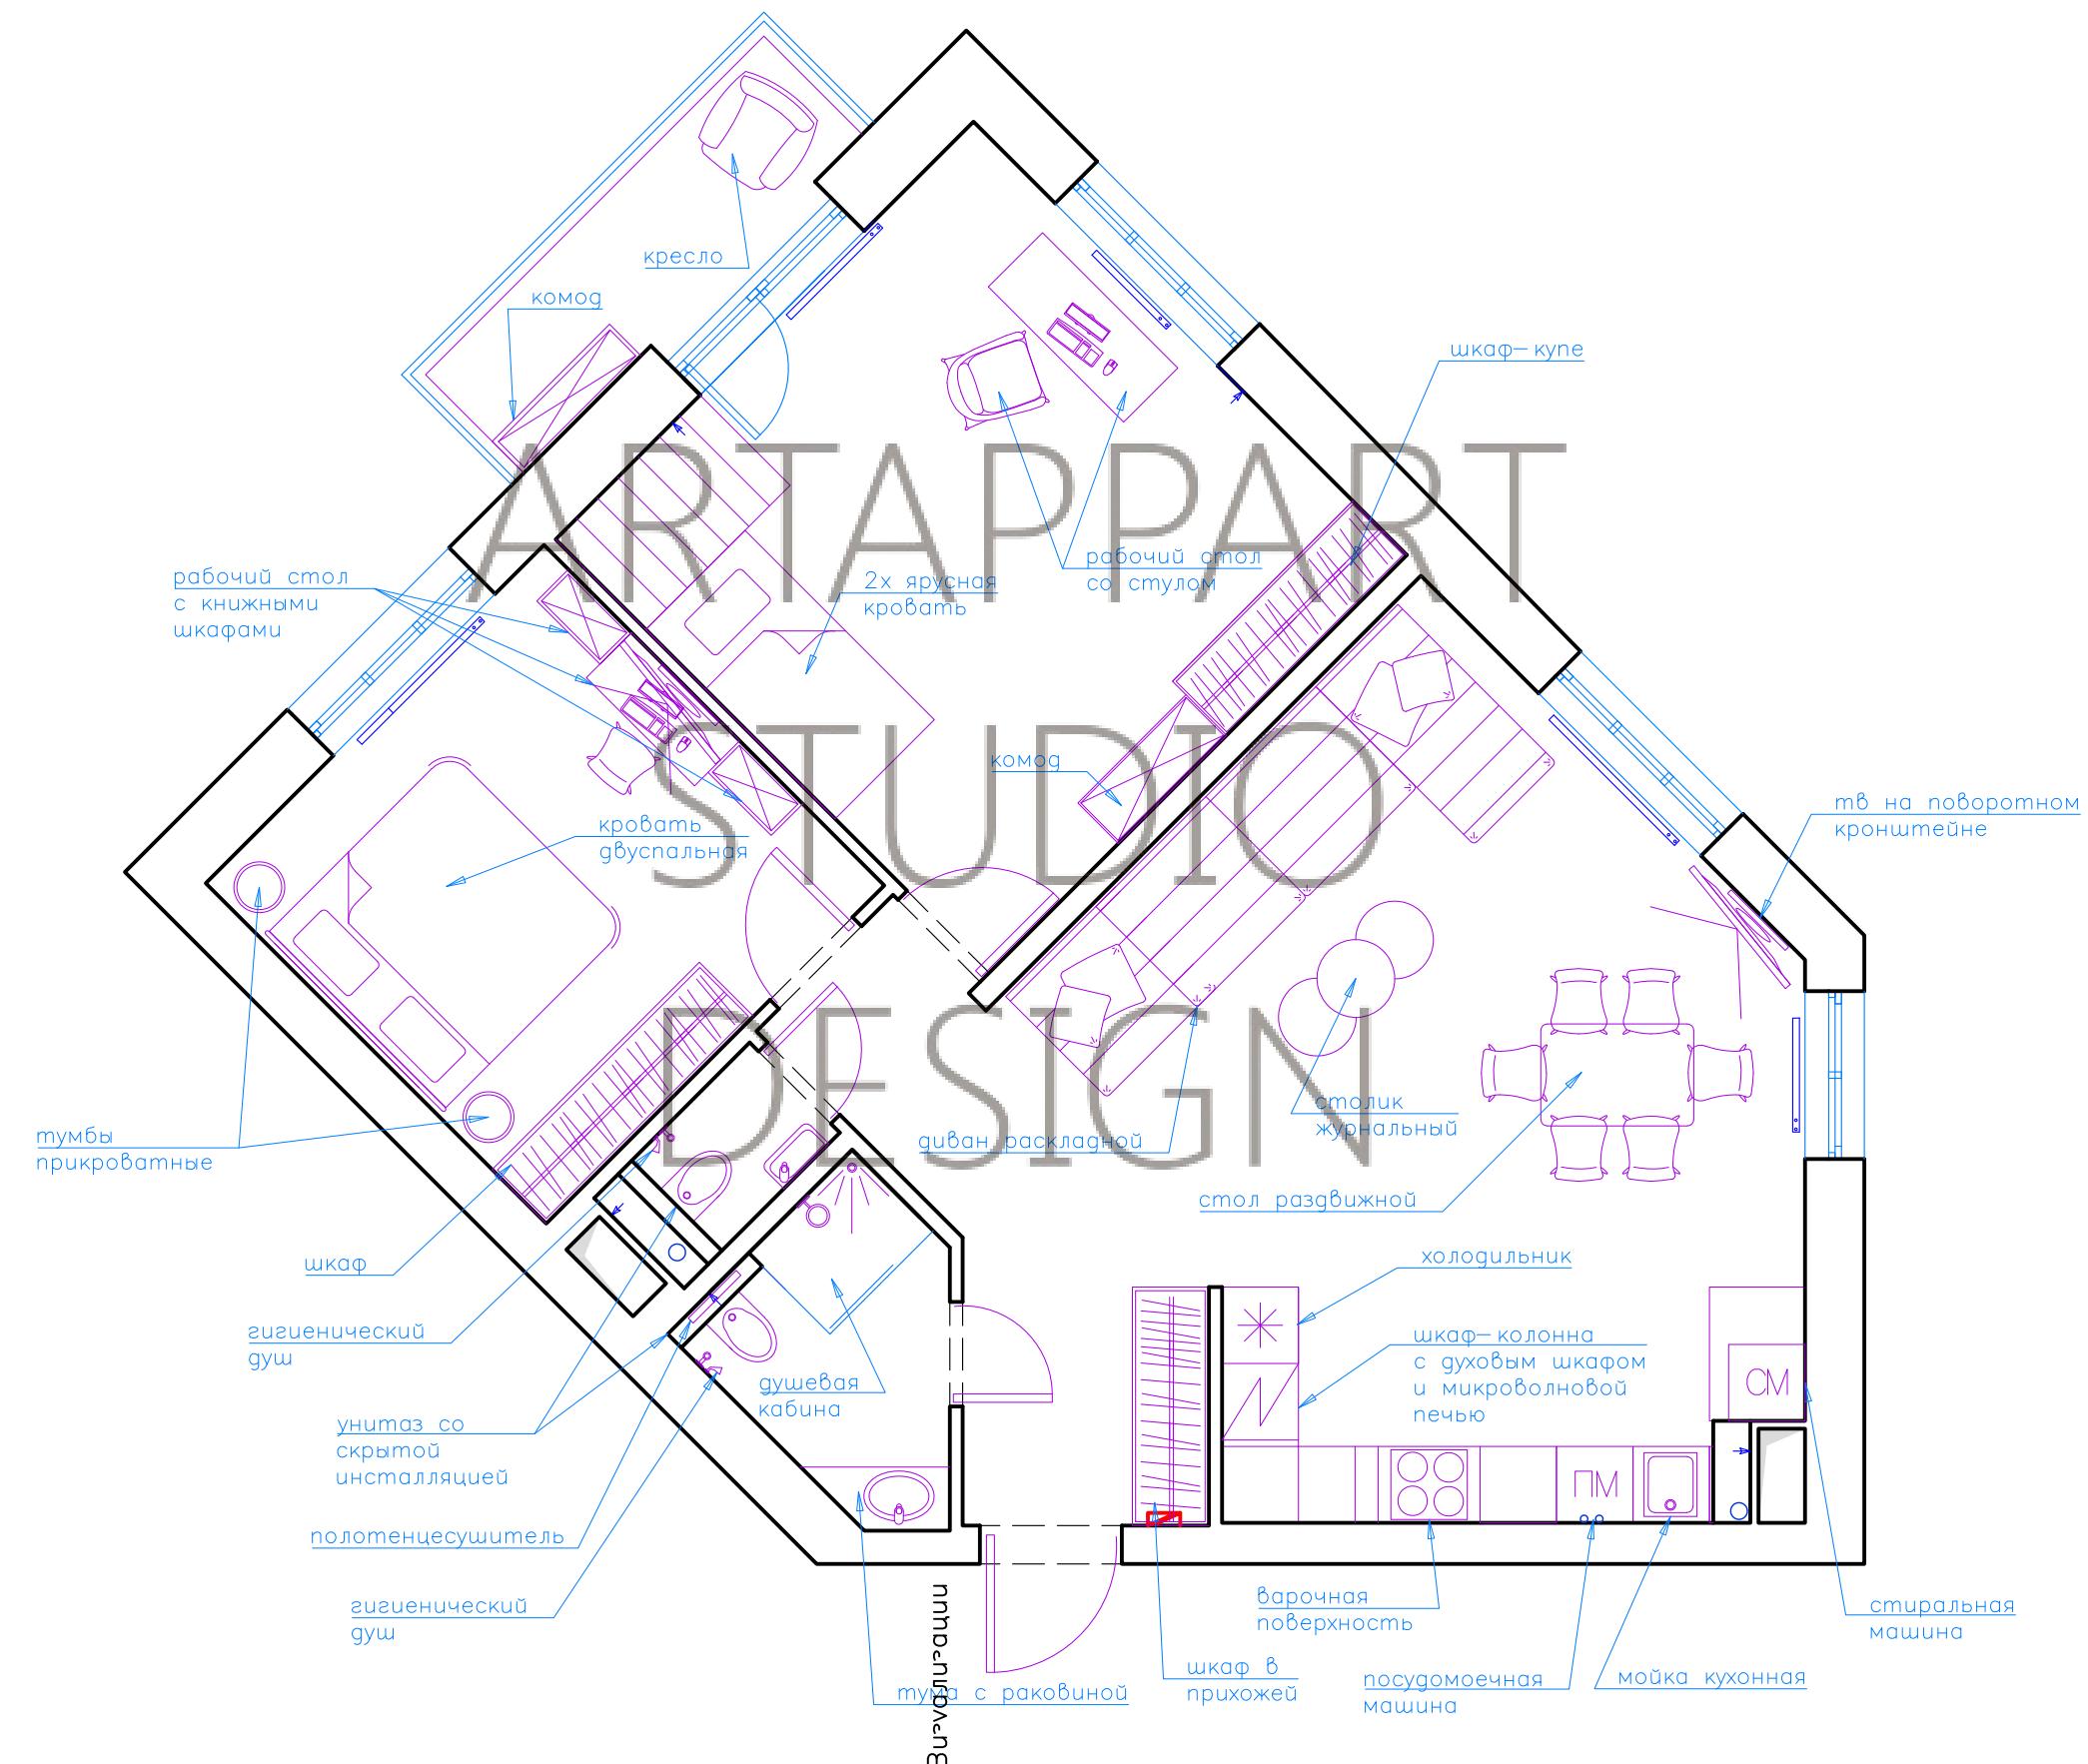

Лист	Листов	Масштаб
		M 1:60
Дизайнер		
Заказчик		План расстановки мебели и оборудования
		ARTAPPART DESIGN STUDIO

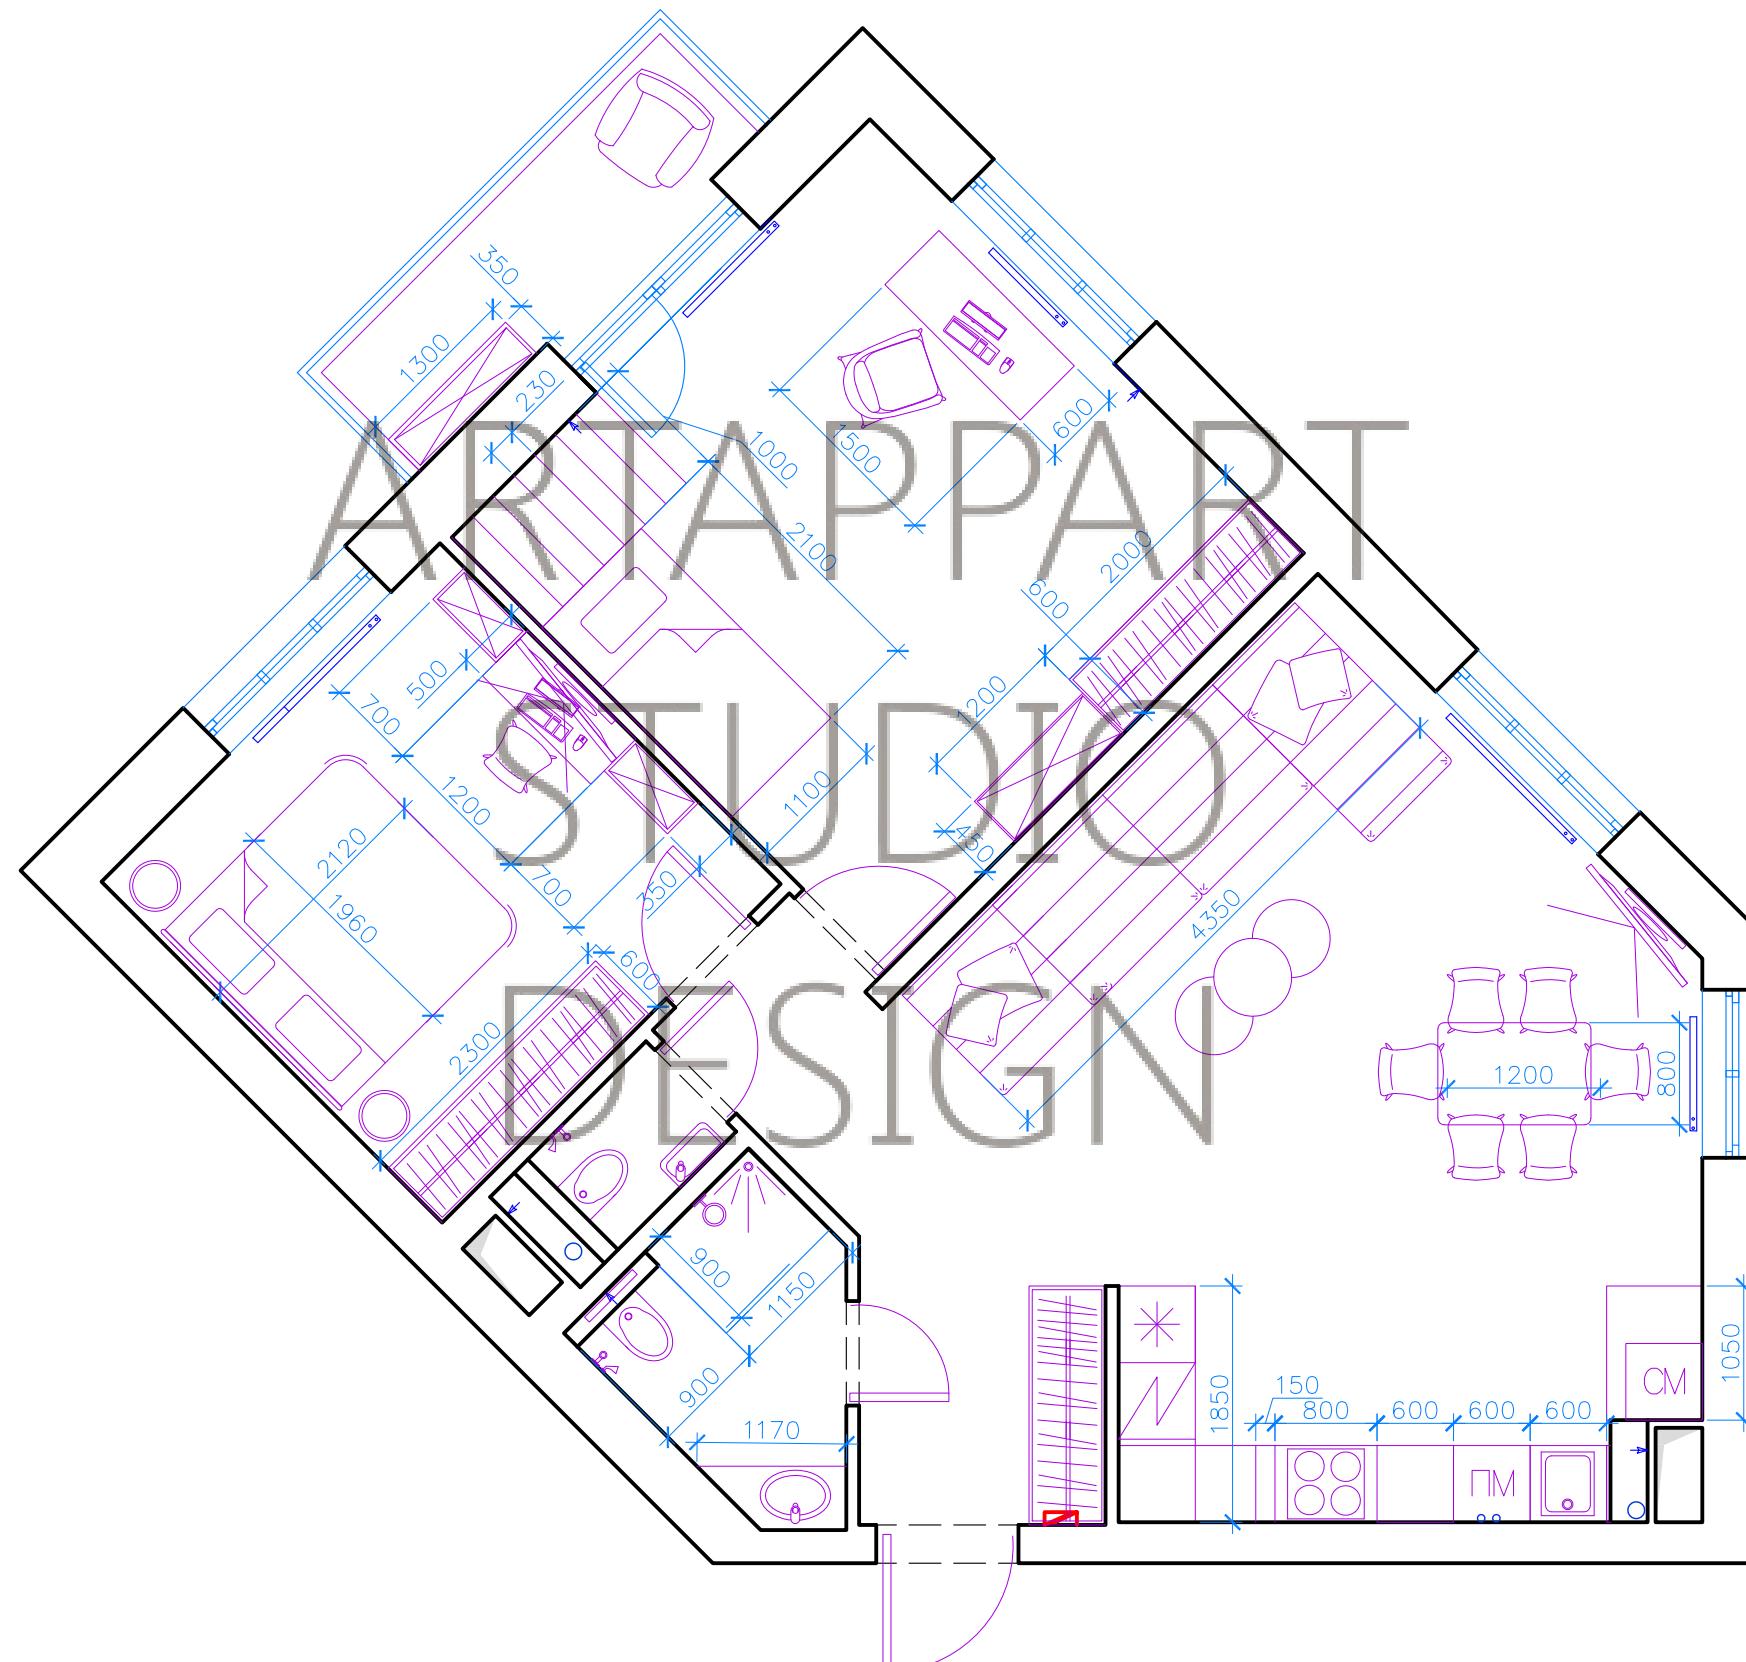

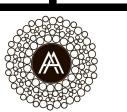Лист	Листов	Масштаб
		M 1:60
Дизайнер	Заказчик	Схема расположения с указанием габаритов
		 ARTAPPART DESIGN STUDIO



Акцентная стена  
Пано Rasch



Фоновые обои  
Eco wallpaper

# ARTAPPART

# STUDIO

Акцентная стена  
Пано Rasch

Ламинат  
Tarkett CRUISE

# DESIGN


Фоновые обои  
Eco wallpaper



Фоновые обои  
Eco wallpaper



Ламинат  
Ritter Organic

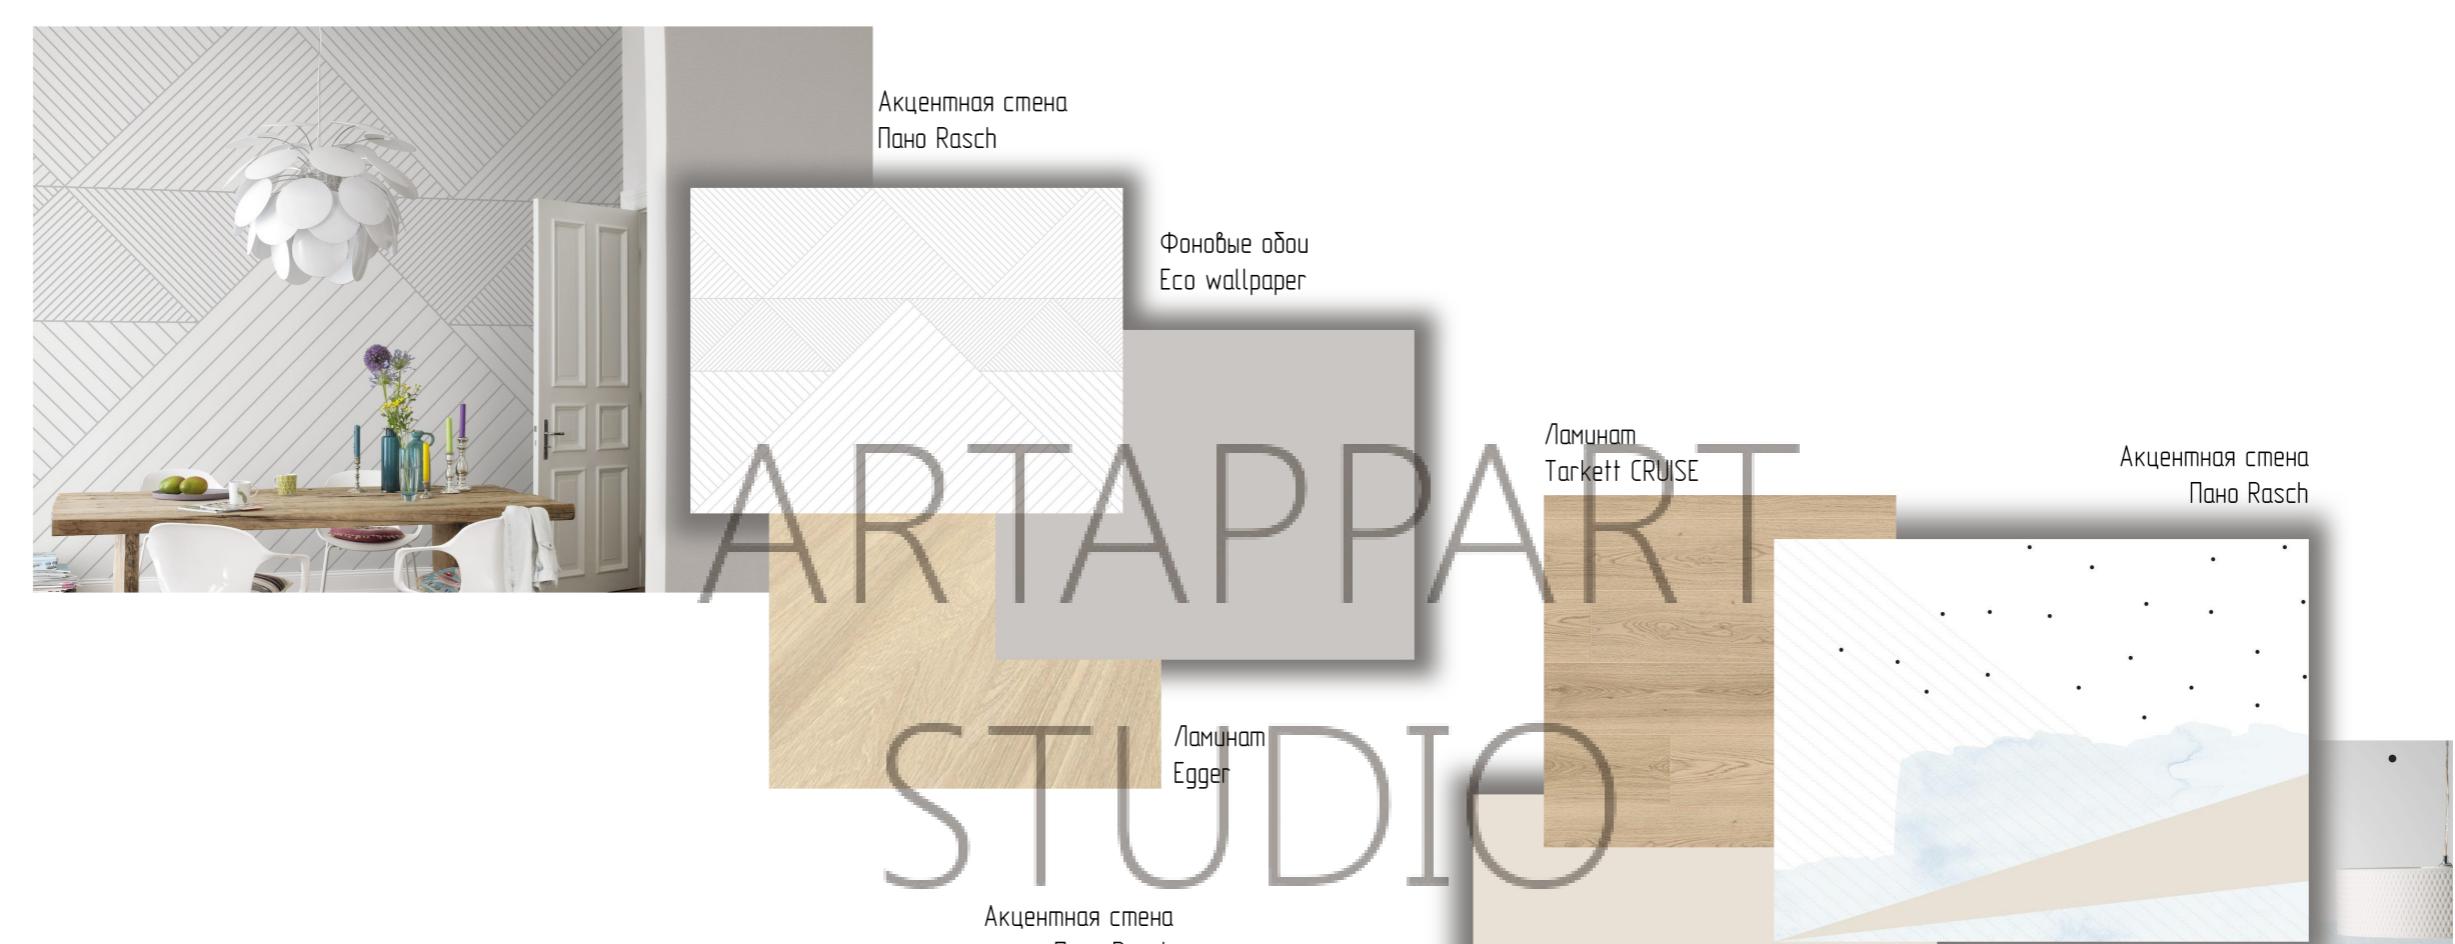

Акцентная стена  
Пано Rasch




Акцентная стена  
Пано Rasch

Лист	Листов	Масштаб
		M 1: 60
Дизайнер	Заказчик	



Обои  
Eco wallpaper

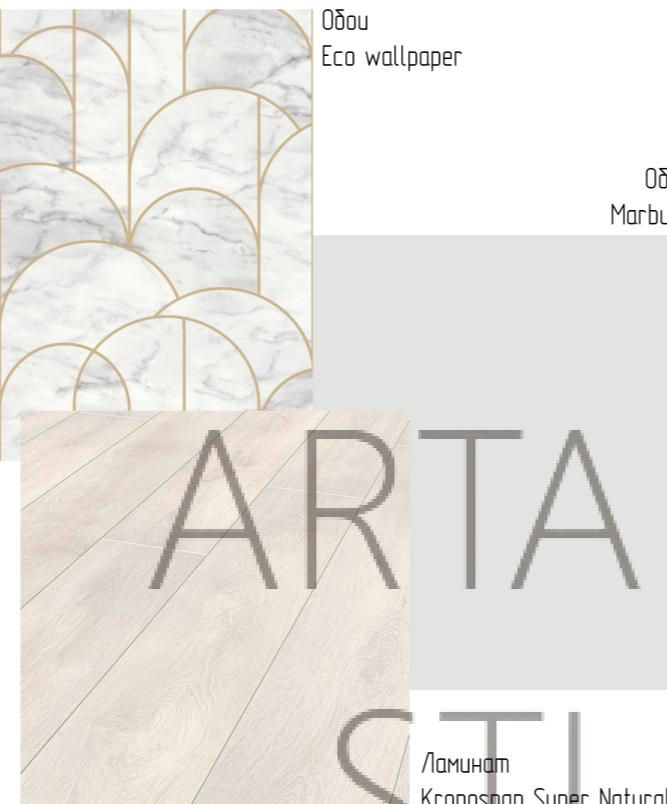

Обои  
Marburg

# ARTAPPART STUDIO

Ламинат  
Kronospan Super Natural



Обои  
Eco wallpaper



Ламинат  
Kronospan Super Natural

Обои  
Marburg




Обои  
Eco wallpaper



Ламинат  
Tarkett Woodstock

Ааі ғұа өттөе аәәе ішіліләәе ғұа аәү ішіліләәе, іа ғірінүйін өттөе тәаілілік  
ішіліләәе аїтөліліләәе.

Лист	Листов	Масштаб
		M 1: 60
Дизайнер		
Заказчик		

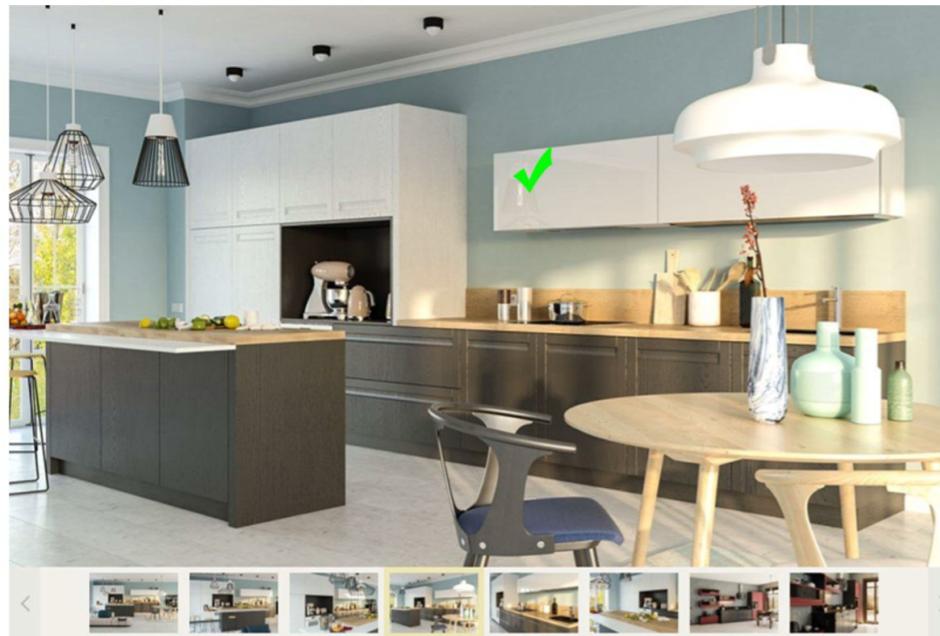


Кухонный гарнитур из массива. Очень интересная модель, слева показаны оттенки в которые колеруется дерево, галочками пометила то что предлагаю.  
Выше показаны оттенки стекла, которое можно вставить в деревянные фасады. Либо сделать как например, подвесные ящики с фасадами из пластика



Предлагаю вот эту модель дивана, она будет по ширине 4500, помещается в Вашу гостиную. У этого производителя есть кожезаменитель, то есть это будет не натуральная кожа. Цвет можно подобрать близко к тому что на картинке.



Вариант обеденного стола

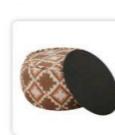

Вариант обеденного стола



Элегантный вариант журнального столика

В качестве журнальных столиков предлагаю поставить два вот таких пуфа-столика, они очень интересно будут смотреться в интерьере.



120 см



Вариант обеденного стола



Вариант обеденного стола



Паркет, который я предлагаю в подборку

[Eurostandard Дуб классик](#)

[Eurostandard Дуб Кофейный](#)

[Eurostandard Ясень кремовый](#)



847 руб/м<sup>2</sup>  
Kerama Marazzi Карнаби-  
стрит Орнамент 1577T N  
Декор 20x20 см  
Код товара: 452434



886 руб/м<sup>2</sup>  
Kerama Marazzi Карнаби-  
стрит 1576T N Серый  
Орнамент  
Декор 20x20 см  
Код товара: 452598




847 руб/м<sup>2</sup>  
Kerama Marazzi Коллиано  
SG914600N Орнамент  
Декор 30x30 см  
Артикул: SG914600N  
Код товара: 303051

✓ В НАЛИЧИИ Доставка  
29 Июн, 01-02 Июл



847 руб/м<sup>2</sup>  
Kerama Marazzi Коллиано  
SG914500N Орнамент  
(гранит)  
Декор 30x30 см  
Код товара: 303052

✓ В НАЛИЧИИ Доставка  
29 Июн, 01-02 Июл

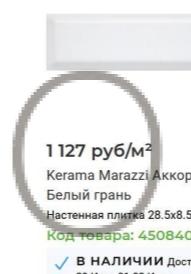

1127 руб/м<sup>2</sup>  
Kerama Marazzi Аккорд  
Белый грань  
Настенная плитка 28.5x8.5 см  
Код товара: 450840

✓ В НАЛИЧИИ Доставка  
29 Июн, 01-02 Июл



1 222 руб/м<sup>2</sup>  
Kerama Marazzi Аккорд  
Зеленый темный грань  
Настенная плитка 28.5x8.5 см  
Код товара: 450843

✓ В НАЛИЧИИ Доставка  
29 Июн, 01-02 Июл



1 222 руб/м<sup>2</sup>  
Kerama Marazzi Аккорд  
Серый грань  
Настенная плитка 28.5x8.5 см  
Код товара: 450844

✓ В НАЛИЧИИ Доставка  
29 Июн, 01-02 Июл




1 222 руб/м<sup>2</sup>  
Kerama Marazzi Аккорд  
Зеленый грань  
Настенная плитка 28.5x8.5 см  
Код товара: 450845

✓ В НАЛИЧИИ Доставка  
29 Июн, 01-02 Июл



1 222 руб/м<sup>2</sup>  
Kerama Marazzi Аккорд  
Темно-серый грань  
Настенная плитка 28.5x8.5 см  
Код товара: 450842

✓ В НАЛИЧИИ Доставка  
29 Июн, 01-02 Июл

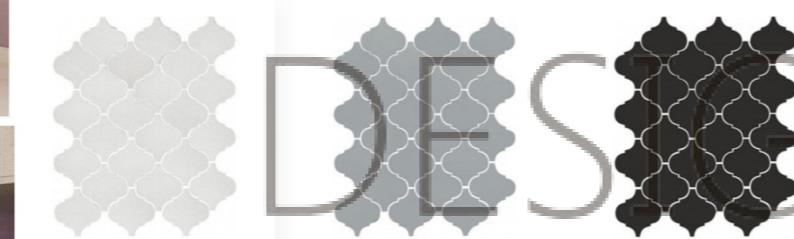

2 790 руб/м<sup>2</sup>  
Kerama Marazzi Арабески  
65000 Глянцевый Белый  
Настенная плитка 26x30 см  
Артикул: 65000  
Код товара: 543120



3 009 руб/м<sup>2</sup>  
Kerama Marazzi Арабески  
65012 Глянцевый Серый  
Настенная плитка 26x30 см  
Артикул: 65012  
Код товара: 543121



3 212 руб/м<sup>2</sup>  
Kerama Marazzi Арабески  
65001 Глянцевый Черный  
Настенная плитка 26x30 см  
Артикул: 65001  
Код товара: 543124








ARTAPART  
STUDIO  
DESIGN





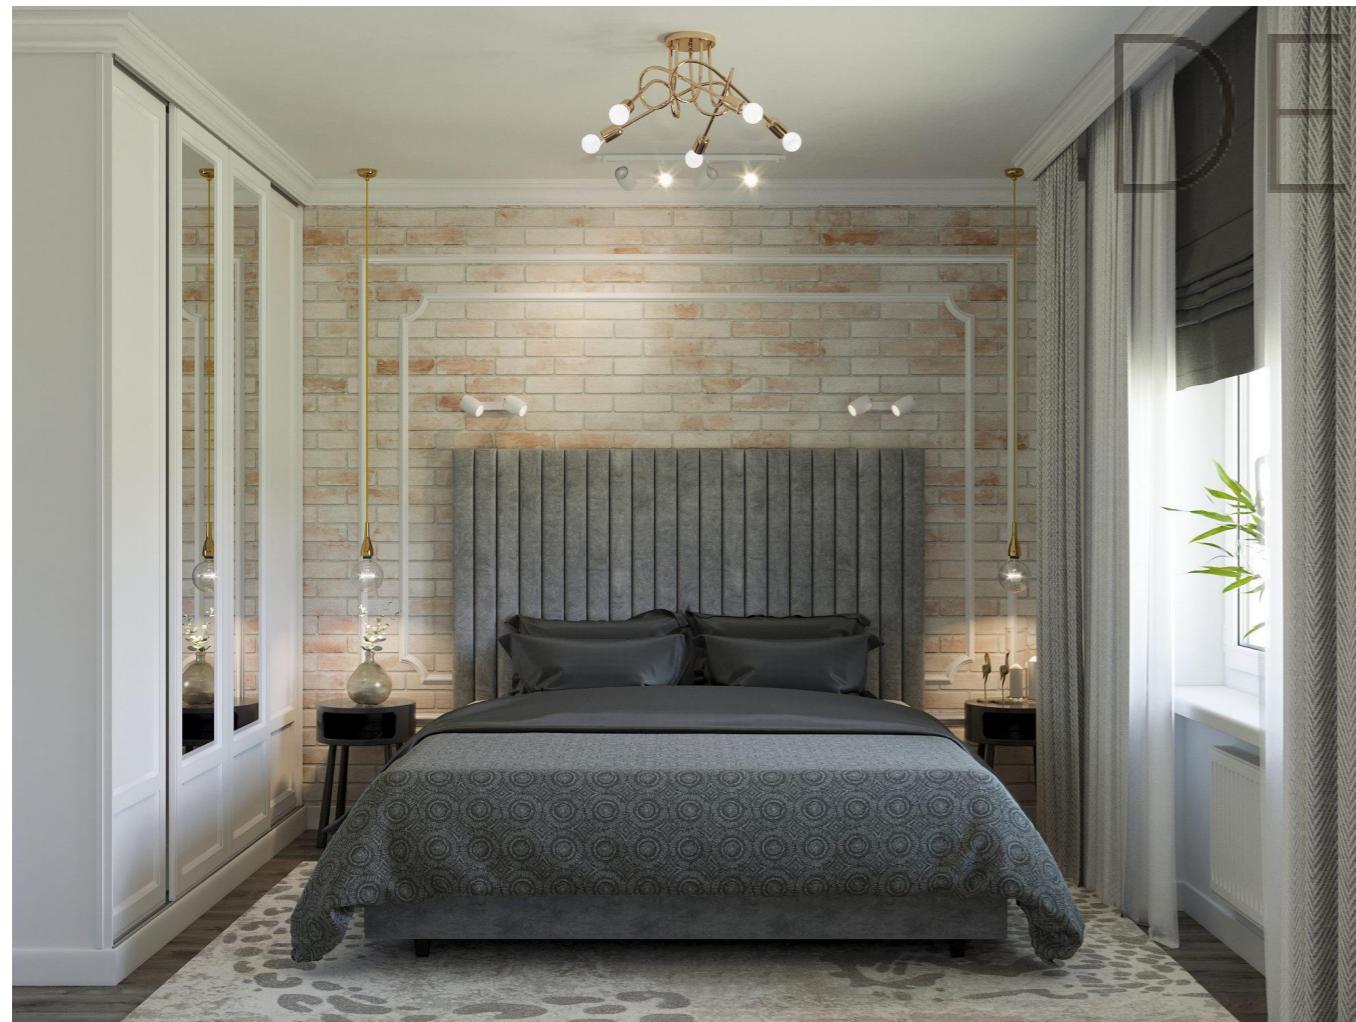




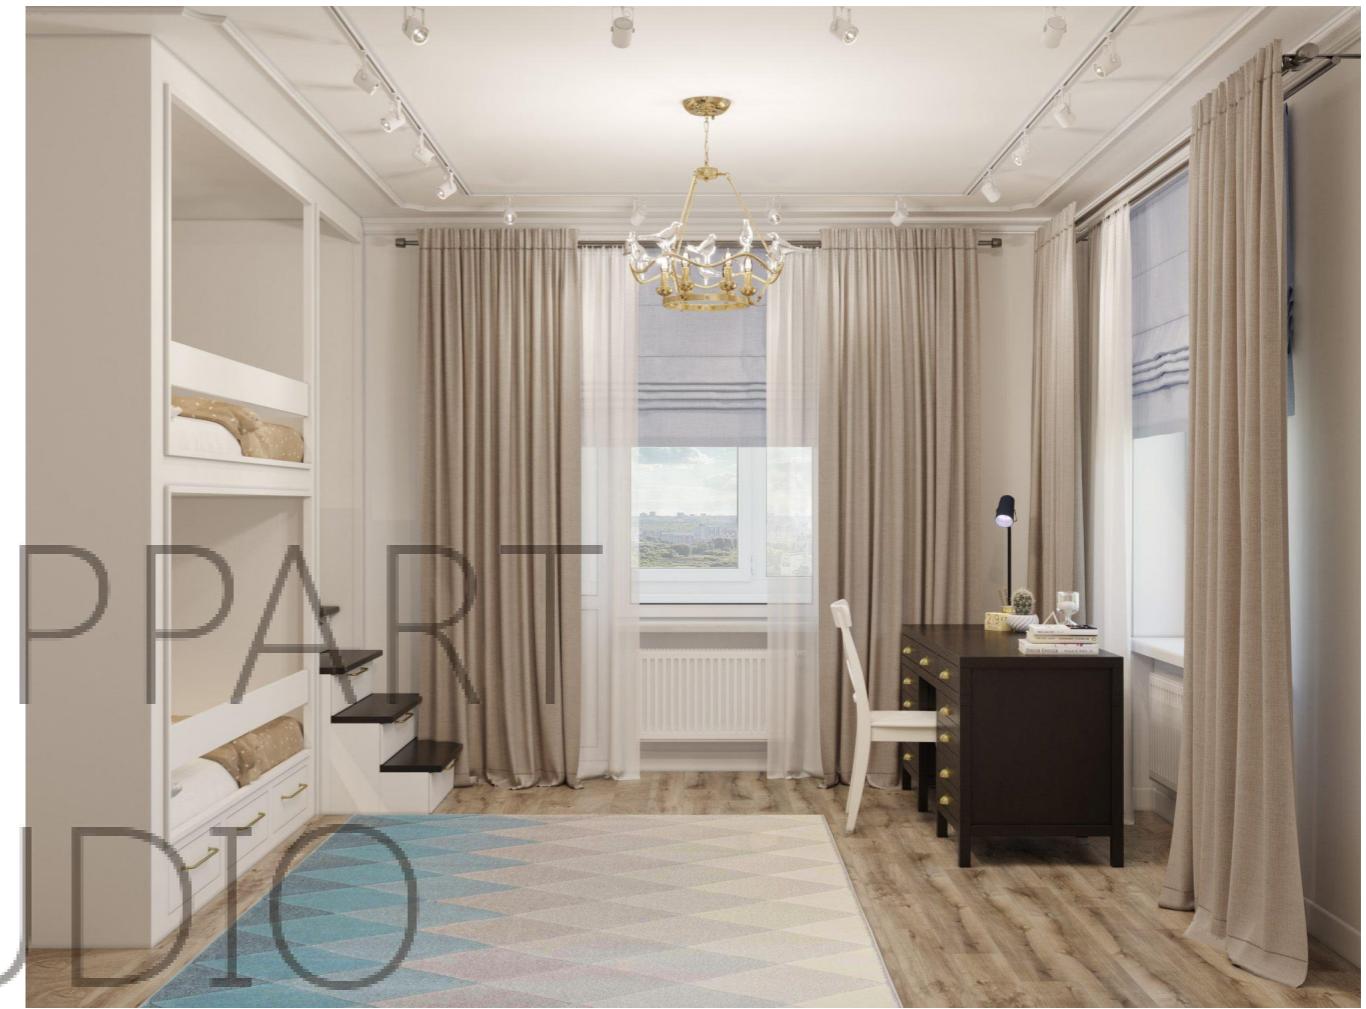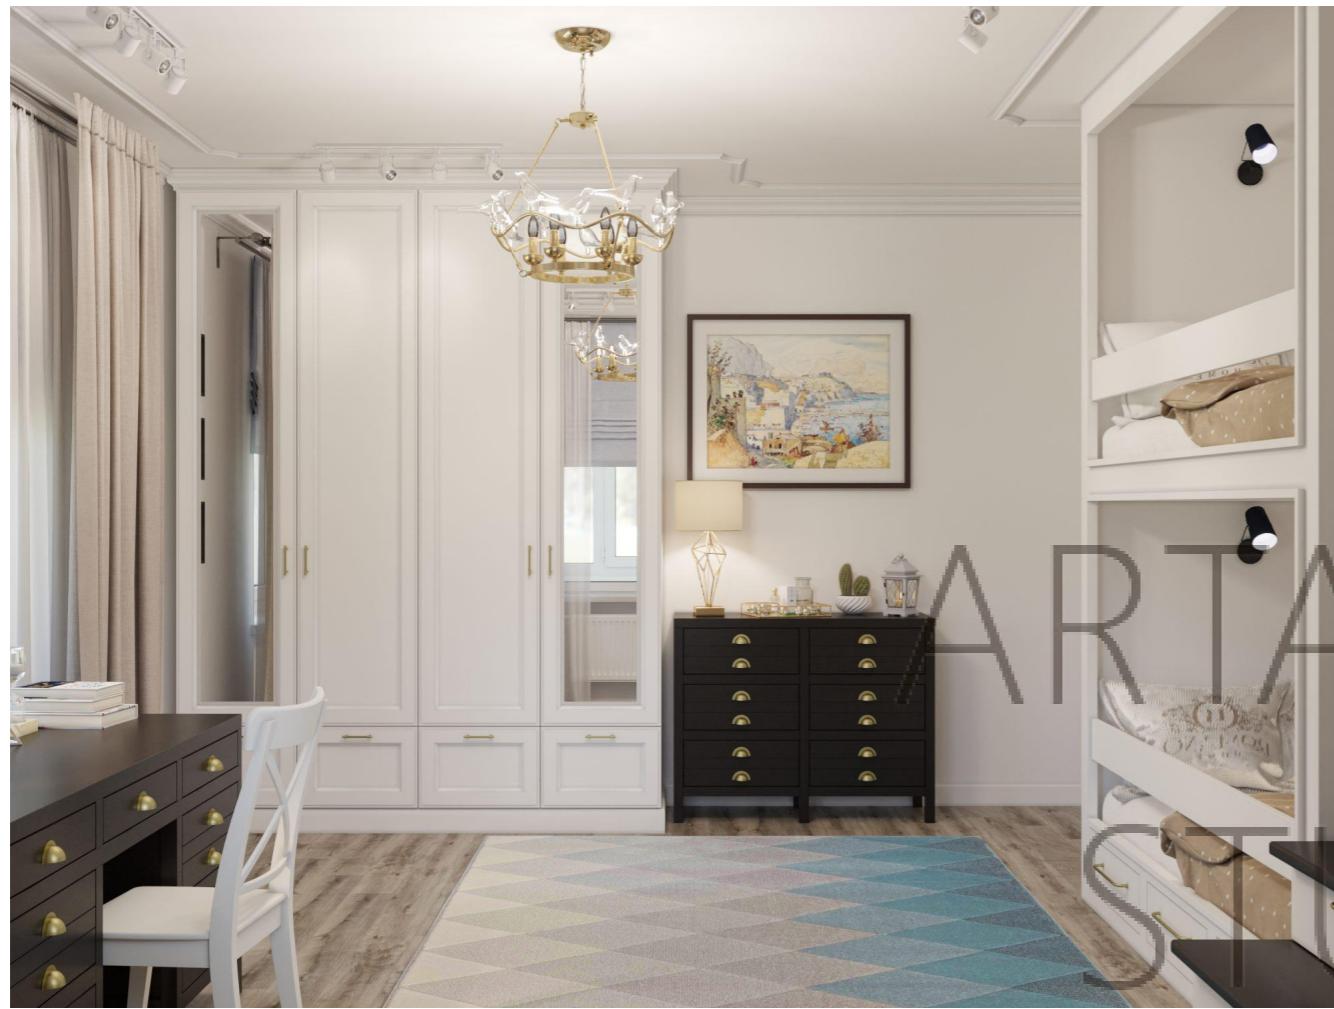

ARTAPART  
STUDIO  
DESIGN




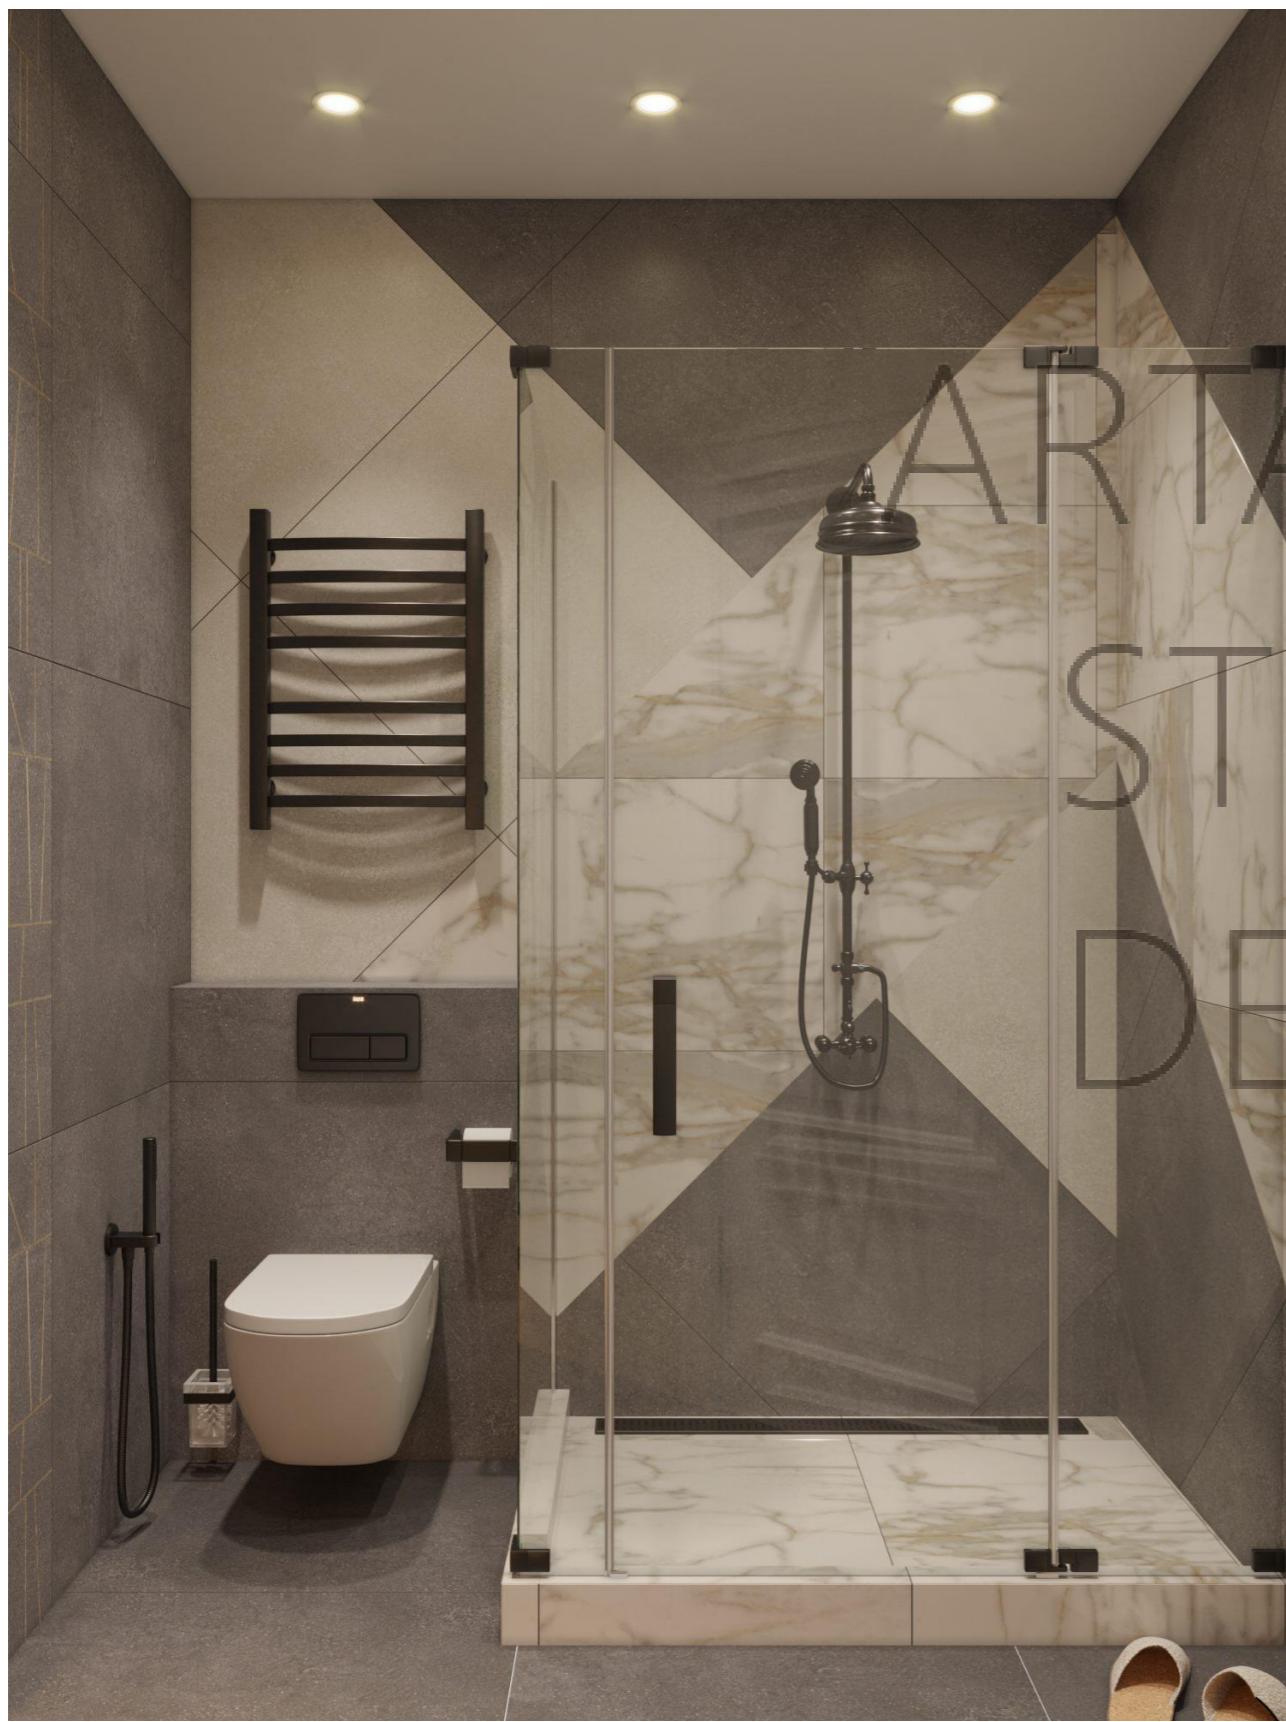

ARTAPPART  
STUDIO  
DESIGN






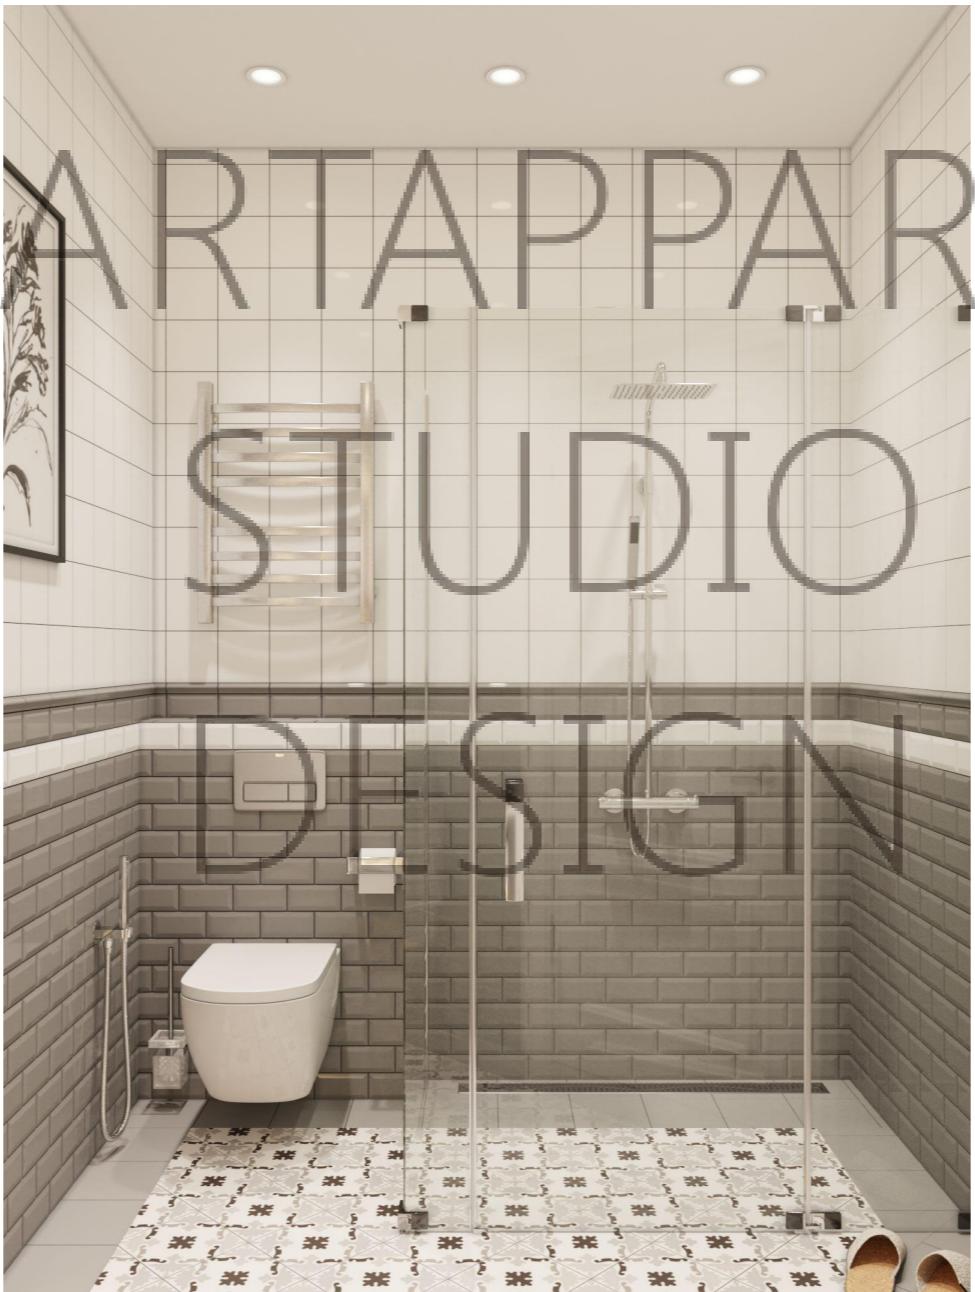



ART APPART  
STUDIO  
DESIGN

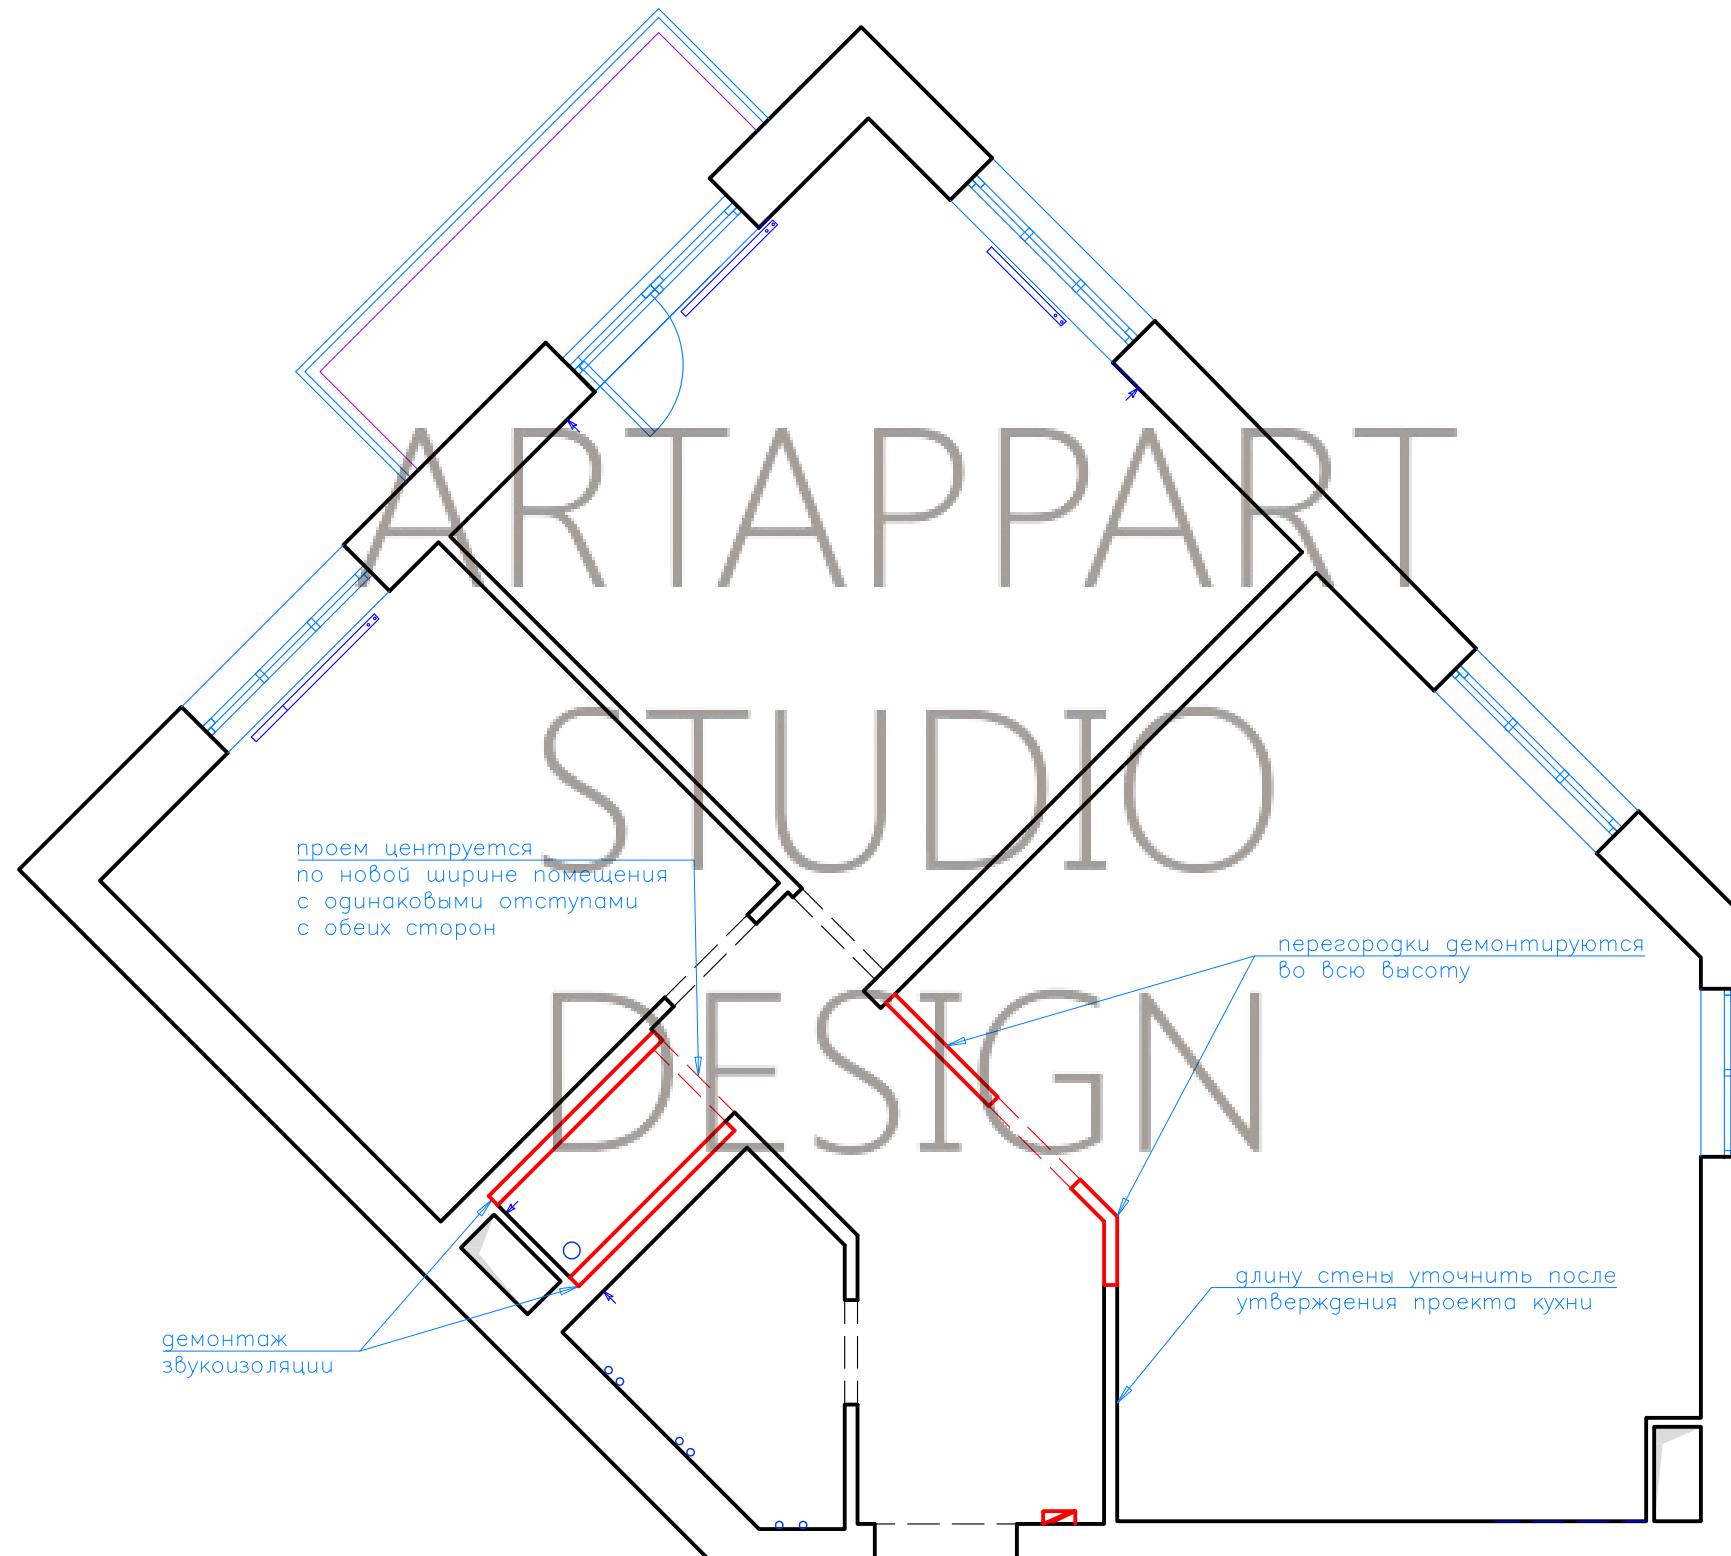


Условные обозначения:  
— — демонтируемые  
 перегородки

				Лист	Листов	Масштаб
						M 1: 60
Дизайнер				План демонтажа		
Заказчик						



ARTAPPART  
 DESIGN  
 STUDIO

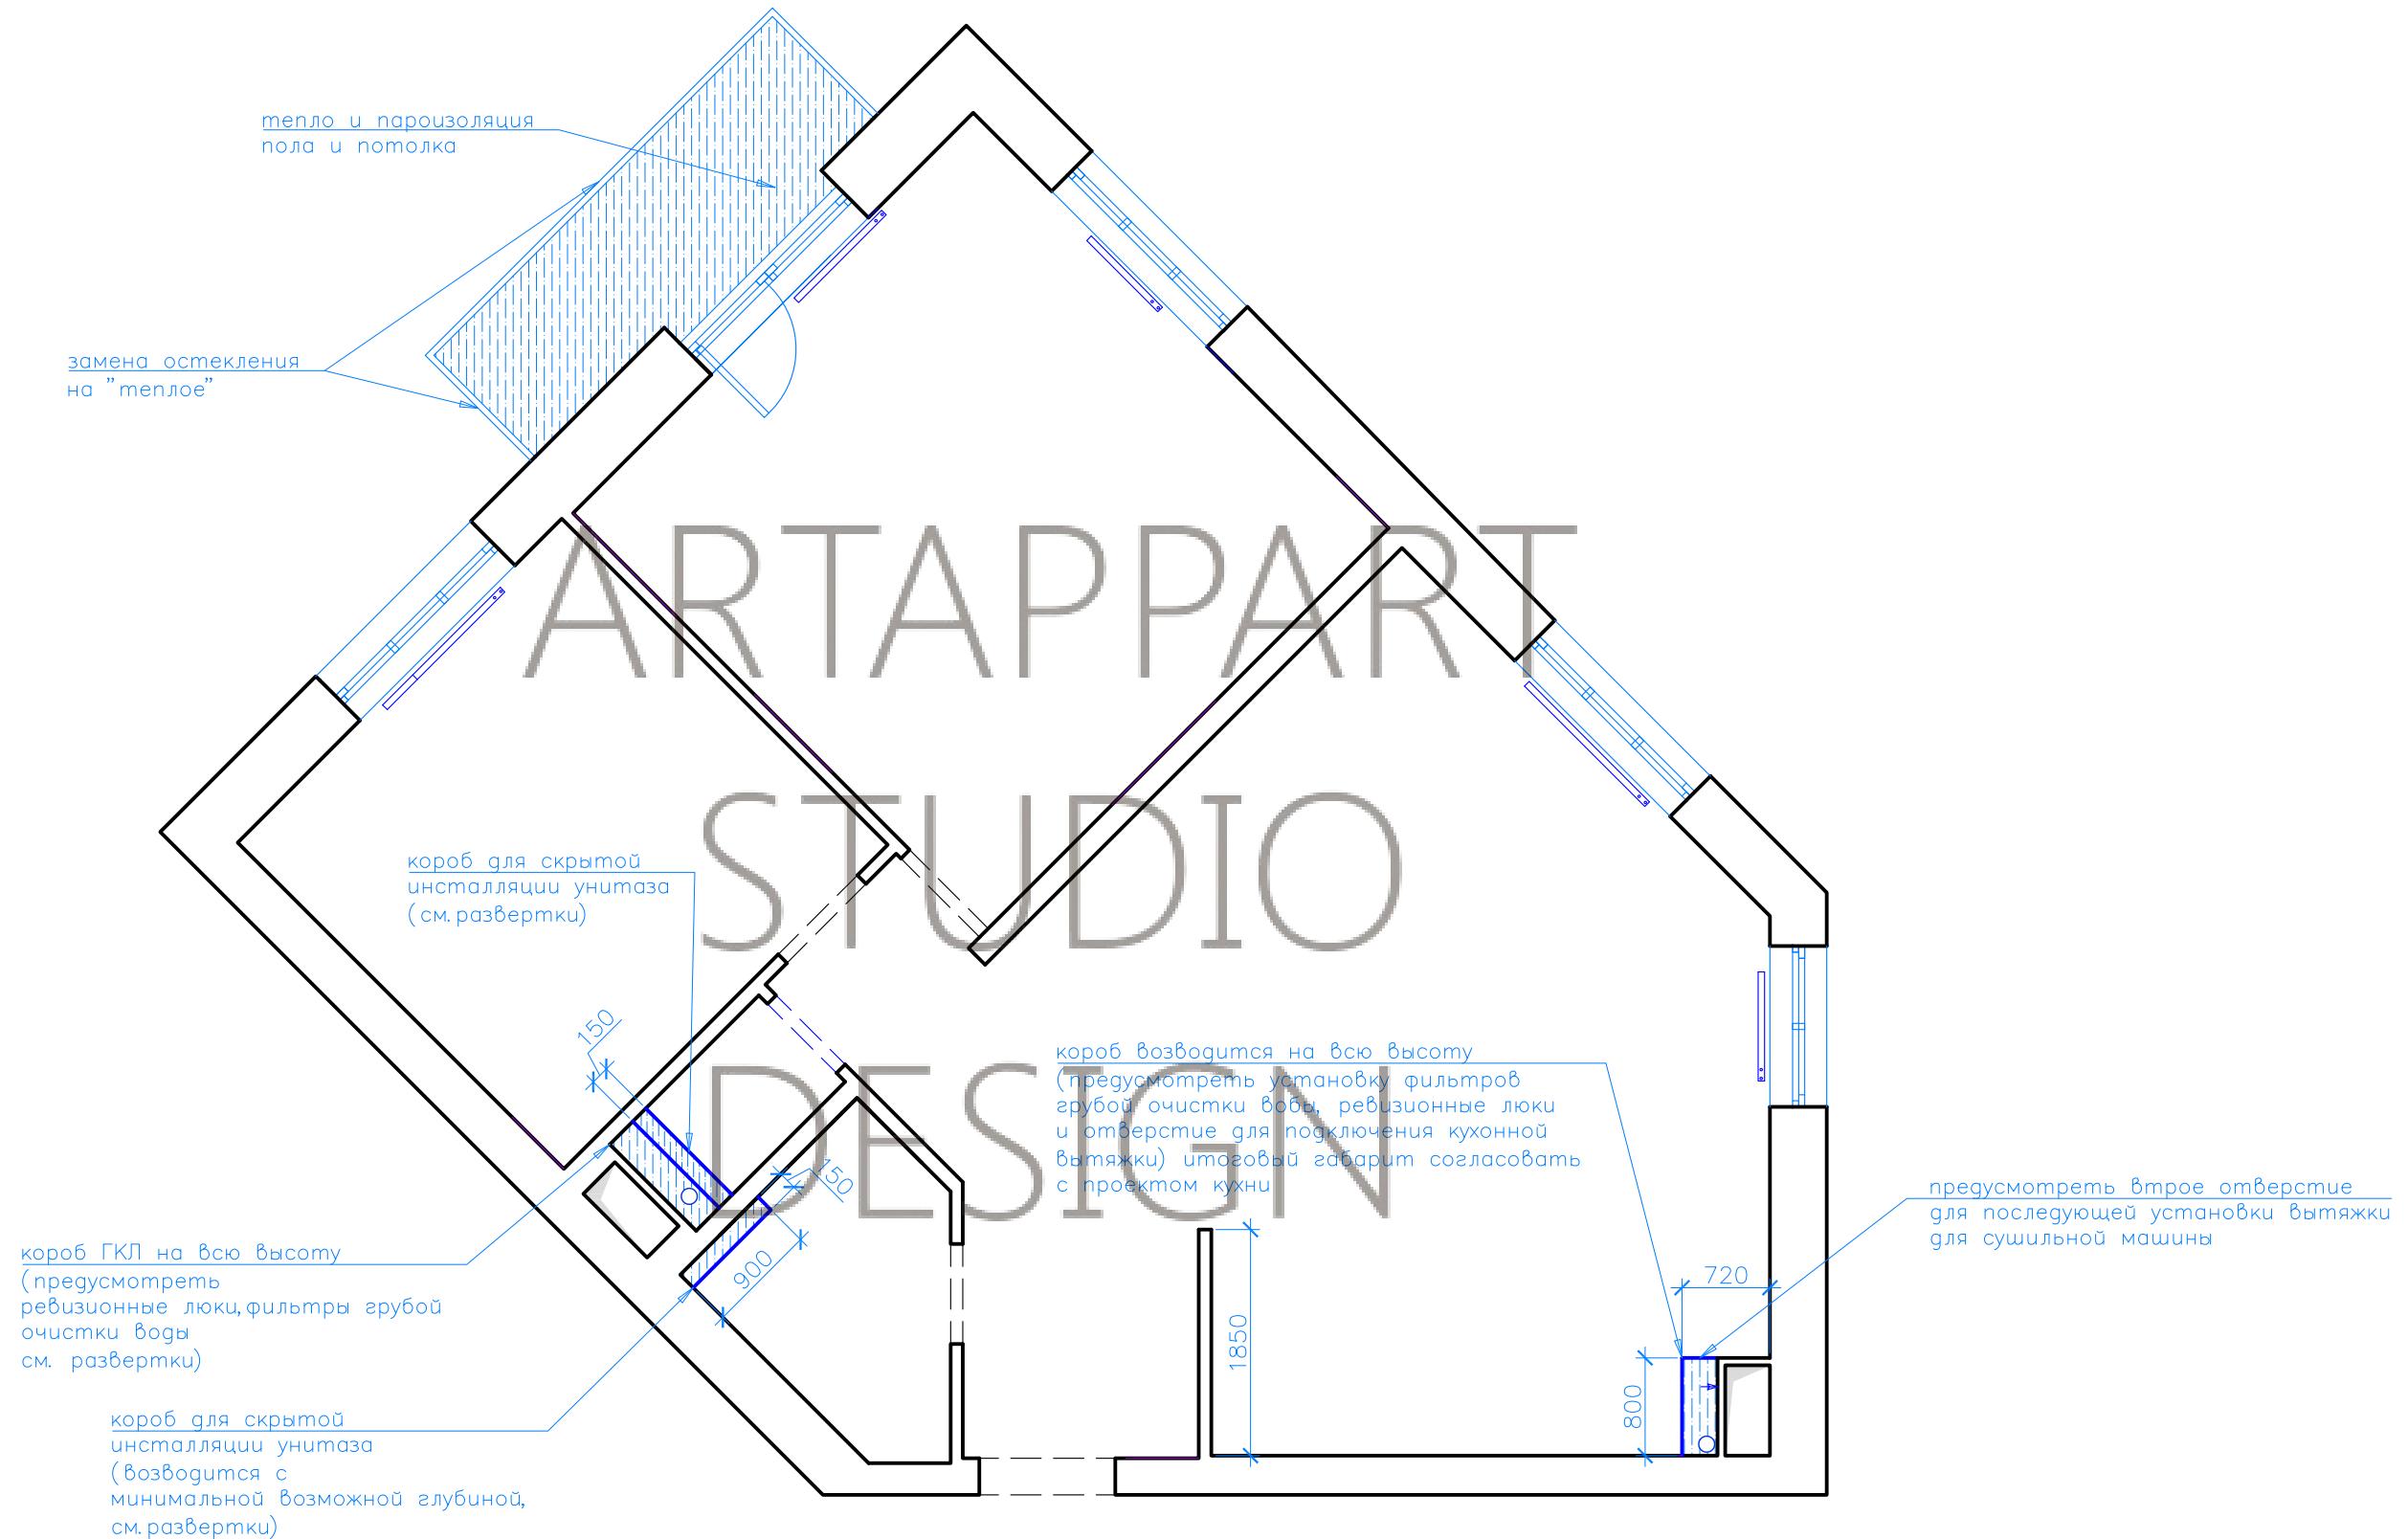


Условные обозначения:

– возводимые перегородки

Примечание:

1. Все возводимые перегородки выполнить из ГКЛ, толщина 100 мм, если не указано иное.
2. Во влажных помещениях использовать влагостойкий гипрок.
3. Высота проемов в возводимых перегородках = 2070 от УЧП (предварительно проконсультироваться, нет ли необходимости в проемах не стандартной высоты. Высота 2070 мм приведена в соответствии со стандартами большинства отечественных производителей дверей)


Лист	Листов	Масштаб
		M 1:60
Дизайнер		План возводимых
Заказчик		перегородок и конструкций
		ARTAPPART DESIGN STUDIO

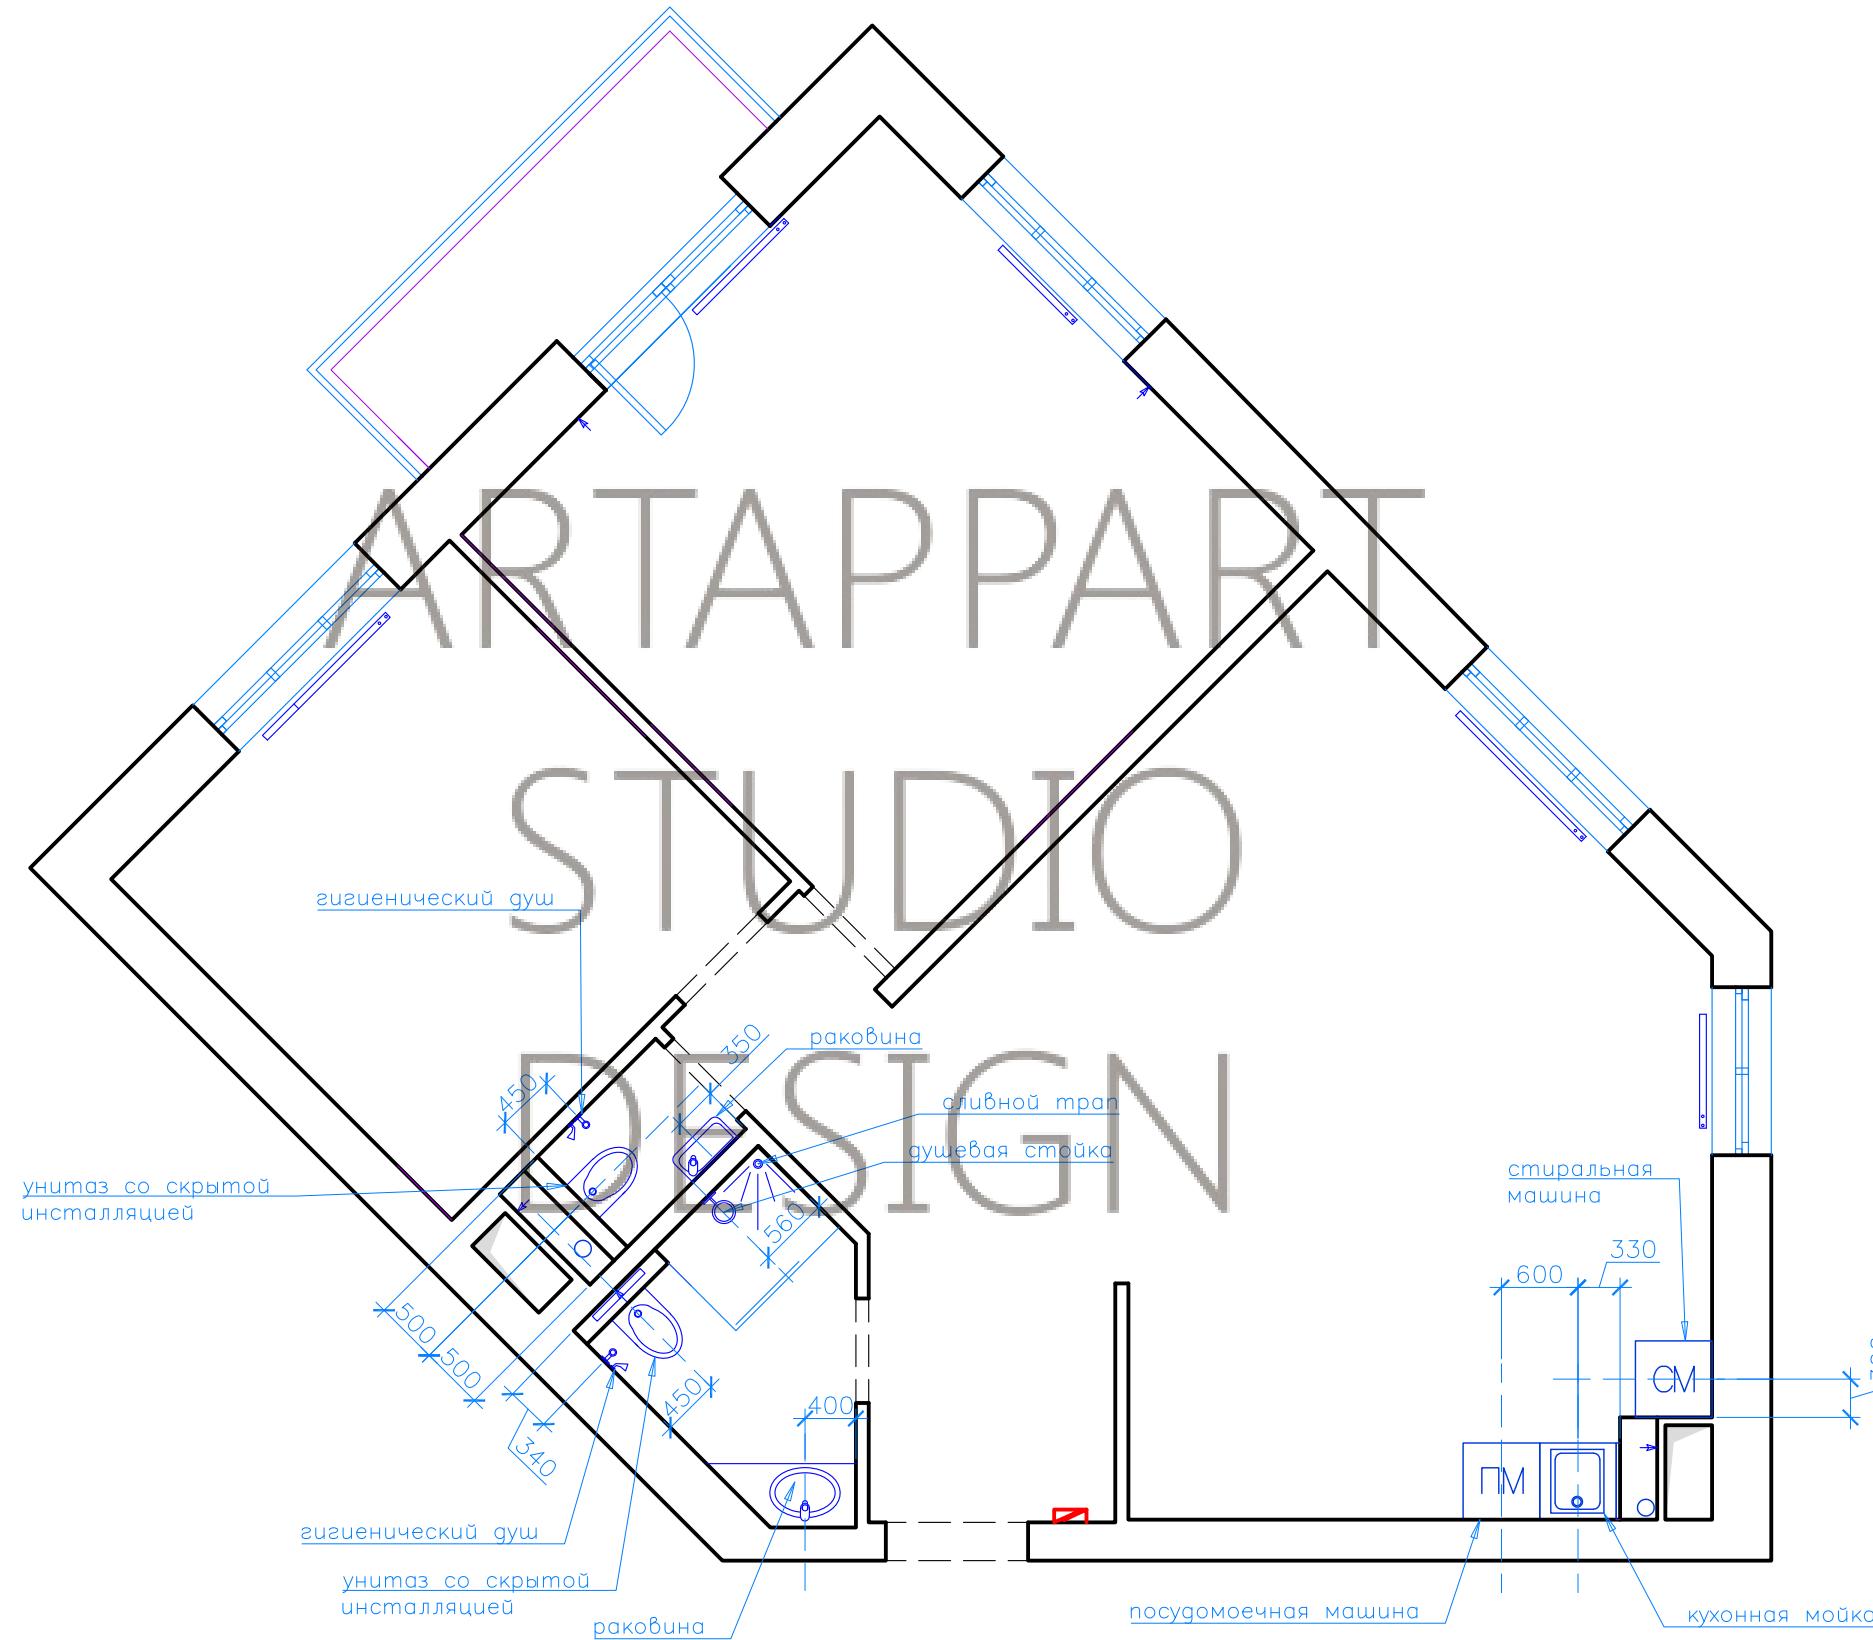

### Примечание:

При необходимости, запросить ТЗ для установки  
водорозеток у производителей оборудования

				Лист	Листовъ	Масштаб
				М 1: 60		
Дизайнер				План расстановки сан. тех. оборудования		
Заказчик						

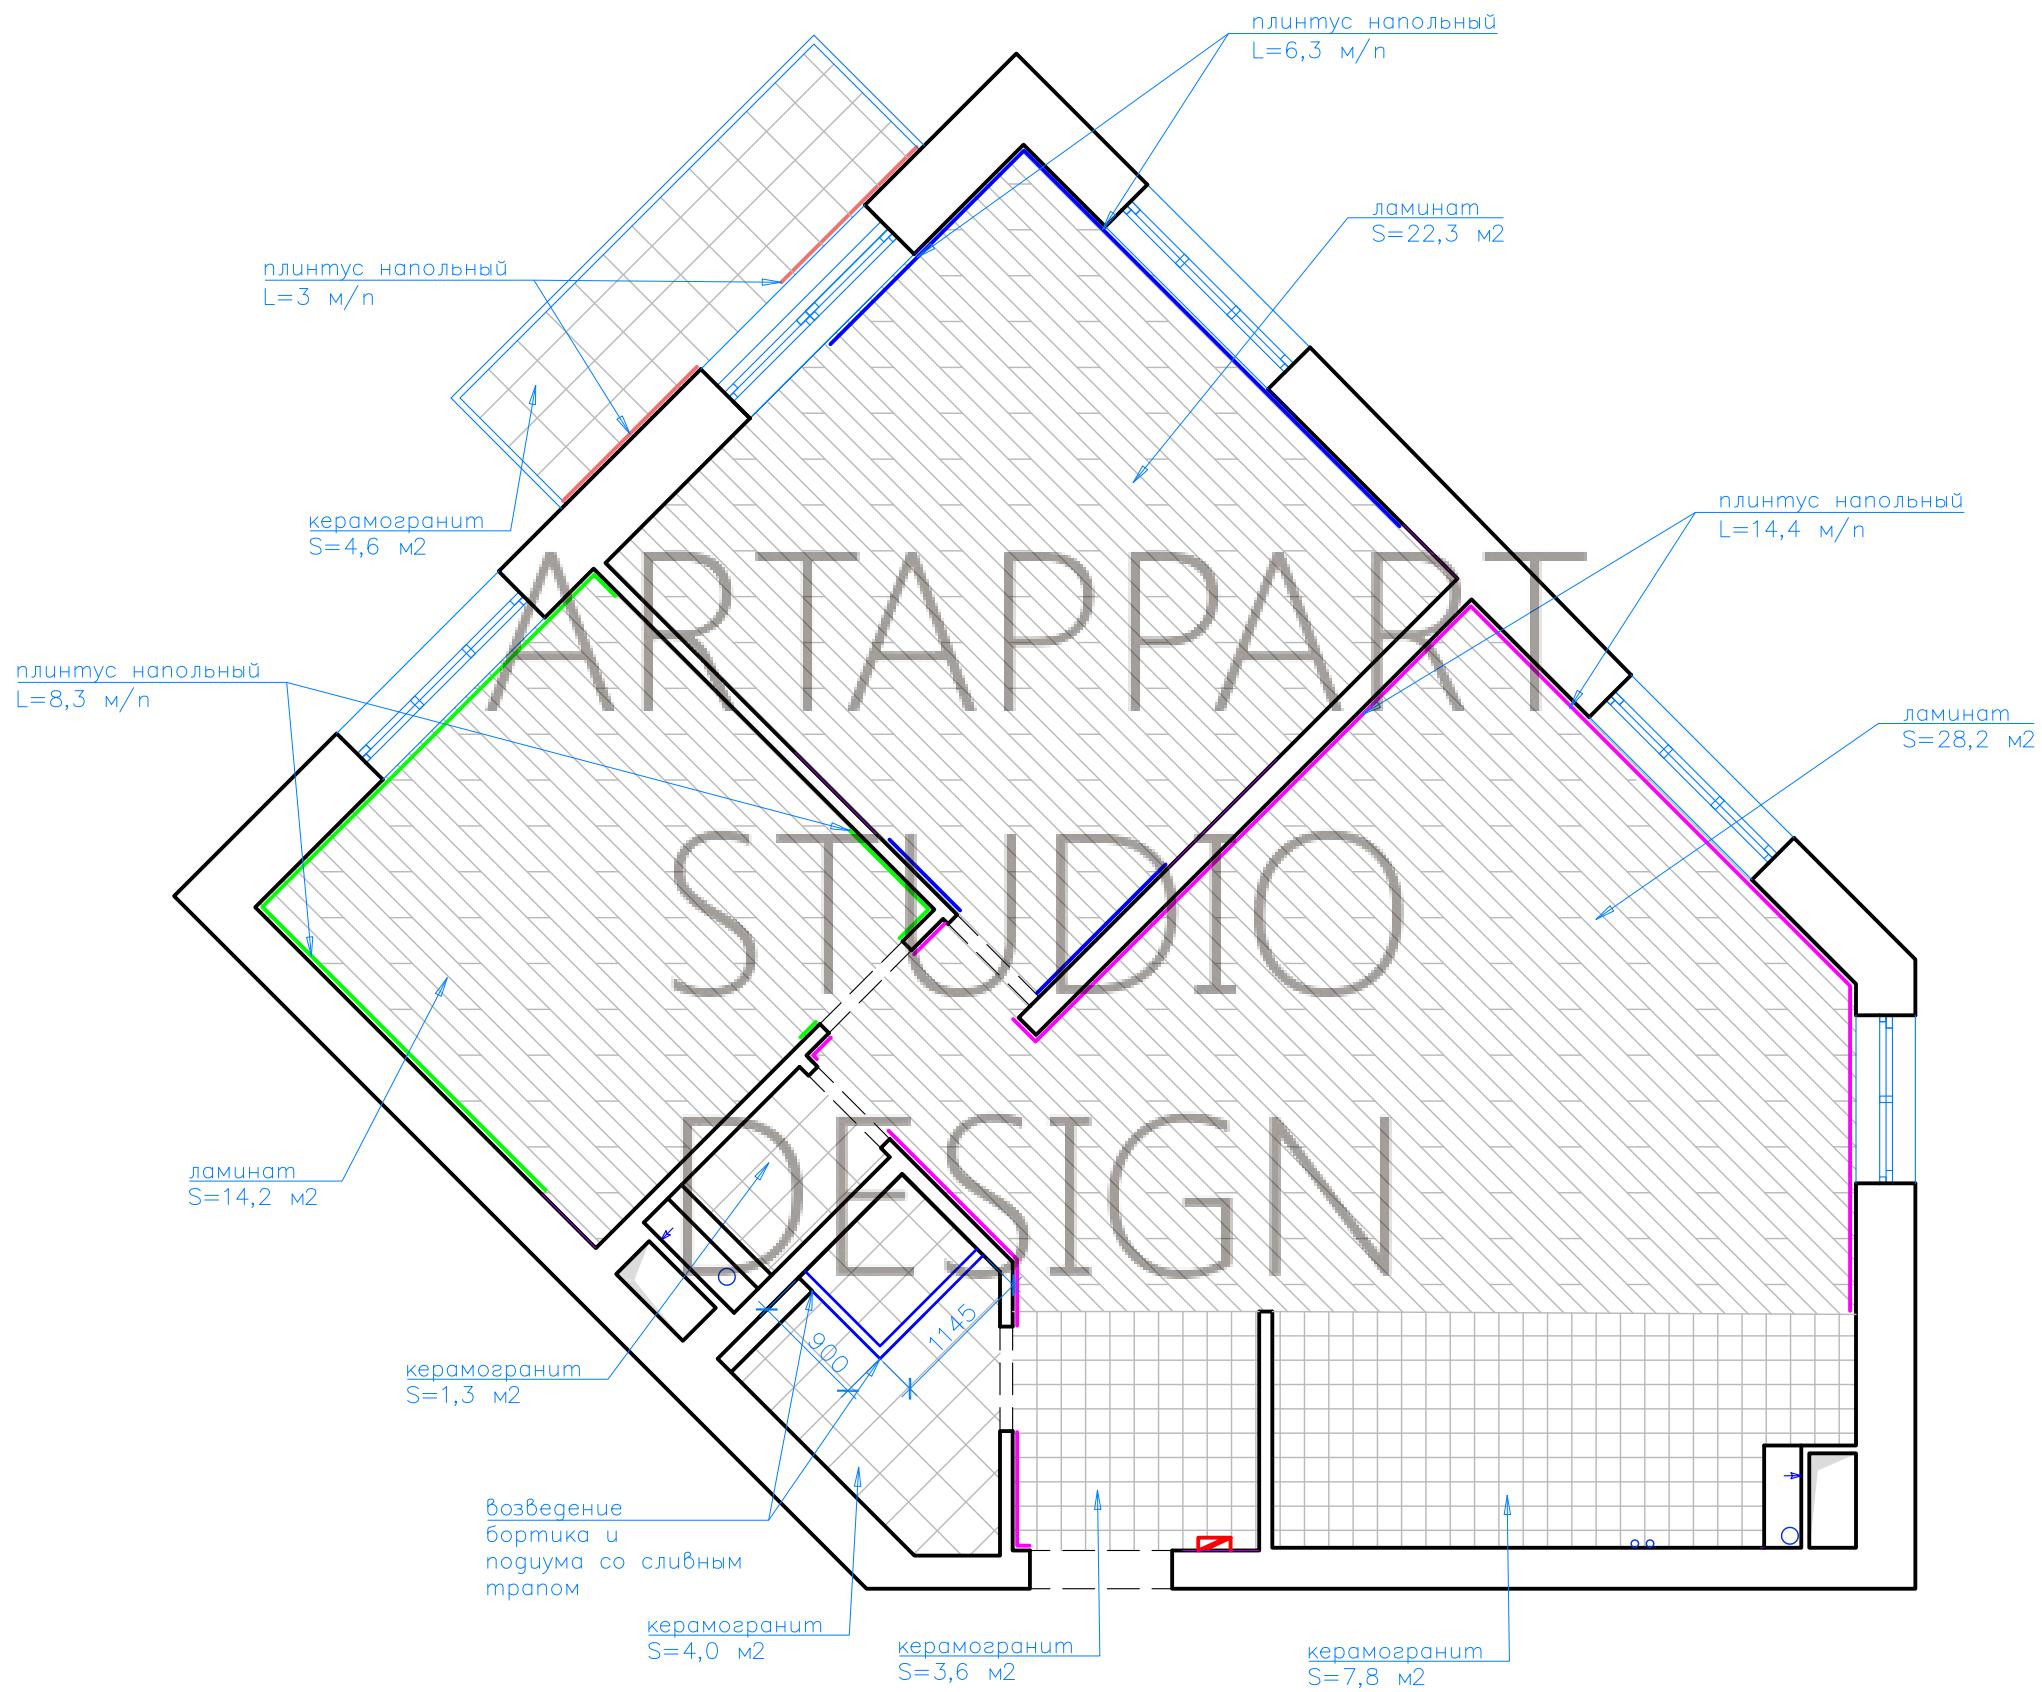

Примечание:

Площади покрытий даны без учета запаса.


Лист	Листов	Масштаб
		M 1: 60

Дизайнер  
Заказчик

План полов и напольных покрытий



ARTAPPART  
DESIGN  
STUDIO

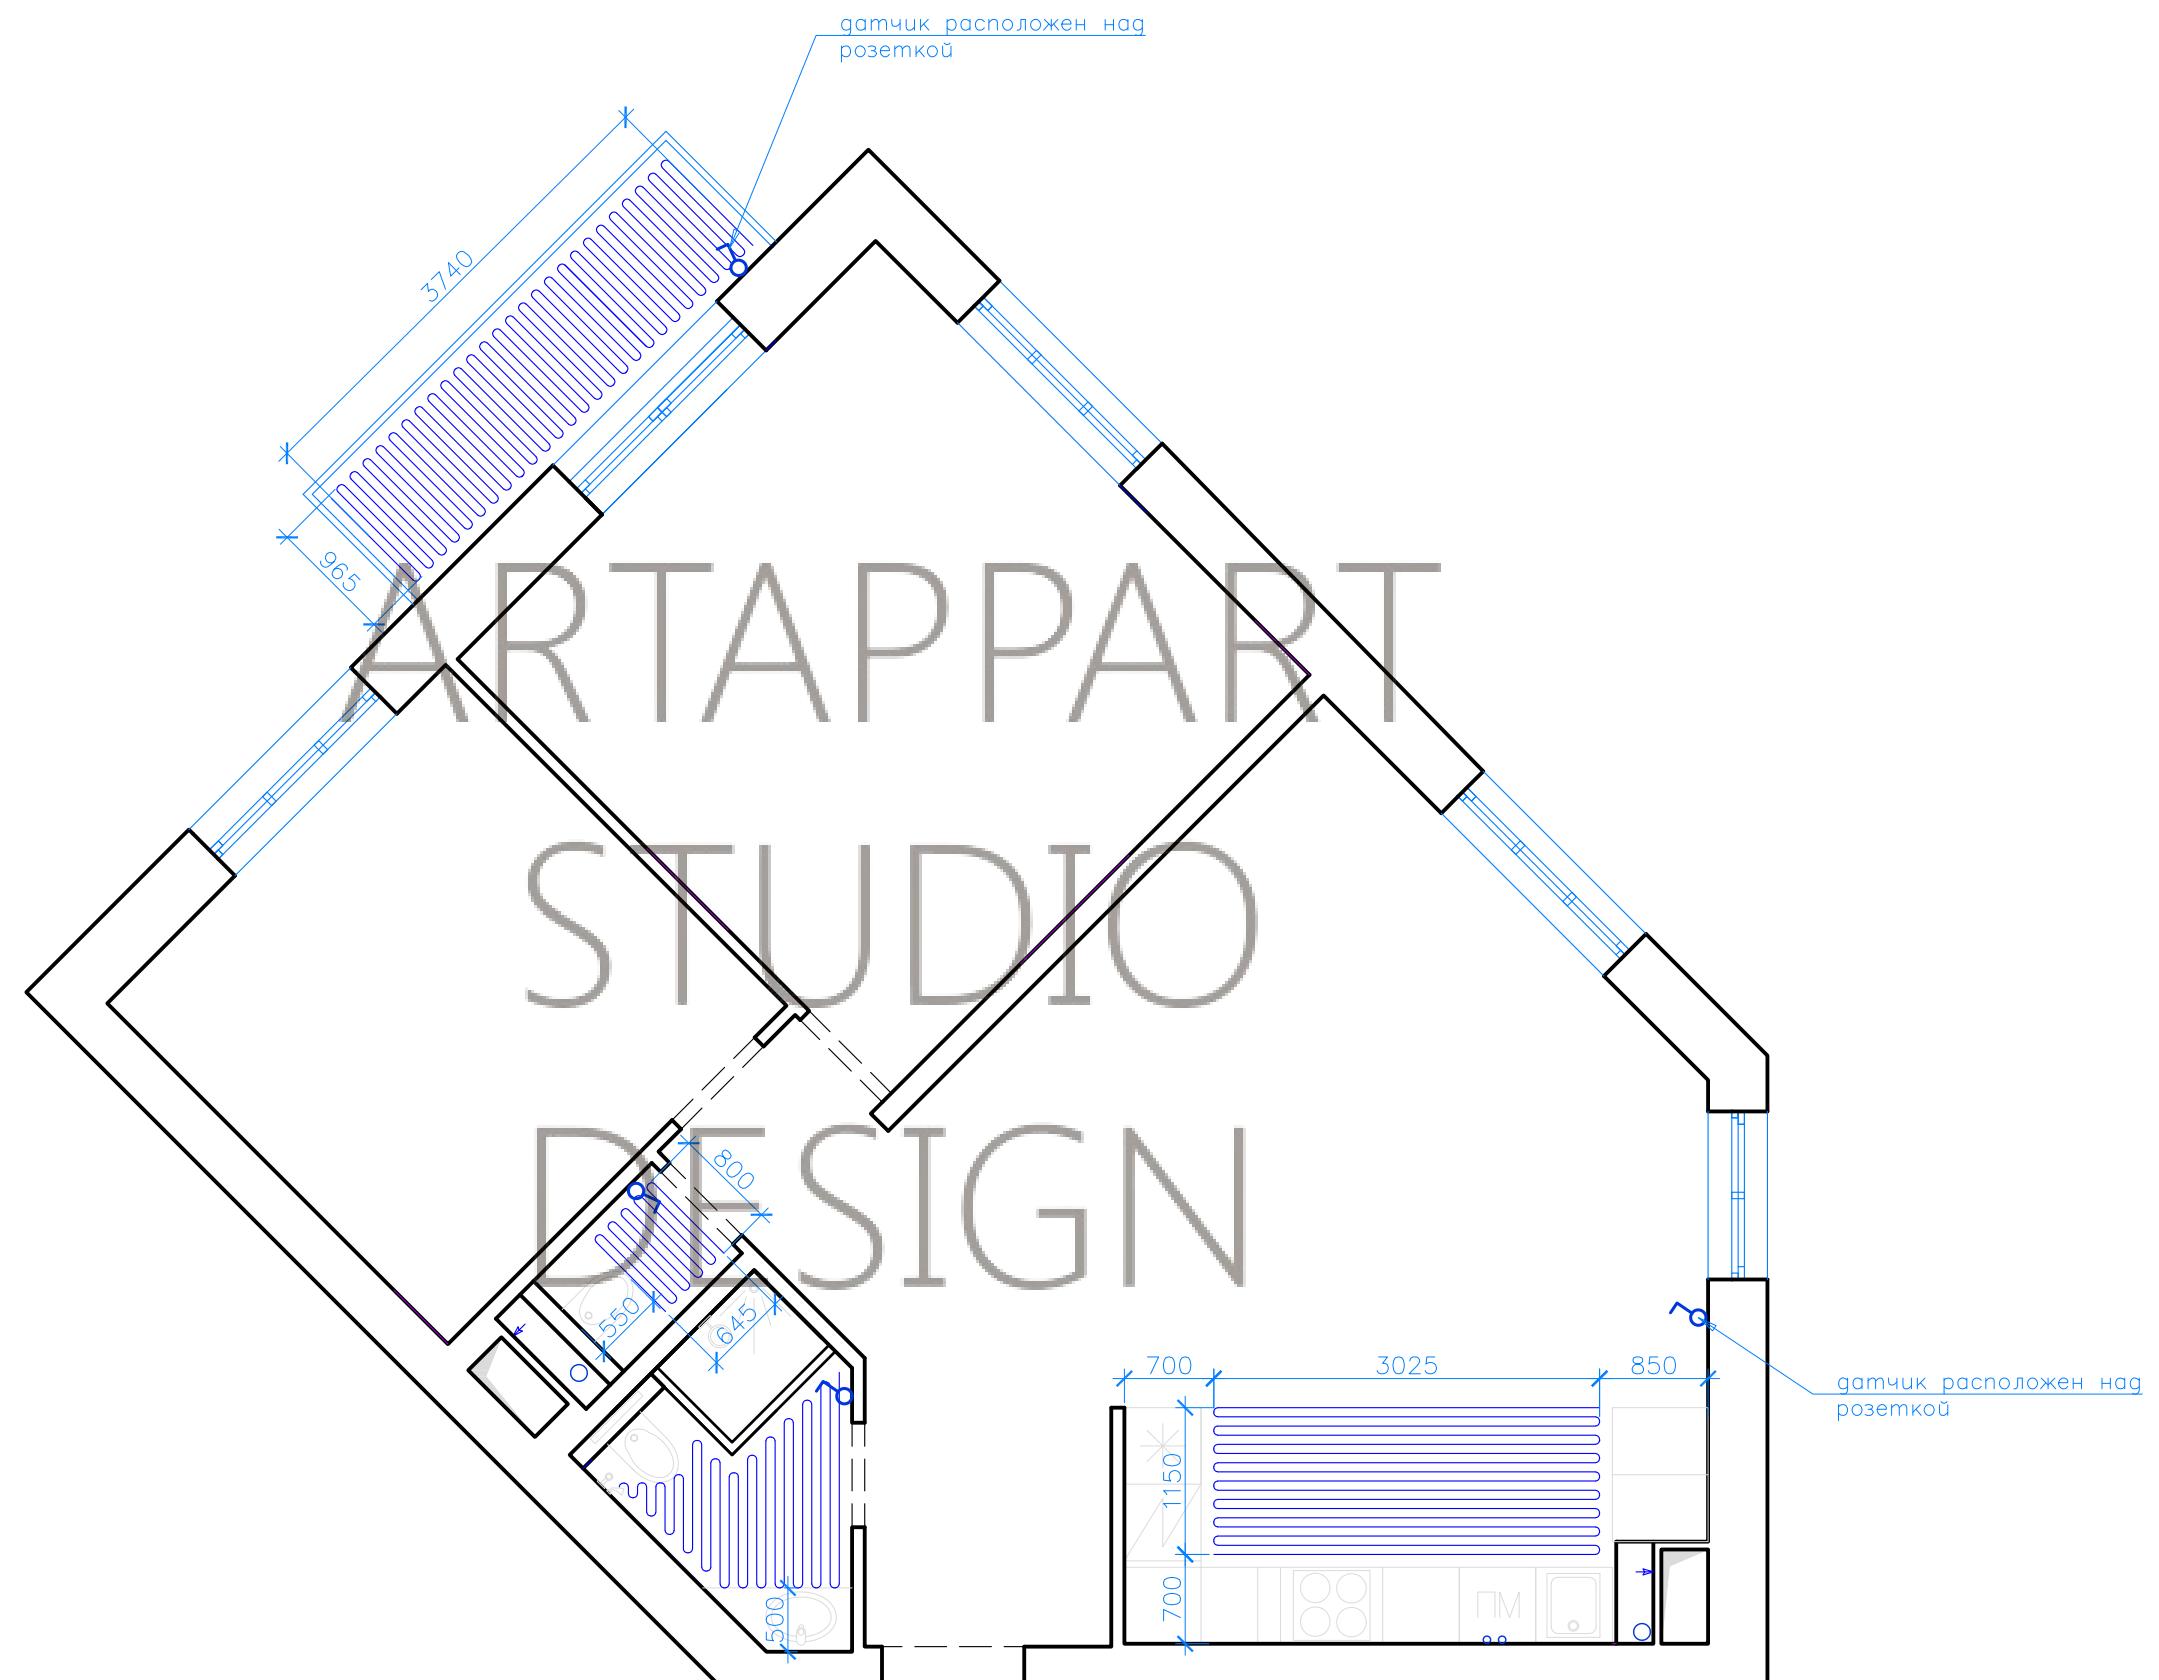


Условные обозначения:

— регулятор электрического теплого пола

Примечание:

- Границы расположения теплого пола удалены от напольных элементов мебели, стен и прочих конструкций на 100мм, если не указано иное.
- Терморегуляторы расположить на высоте 400мм на оси электроустановочного оборудования, если не указано иное.
- Все терморегуляторы установить посередине простенка, либо на расстоянии 250 мм от угла, если не указано иное.

				Лист	Листов	Масштаб
						M 1:60
Дизайнер	Заказчик	План "теплых" полов			ARTAPPART DESIGN STUDIO	

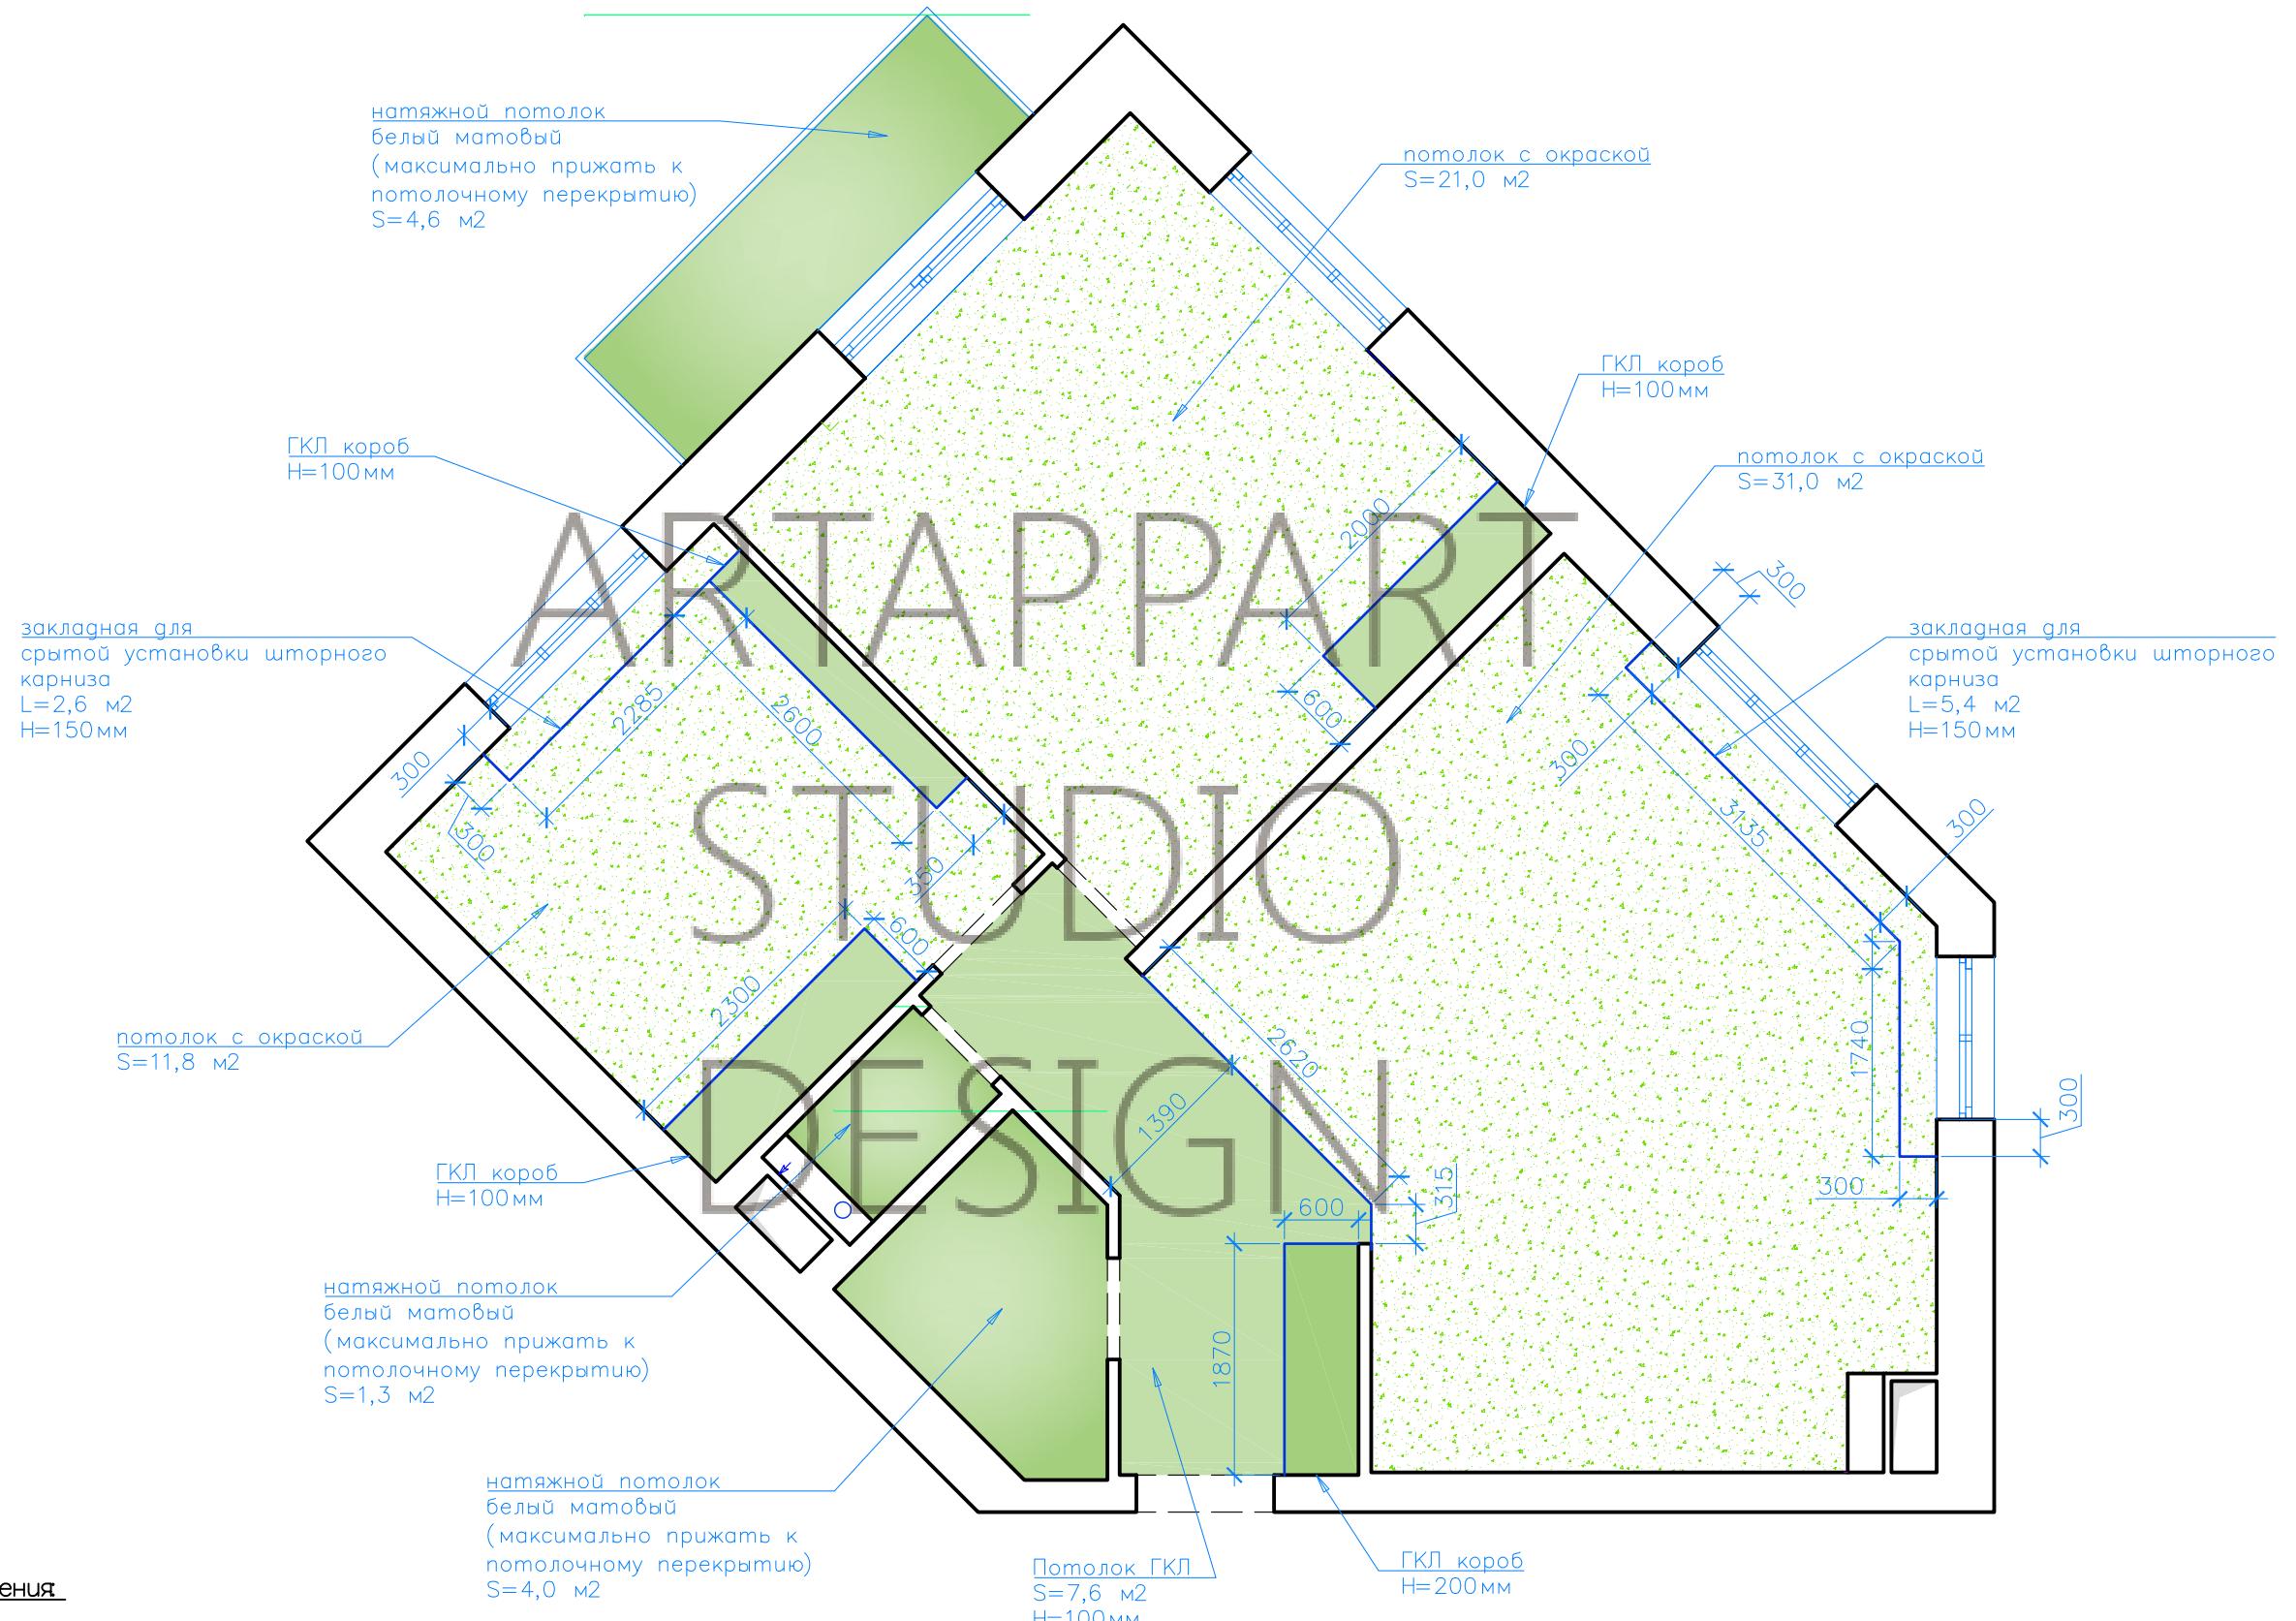

## Условные обозначения



— подшивной потолок ГКЛ



– потолок с окраской




— натяжной потолок

### Примечание:

1. Все покрытия белого цвета, если не указано иное.
  2. За исходный уровень принят уровень потолка с учетом проведенных мероприятий по выравниванию и звукоизоляции.
  3. Натяжные потолки монтируются на минимально возможном расстоянии от перекрытия, если не указано иное.

				Лист	Листовъ	Масштаб
						M 1: 60
Дизайнер						
Заказчик				План потолков		

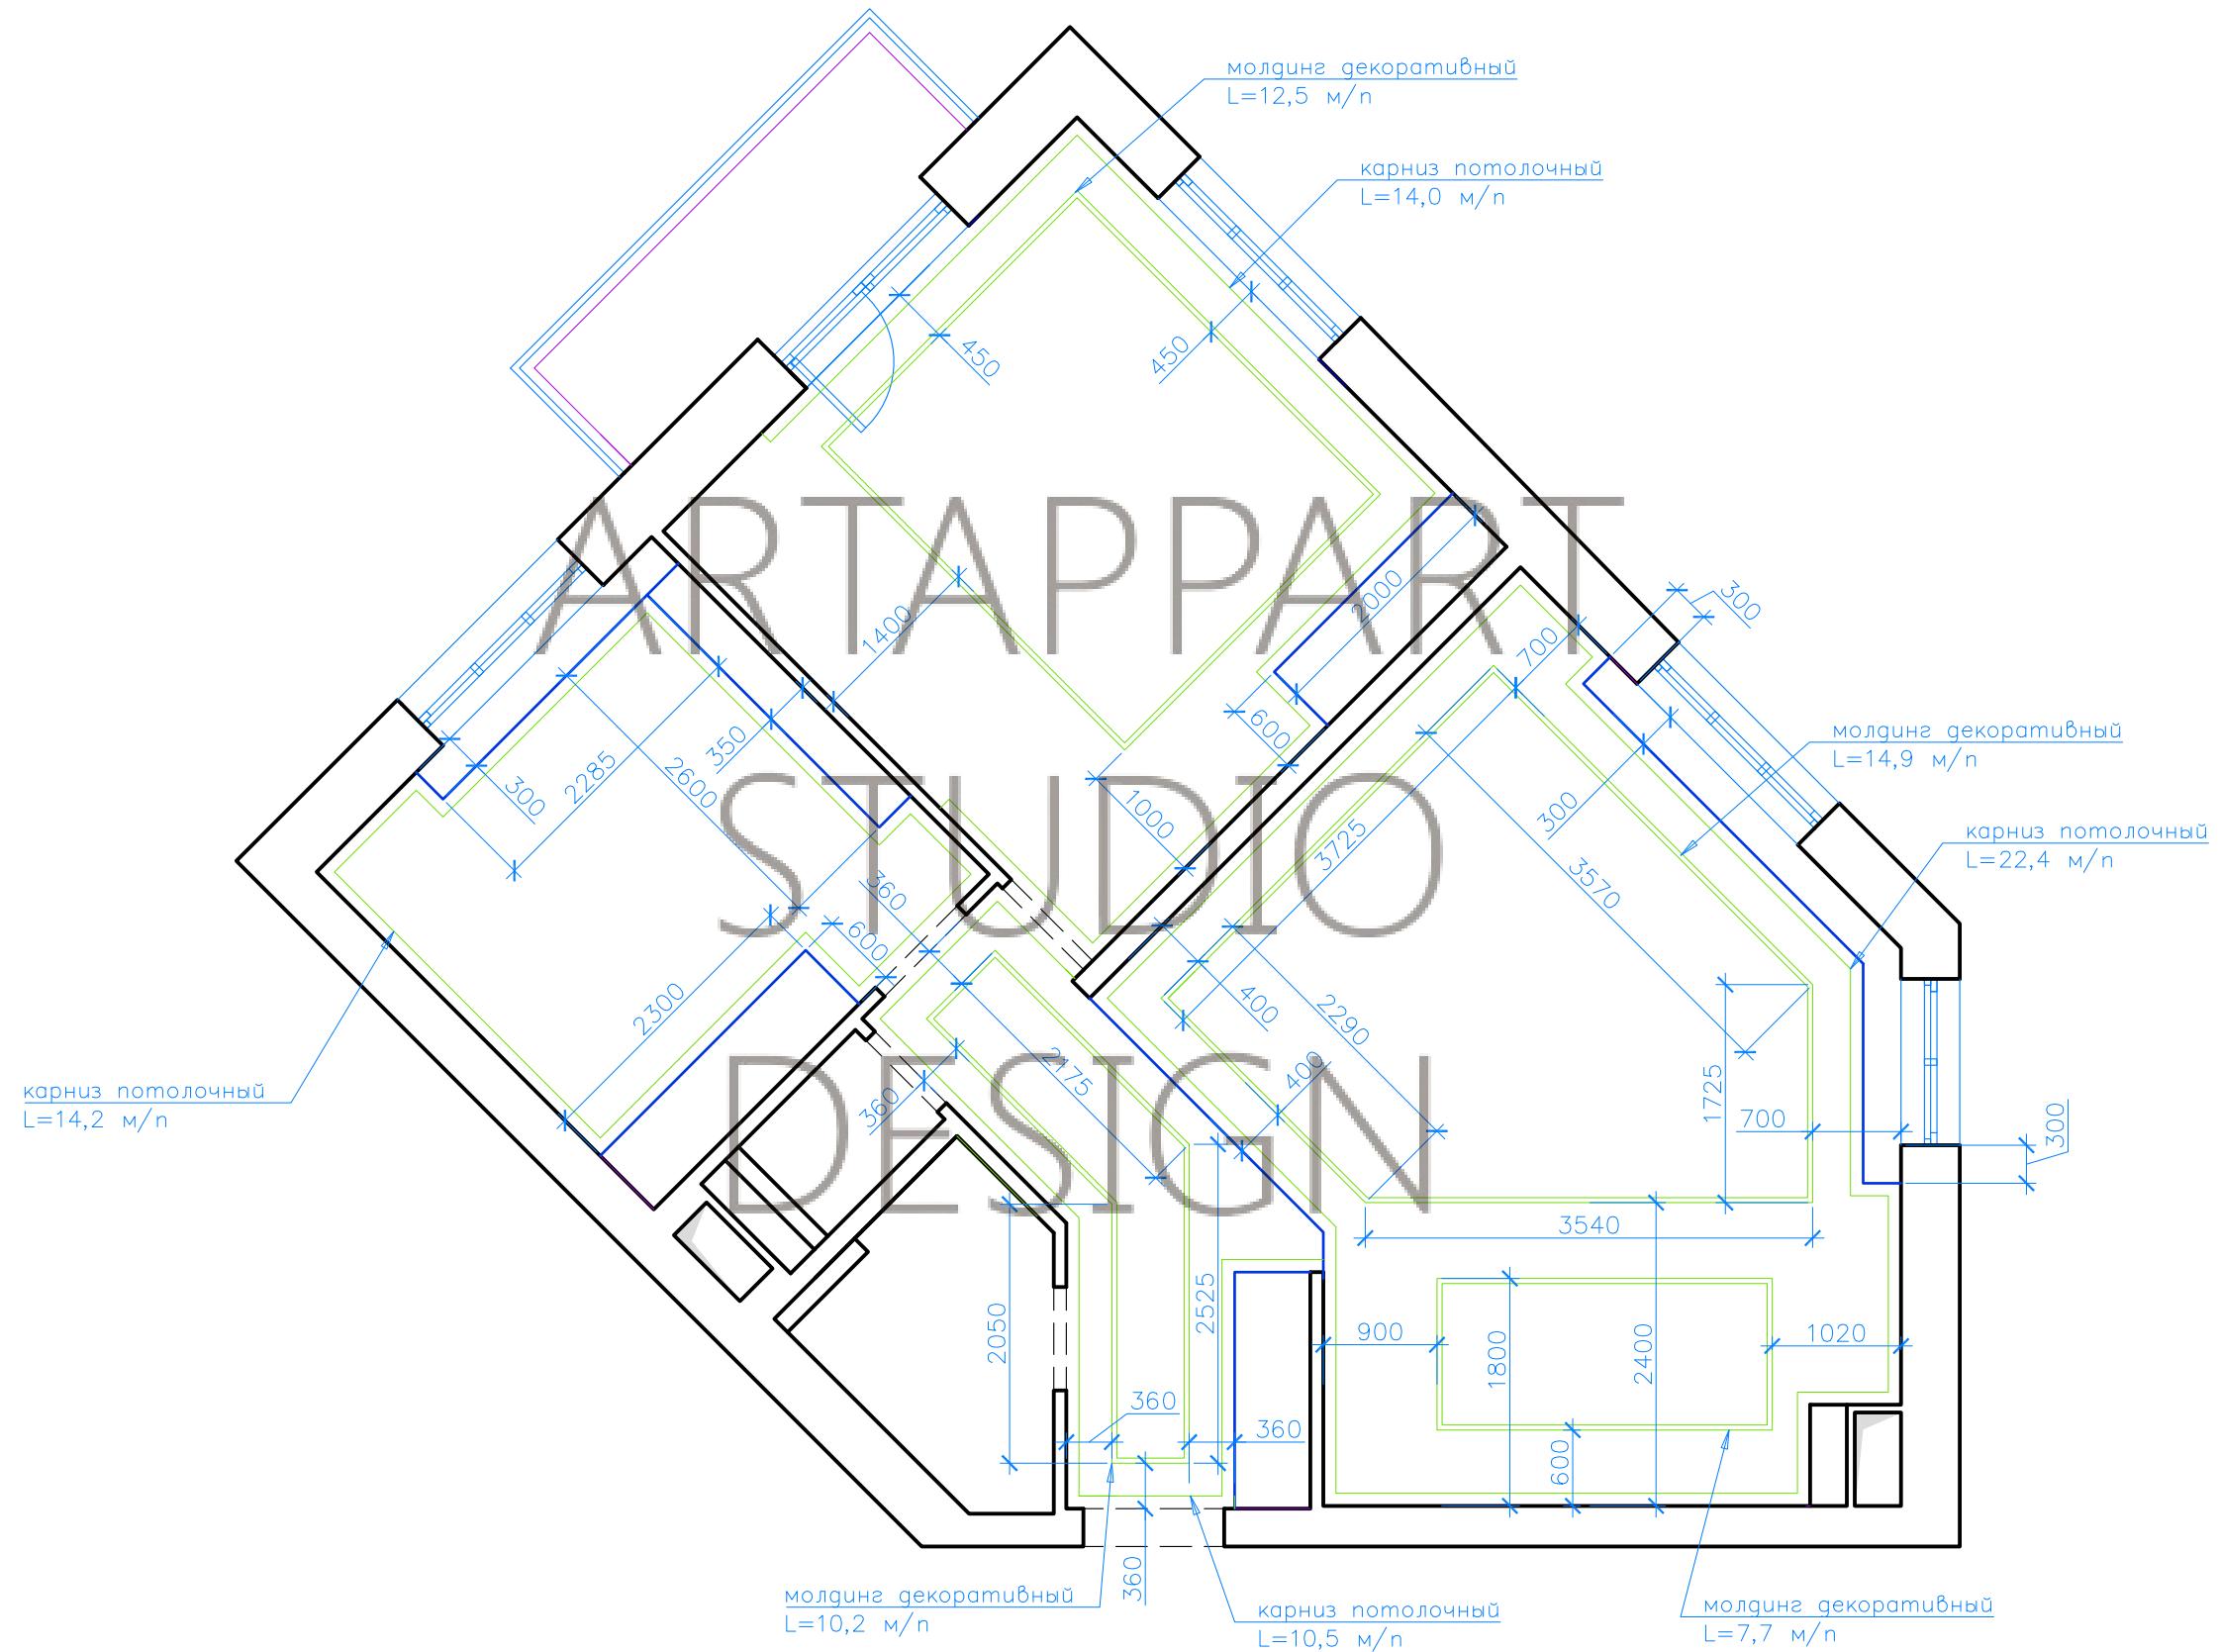


### Условные обозначения:

## – ППУ декор

Примечание: весь пенополиуретановый декор белого цвета, если не указано иное


				Лист	Листовъ	Масштаб
						M 1: 60
Дизайнер						
Заказчик						

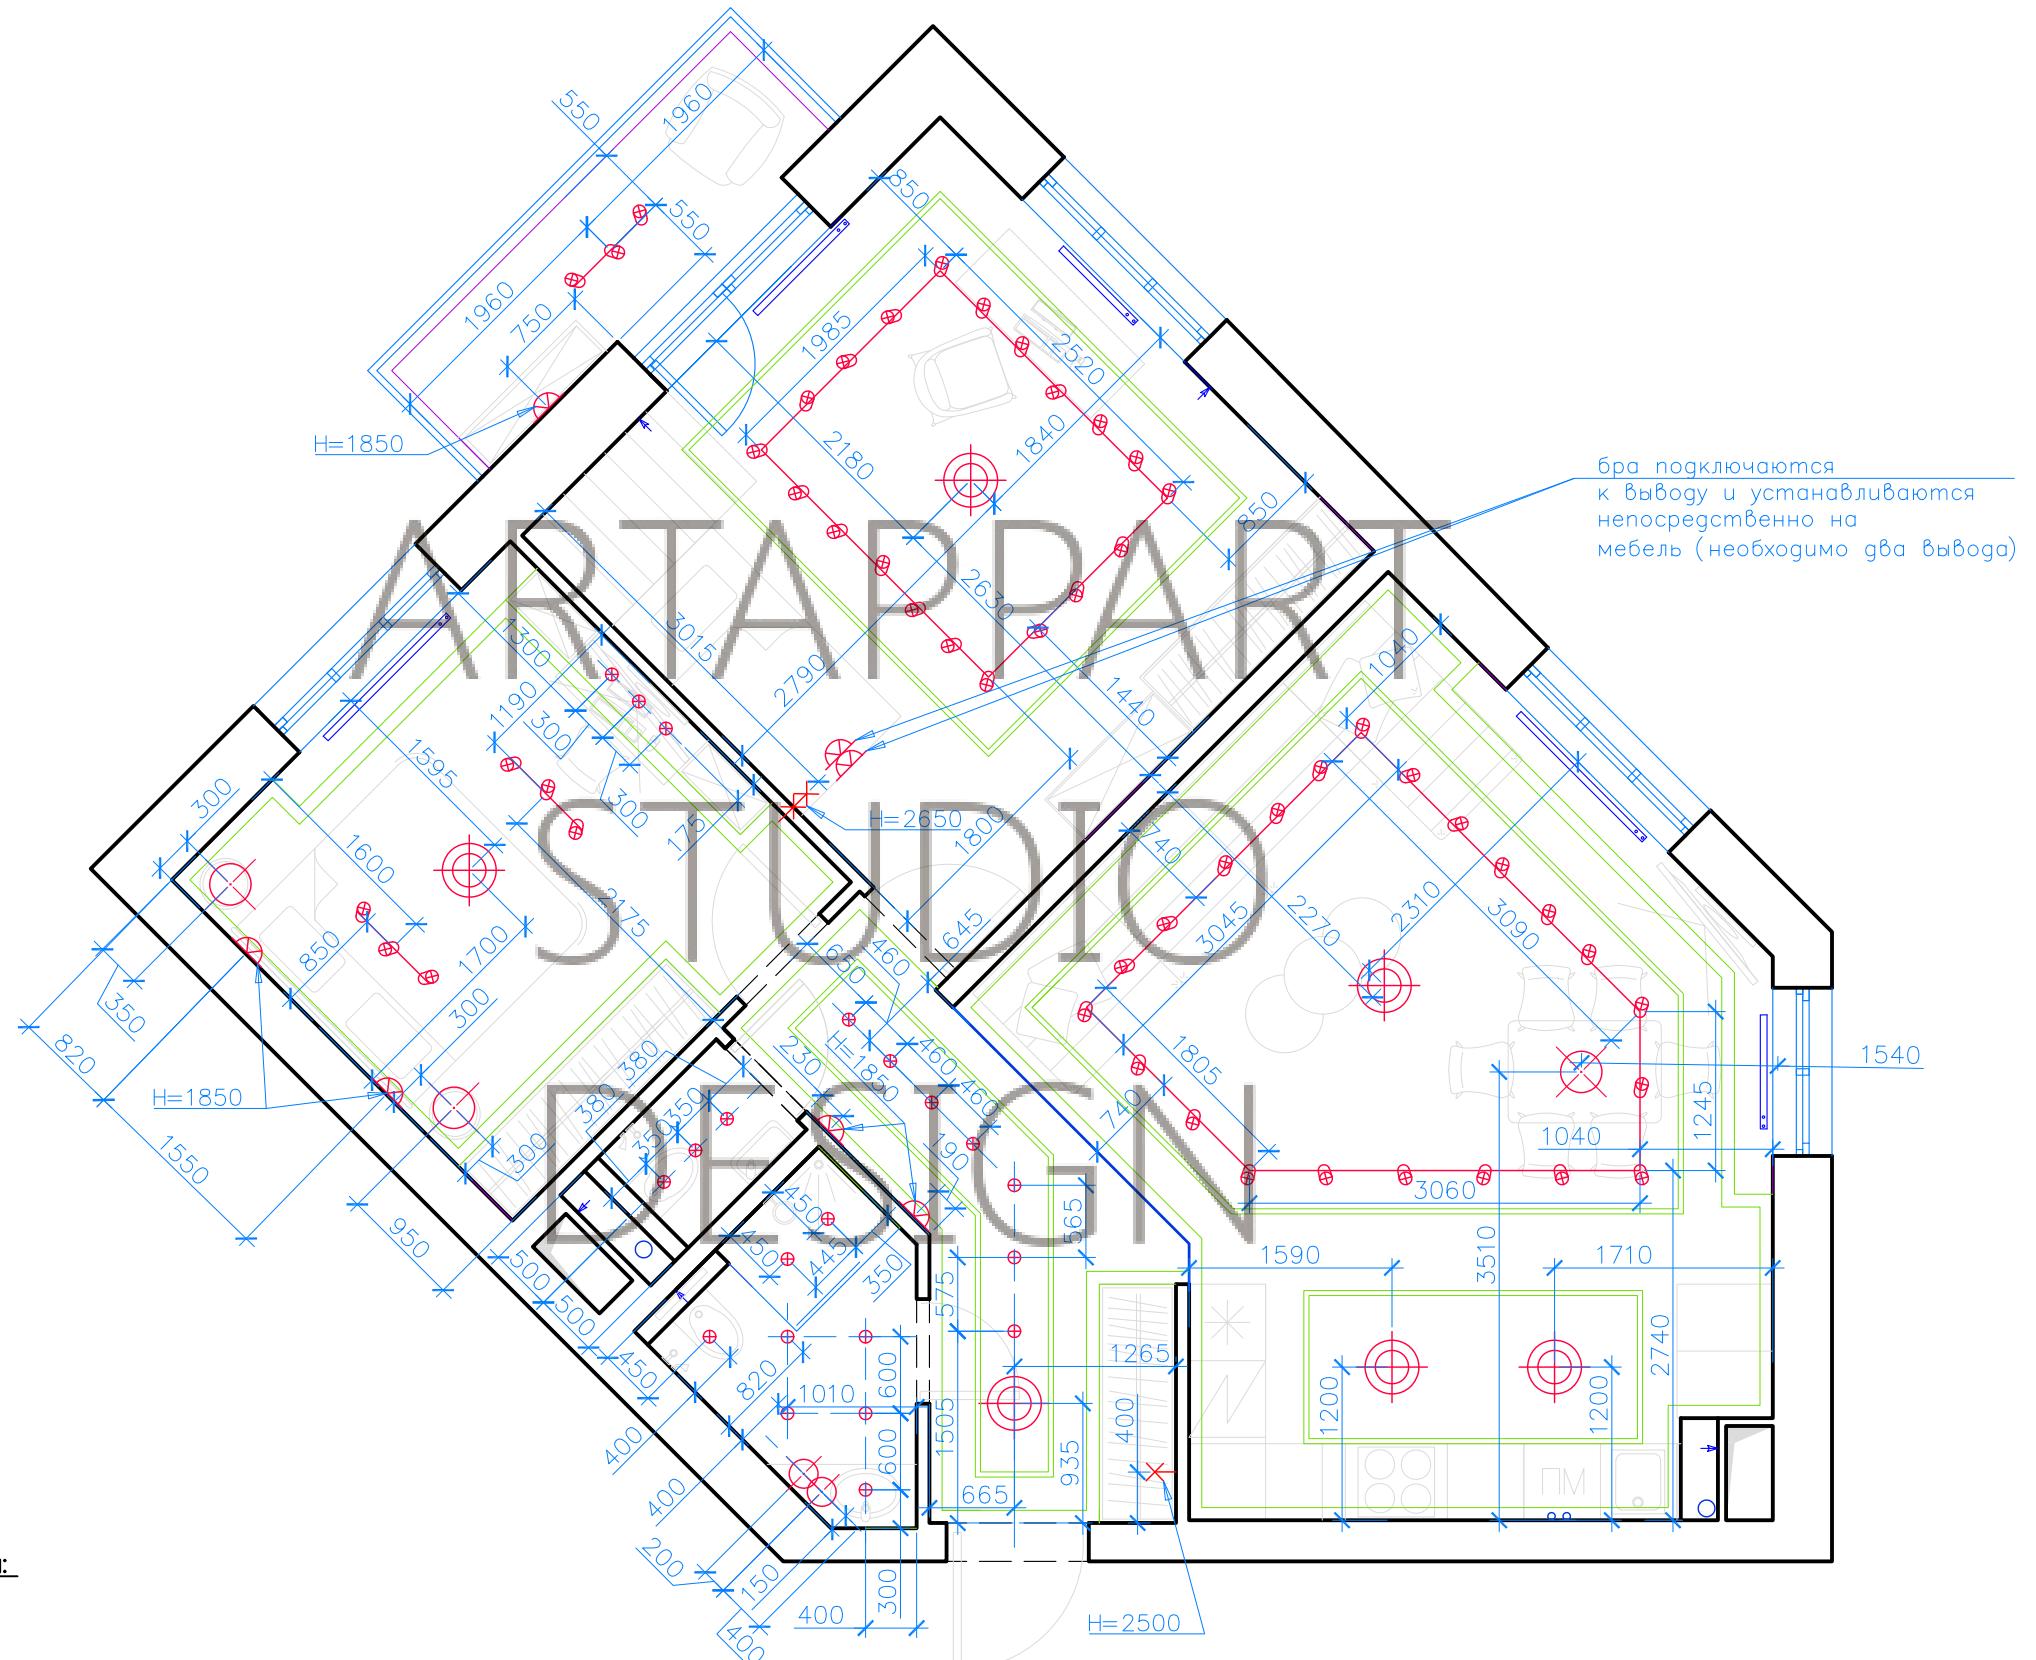

Условные обозначения:

- — люстра
- — подвес
- △ — бра/настен. светильник
- ✗ — эл. вывод
- ⊕ — точечный светильник

Лист	Листов	Масштаб
		M 1:60
План привязки осветительных приборов		
Дизайнер		
Заказчик		
ARTAPPART DESIGN STUDIO		

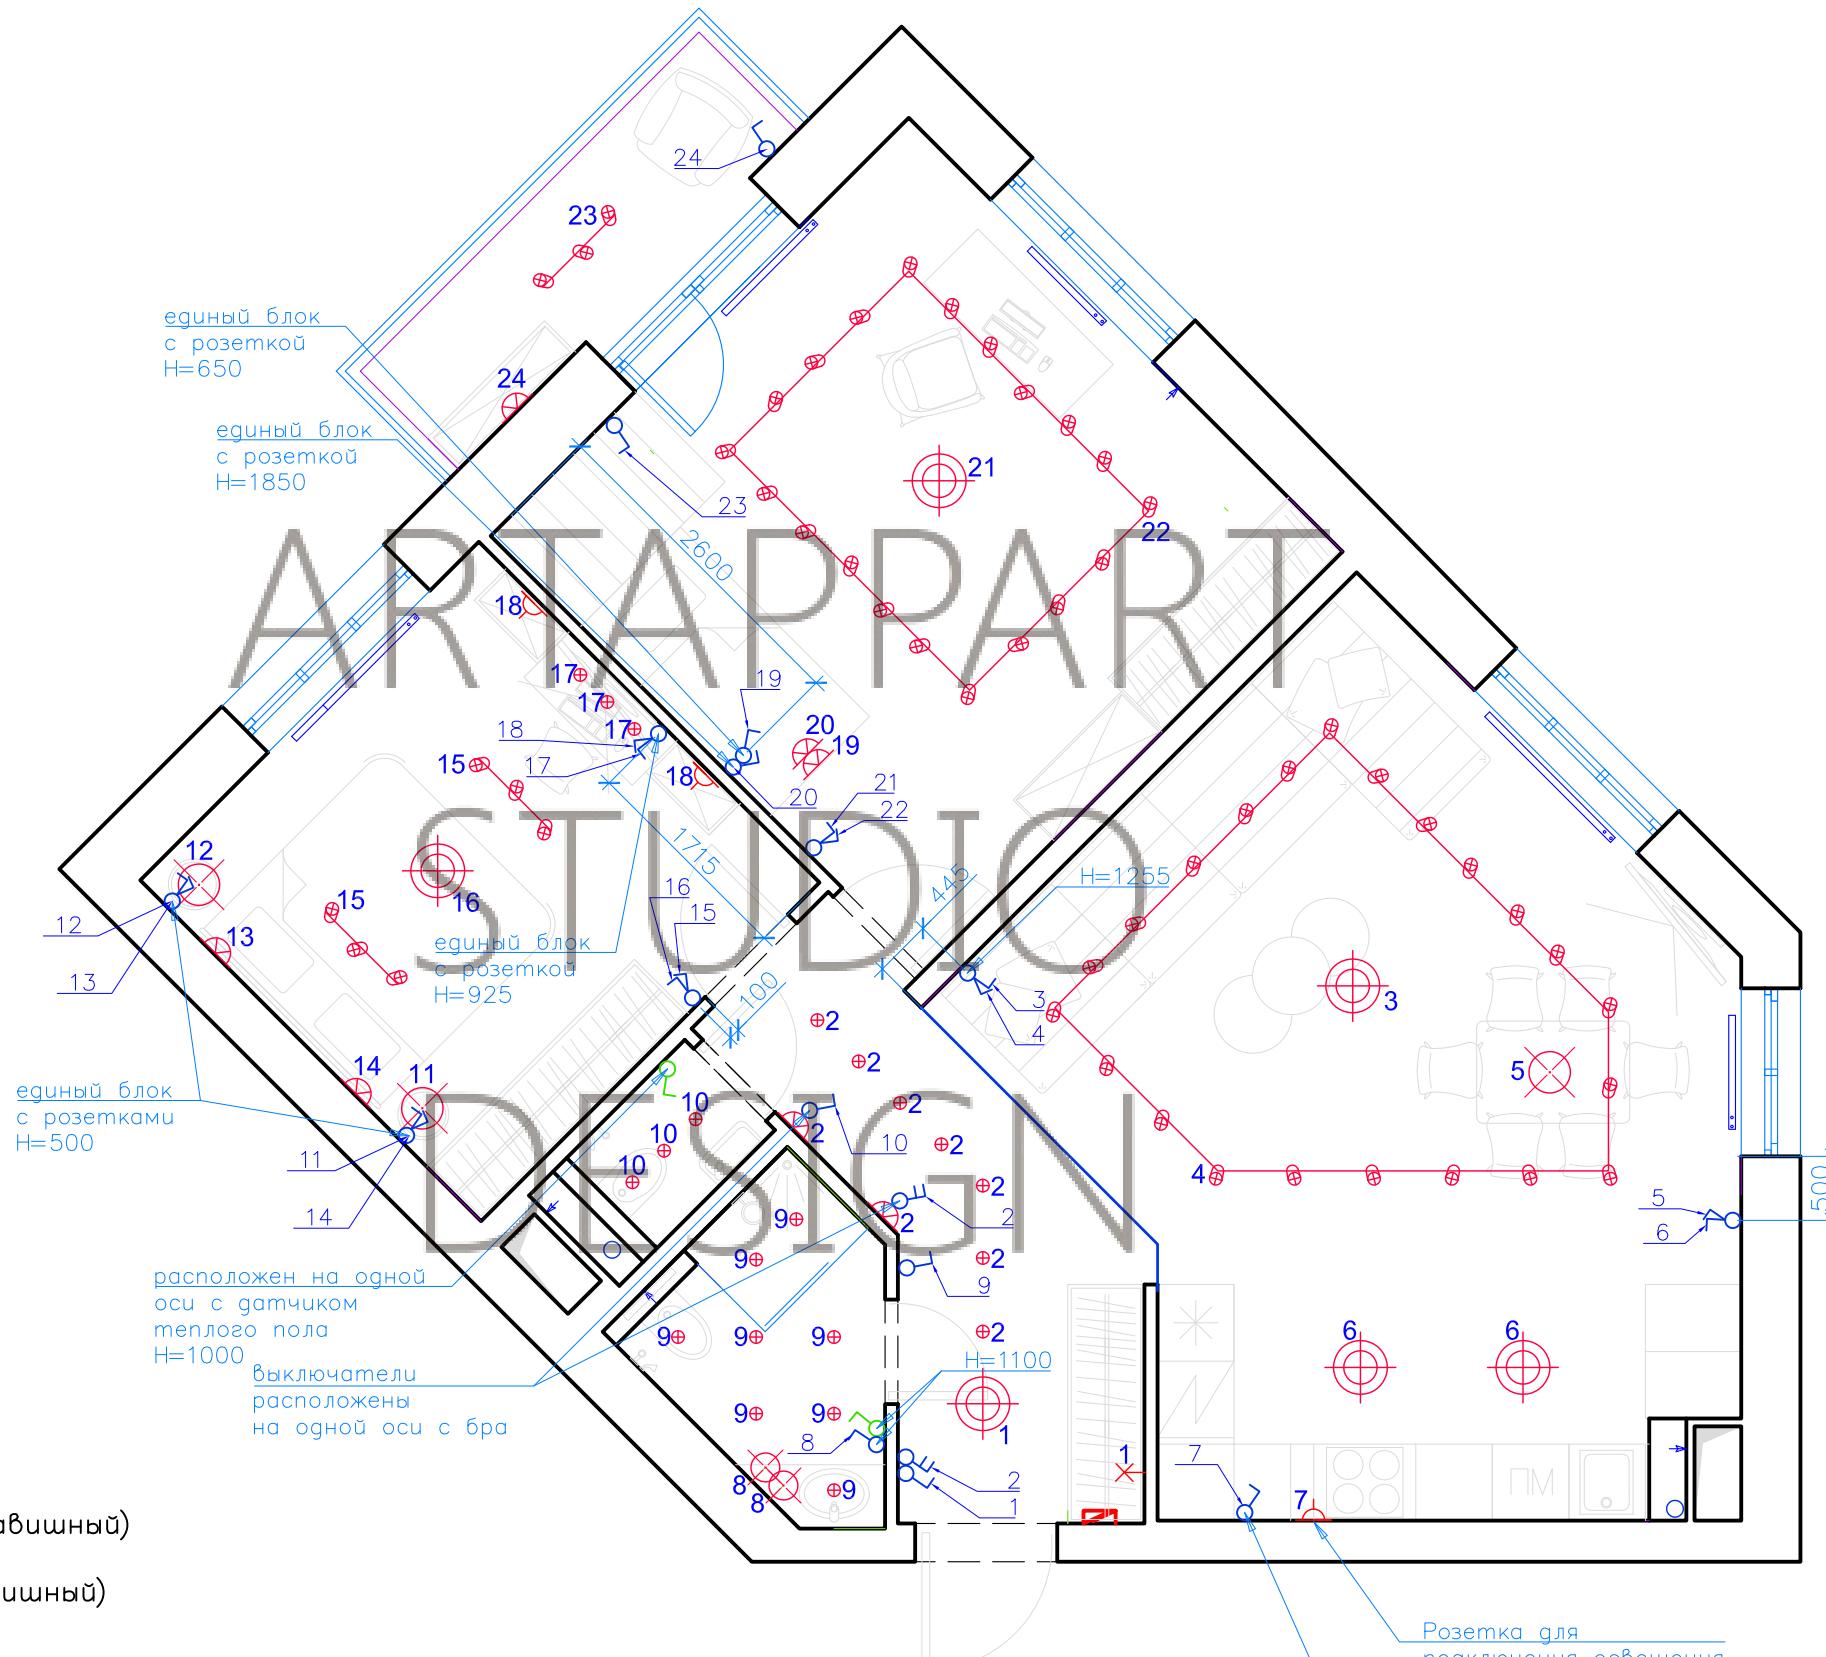


Условные обозначения:

- ↗ – выключатель (1-но клавишный)
- ↗ – Выключатель (2-ух клавишный)
- ↗ – переключатель
- ↗ – вкл. вентиляции

Примечание:

1. Все выключатели установить посередине простенка либо на расстоянии 250мм от угла, если не указано иное;
2. Высота до оси выключателя(–лей) 900мм от УЧП, если не указано иное;
3. Количество номеров групп светильников у выключателя определяет его тип: 1-но / 2-ух клавишный;
4. Привязки даны в мм от УЧП до осей приборов.
5. Для возможности редактирования рекомендуется оставлять выводы достаточной длины.

Лист	Листов	Масштаб
		M 1:60
Дизайнер		План разводки осветительных приборов на выключатели
Заказчик		ARTAPPART DESIGN STUDIO

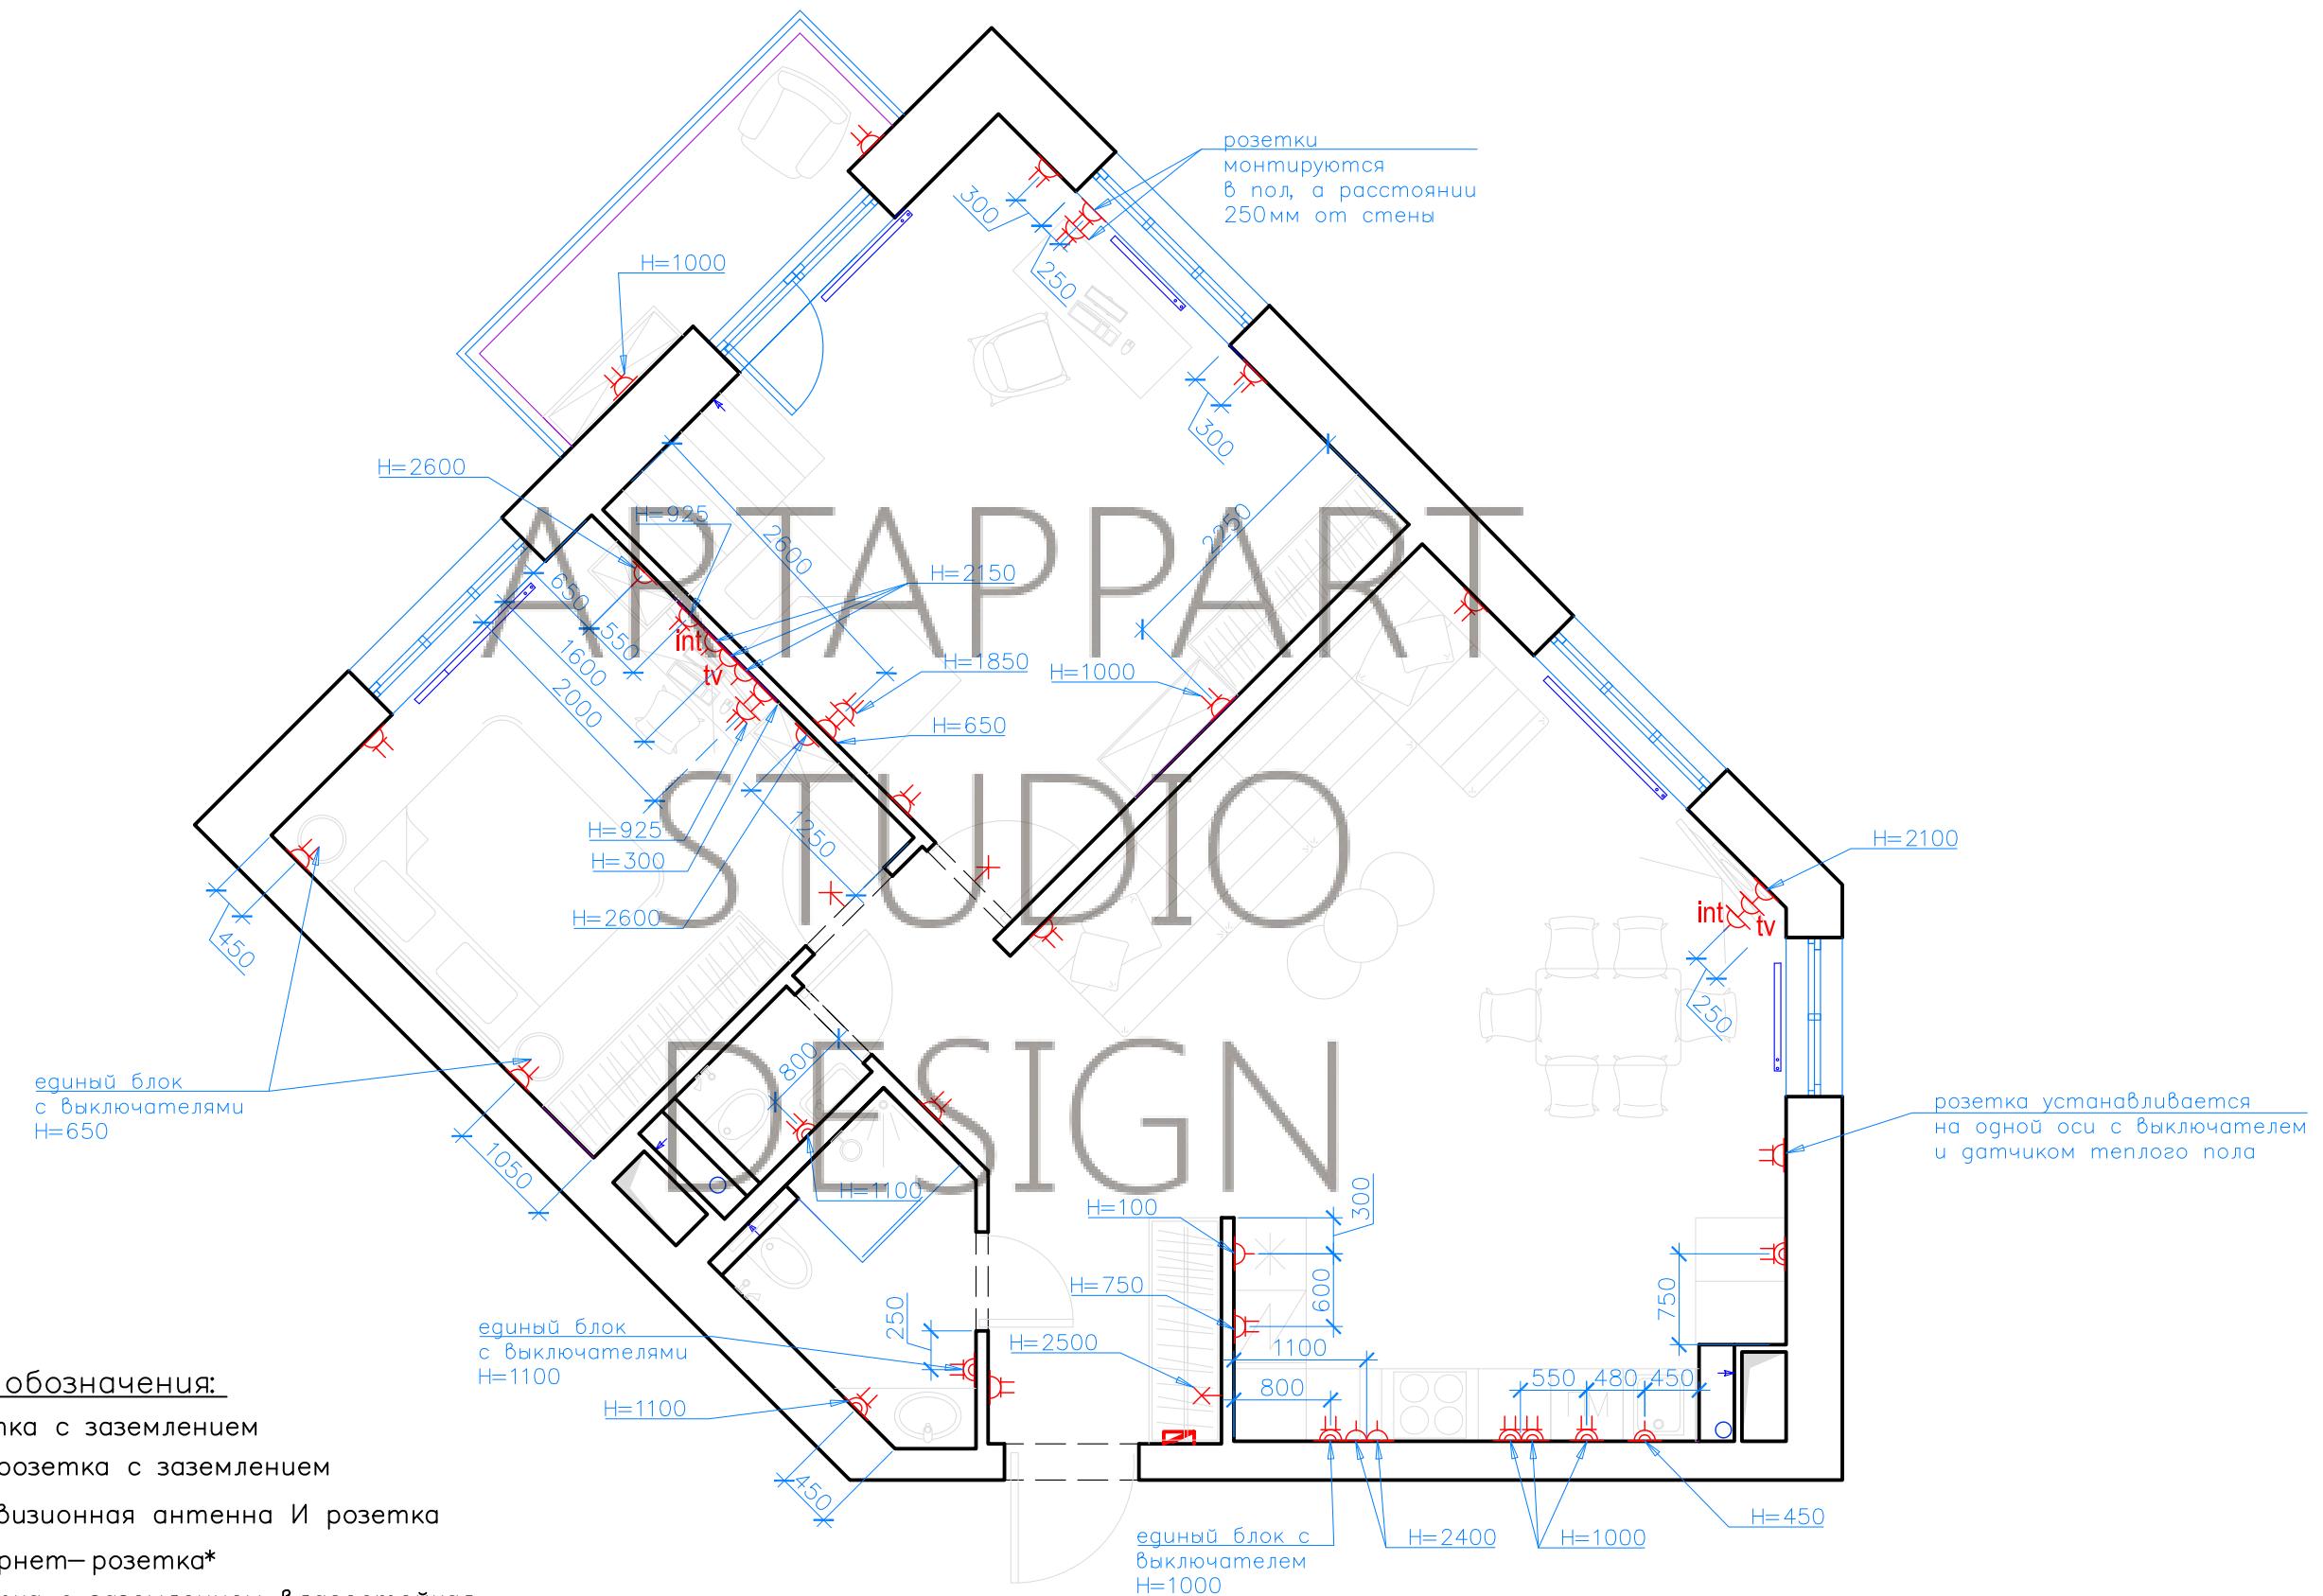


Условные обозначения:

- розетка с заземлением
- 2-я розетка с заземлением
- tv — телевизионная антenna И розетка
- int — интернет-розетка\*
- розетка с заземлением влагостойкая
- 2-я розетка с заземлением влагостойкая
- эл. вывод


Примечание:

1. Все розетки, кроме обозначенных, установить на высоте 300 мм от УЧП;
2. Розетки располагать посередине простенка либо на расстоянии 250мм от угла, если привязки не указаны;
3. Привязки даны в мм от УЧП до осей приборов.
4. Для возможности редактирования рекомендуется оставлять выводы достаточной длины.


Лист	Листов	Масштаб
		M 1:60
Дизайнер		План электрики и
Заказчик		электропроводов
		ARTAPPART DESIGN STUDIO

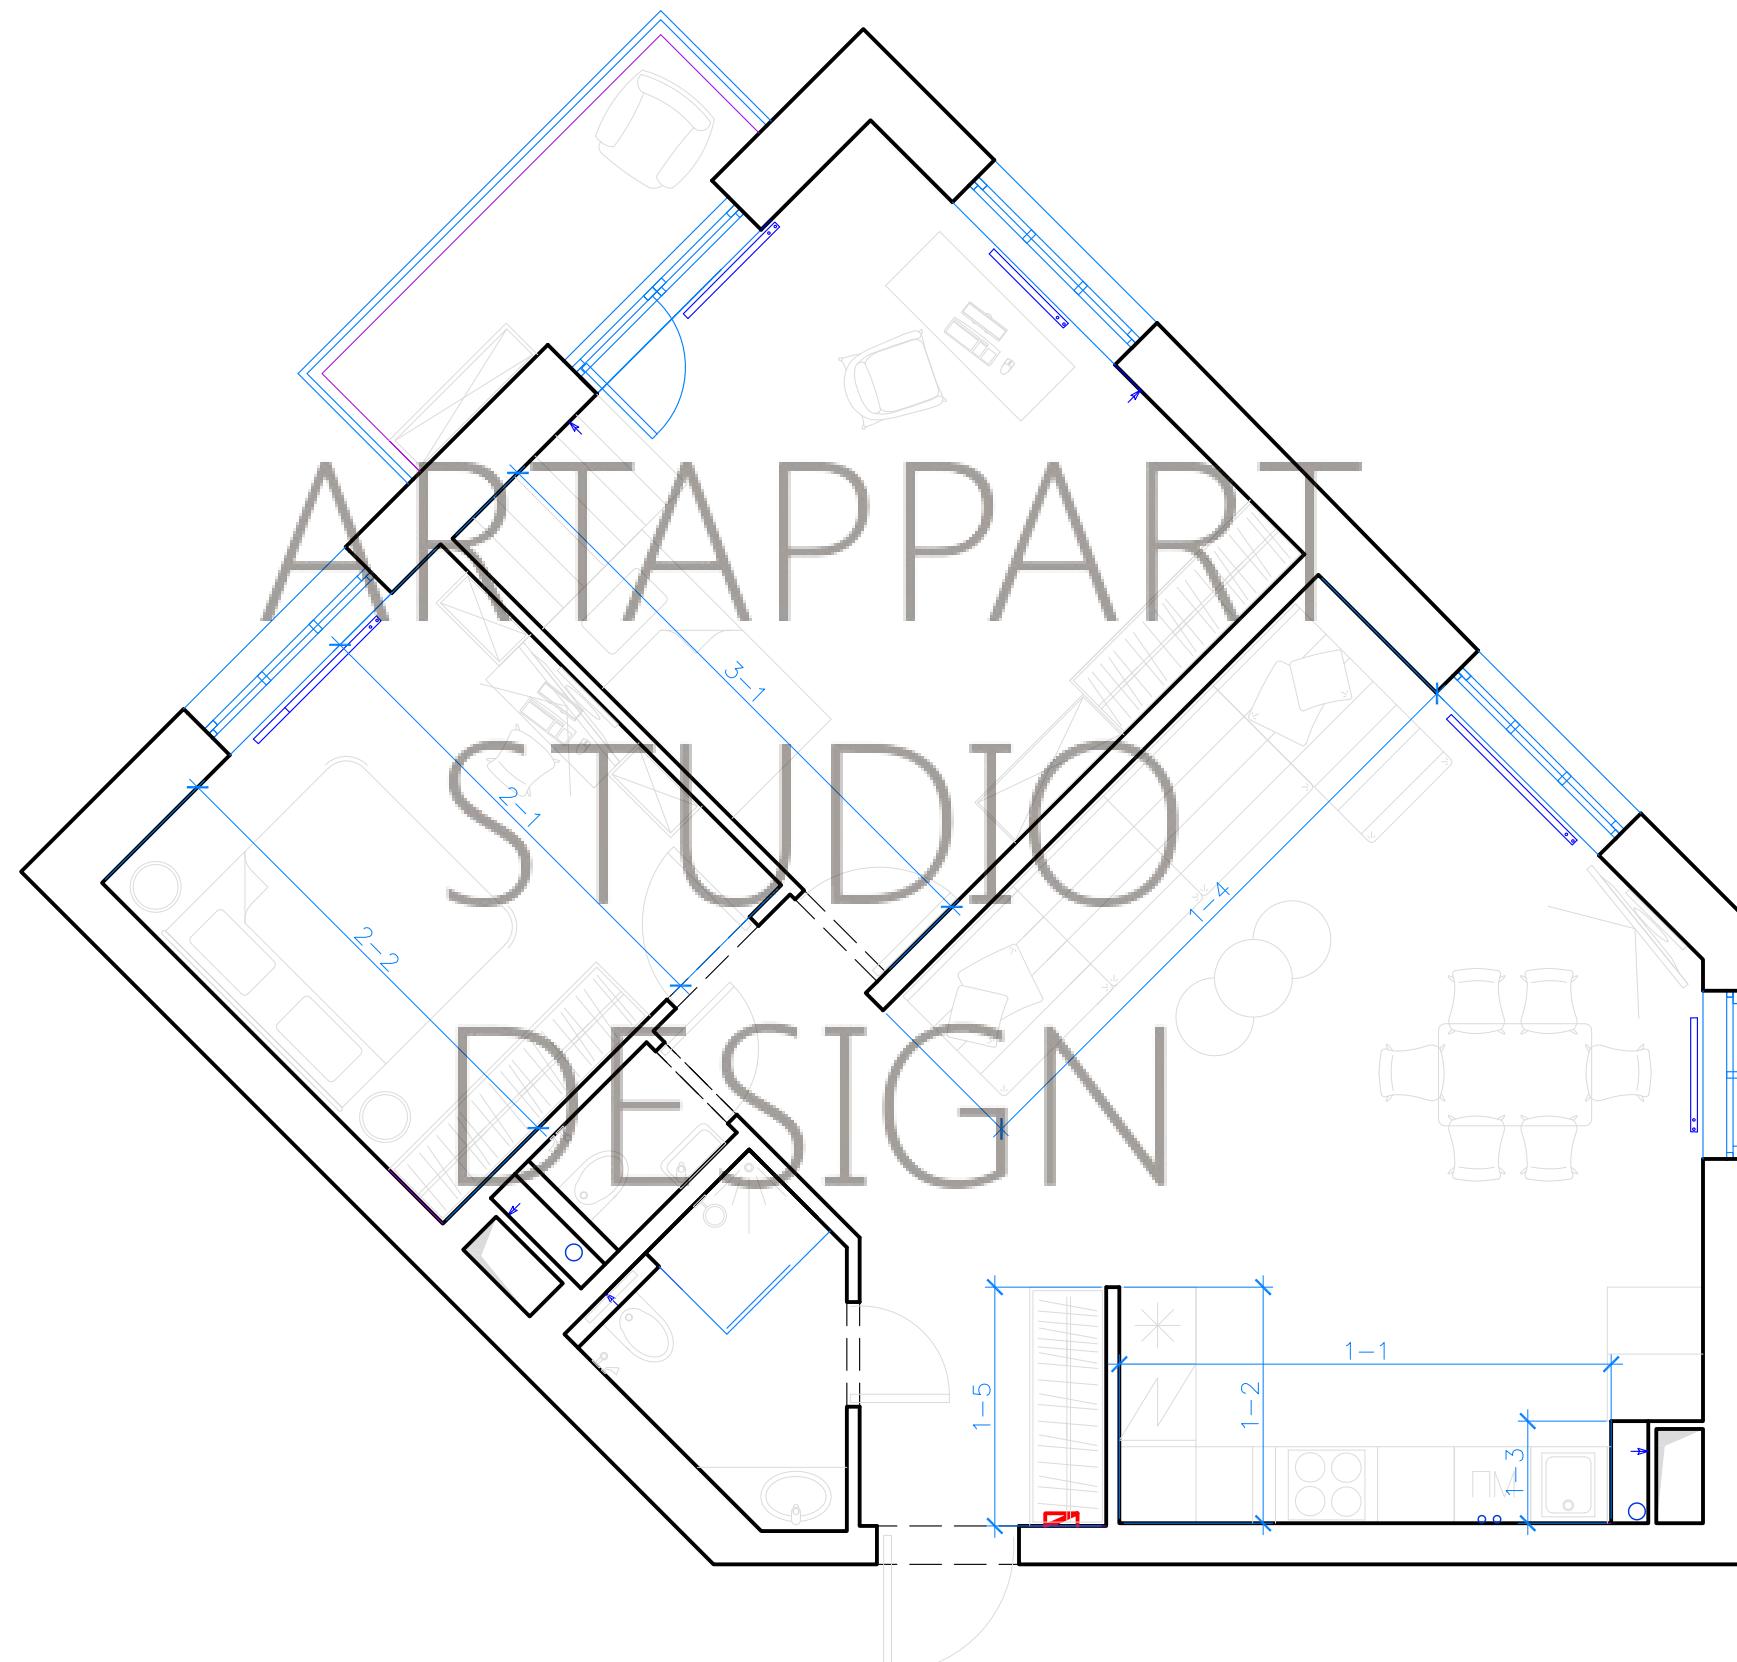

Лист	Листов	Масштаб
		M 1:60
Дизайнер	Заказчик	Схема обозначения разверток
		 ARTAPPART DESIGN STUDIO

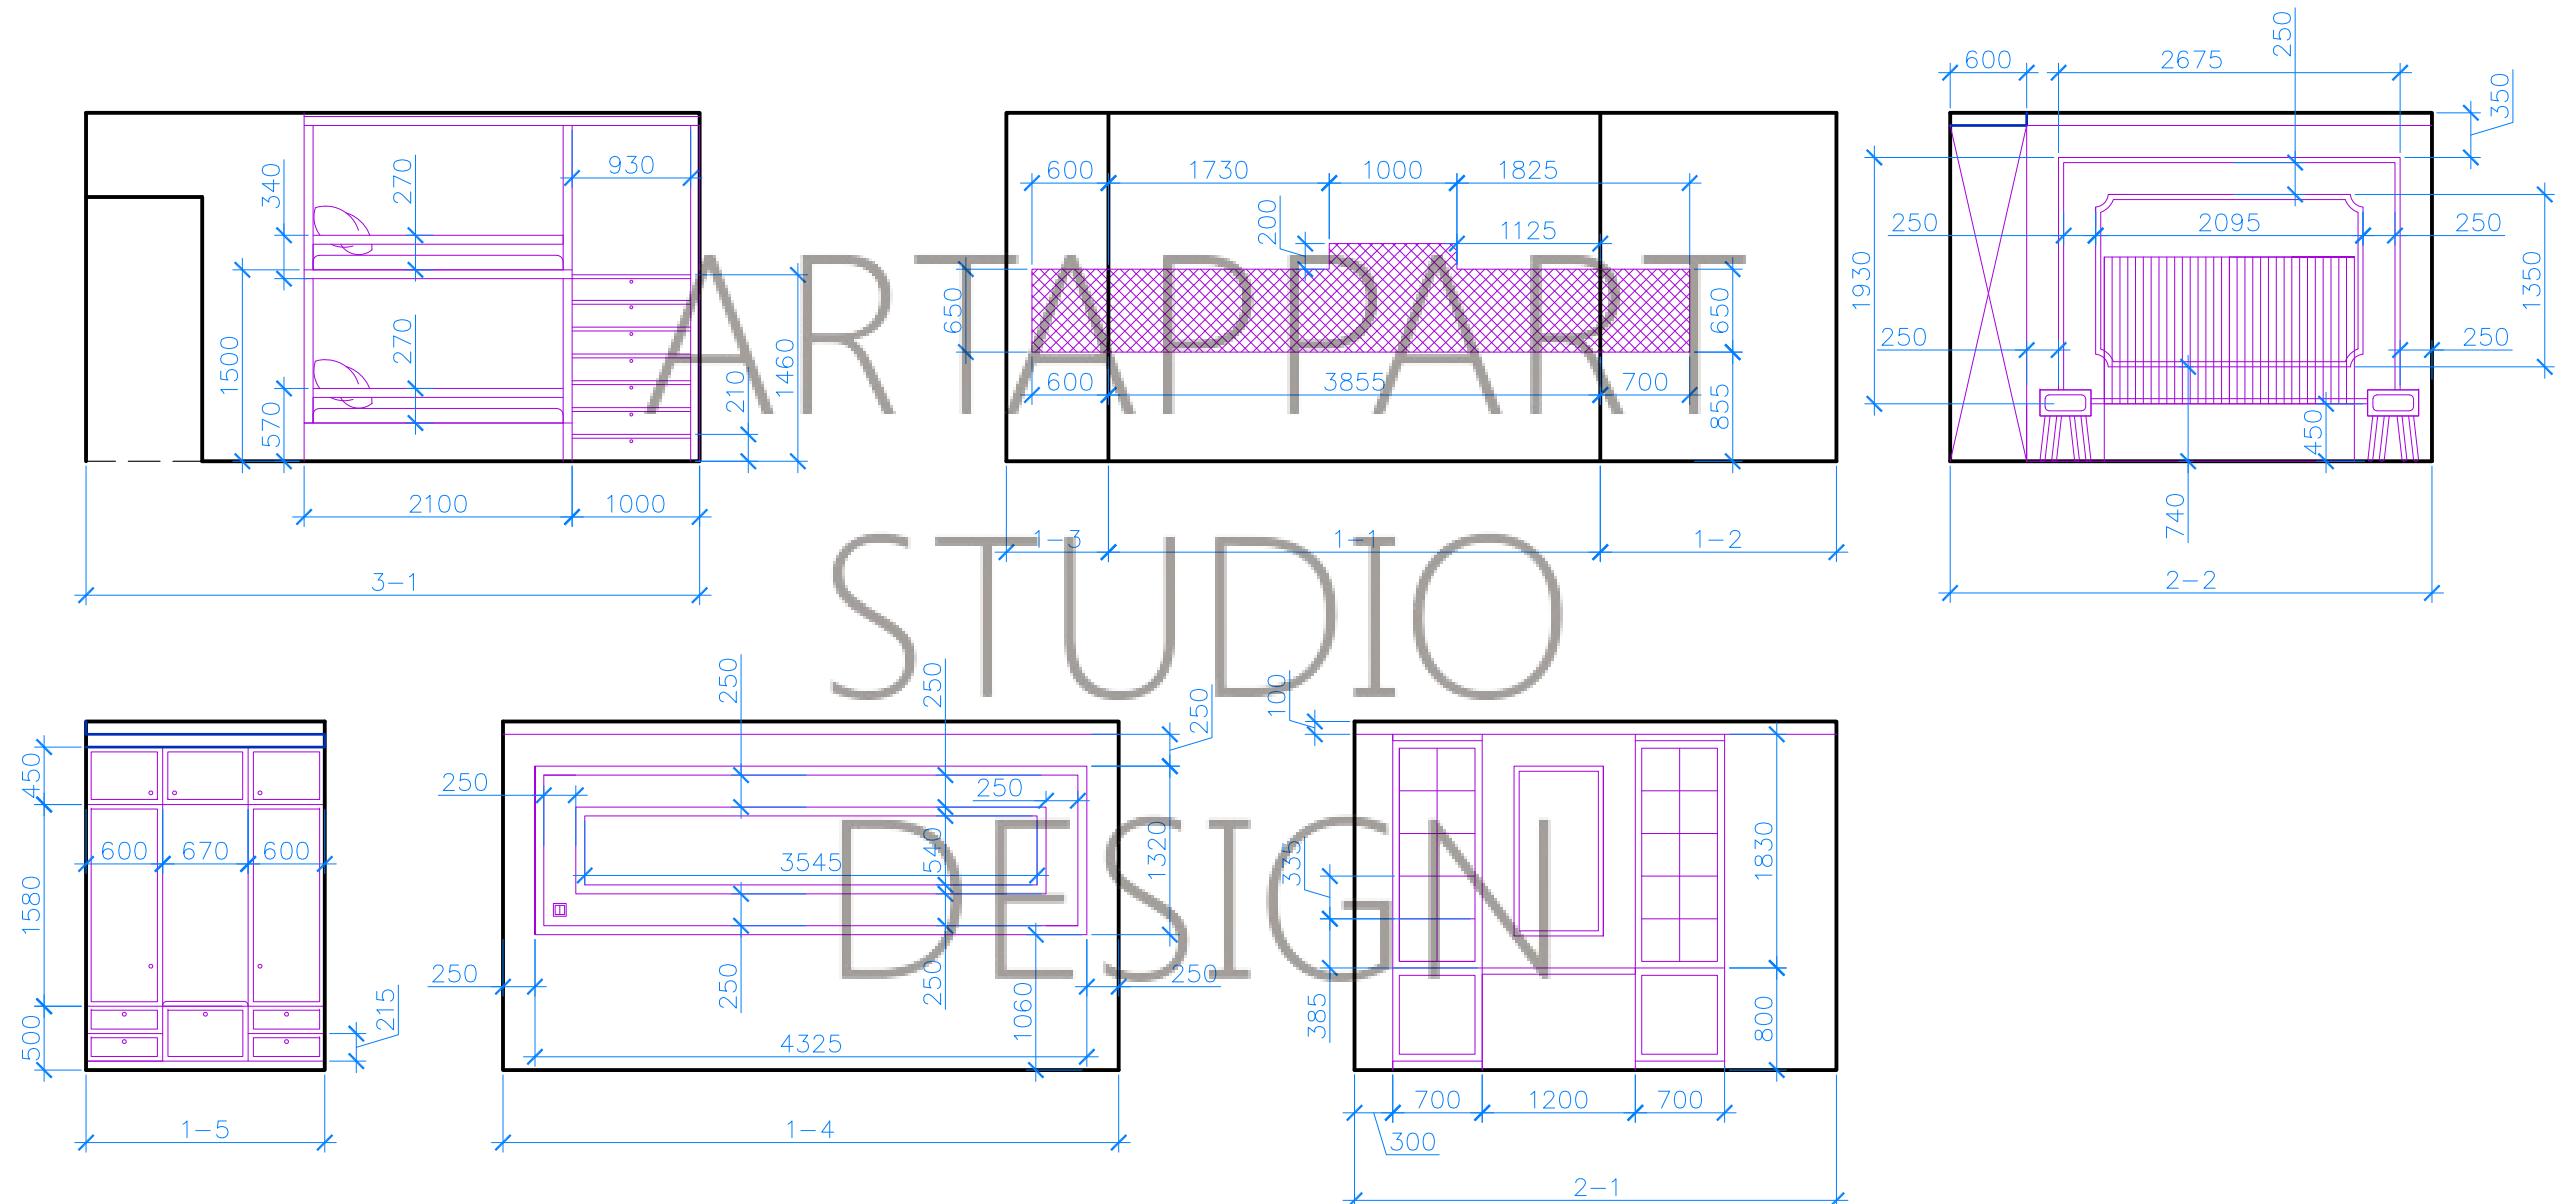

Лист	Листов	Масштаб
		M 1: 60
Дизайнер		
Заказчик		
Развертки по стенам		
		ARTAPPART DESIGN STUDIO

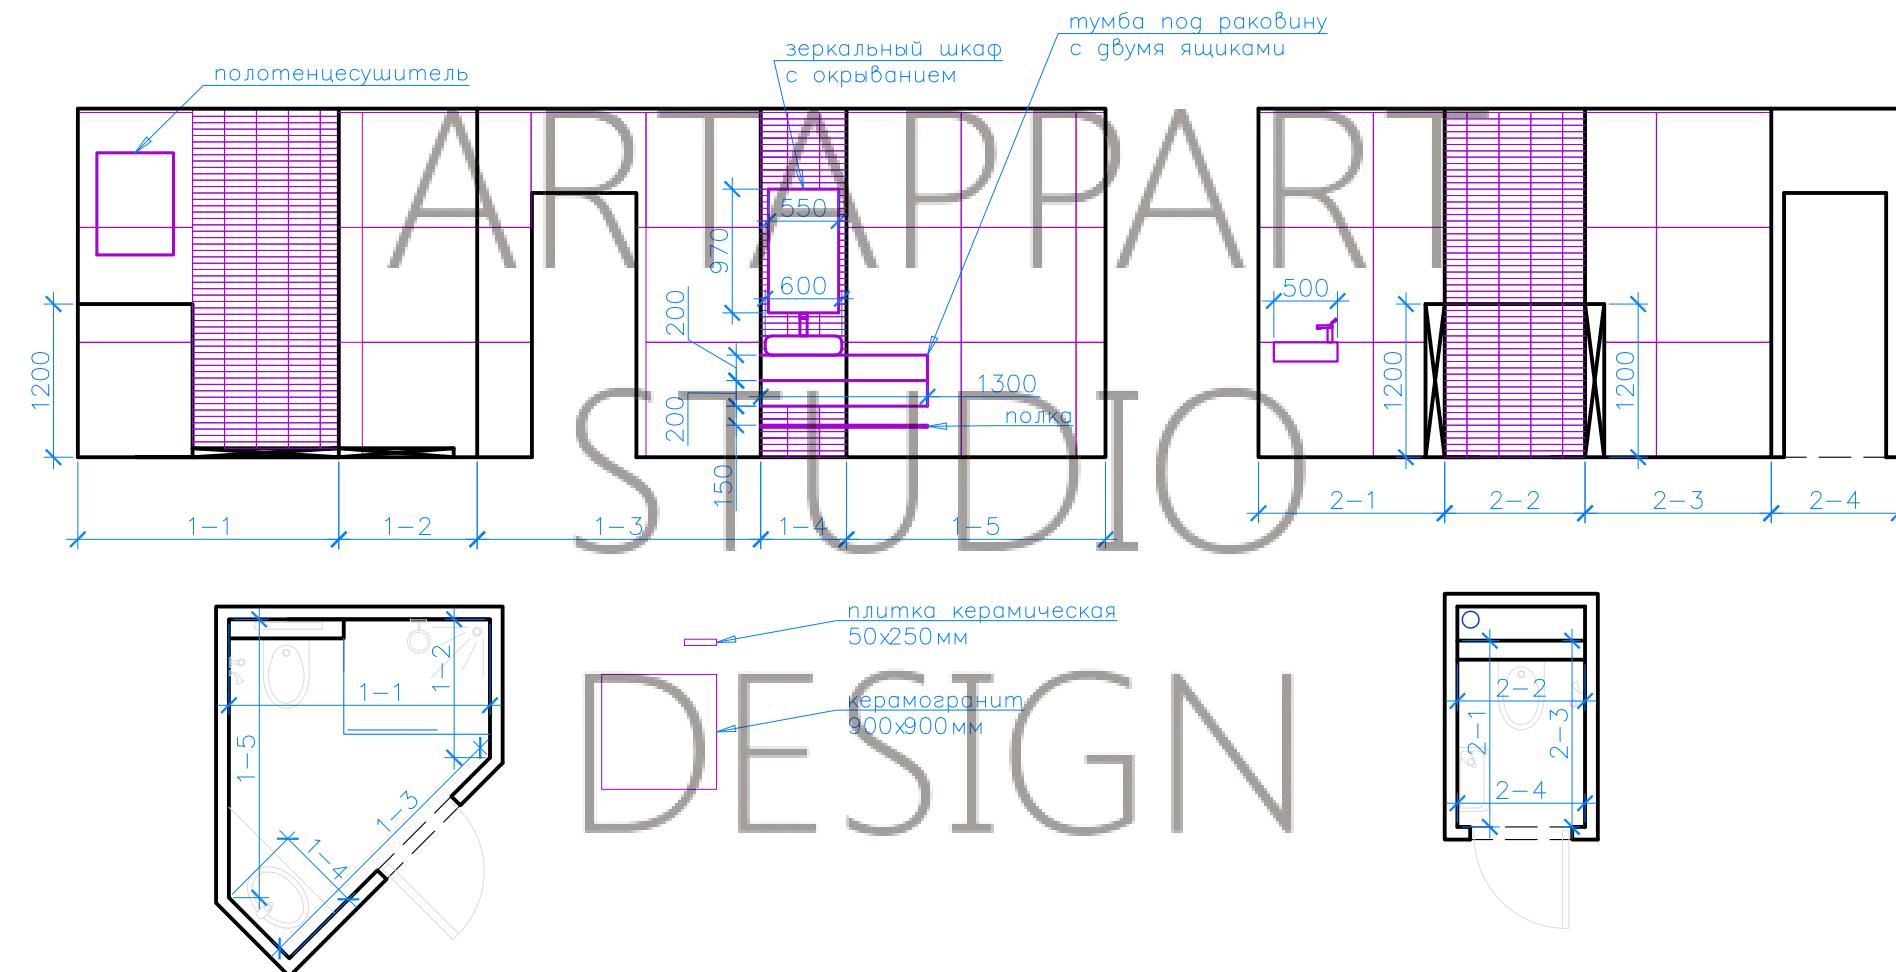

Лист	Листов	Масштаб
		M 1: 60
Дизайнер	Развертки по	
Заказчик	стенам санузлов	



ARTAPPART  
DESIGN  
STUDIO