



Дизайн проект "Эскизный"

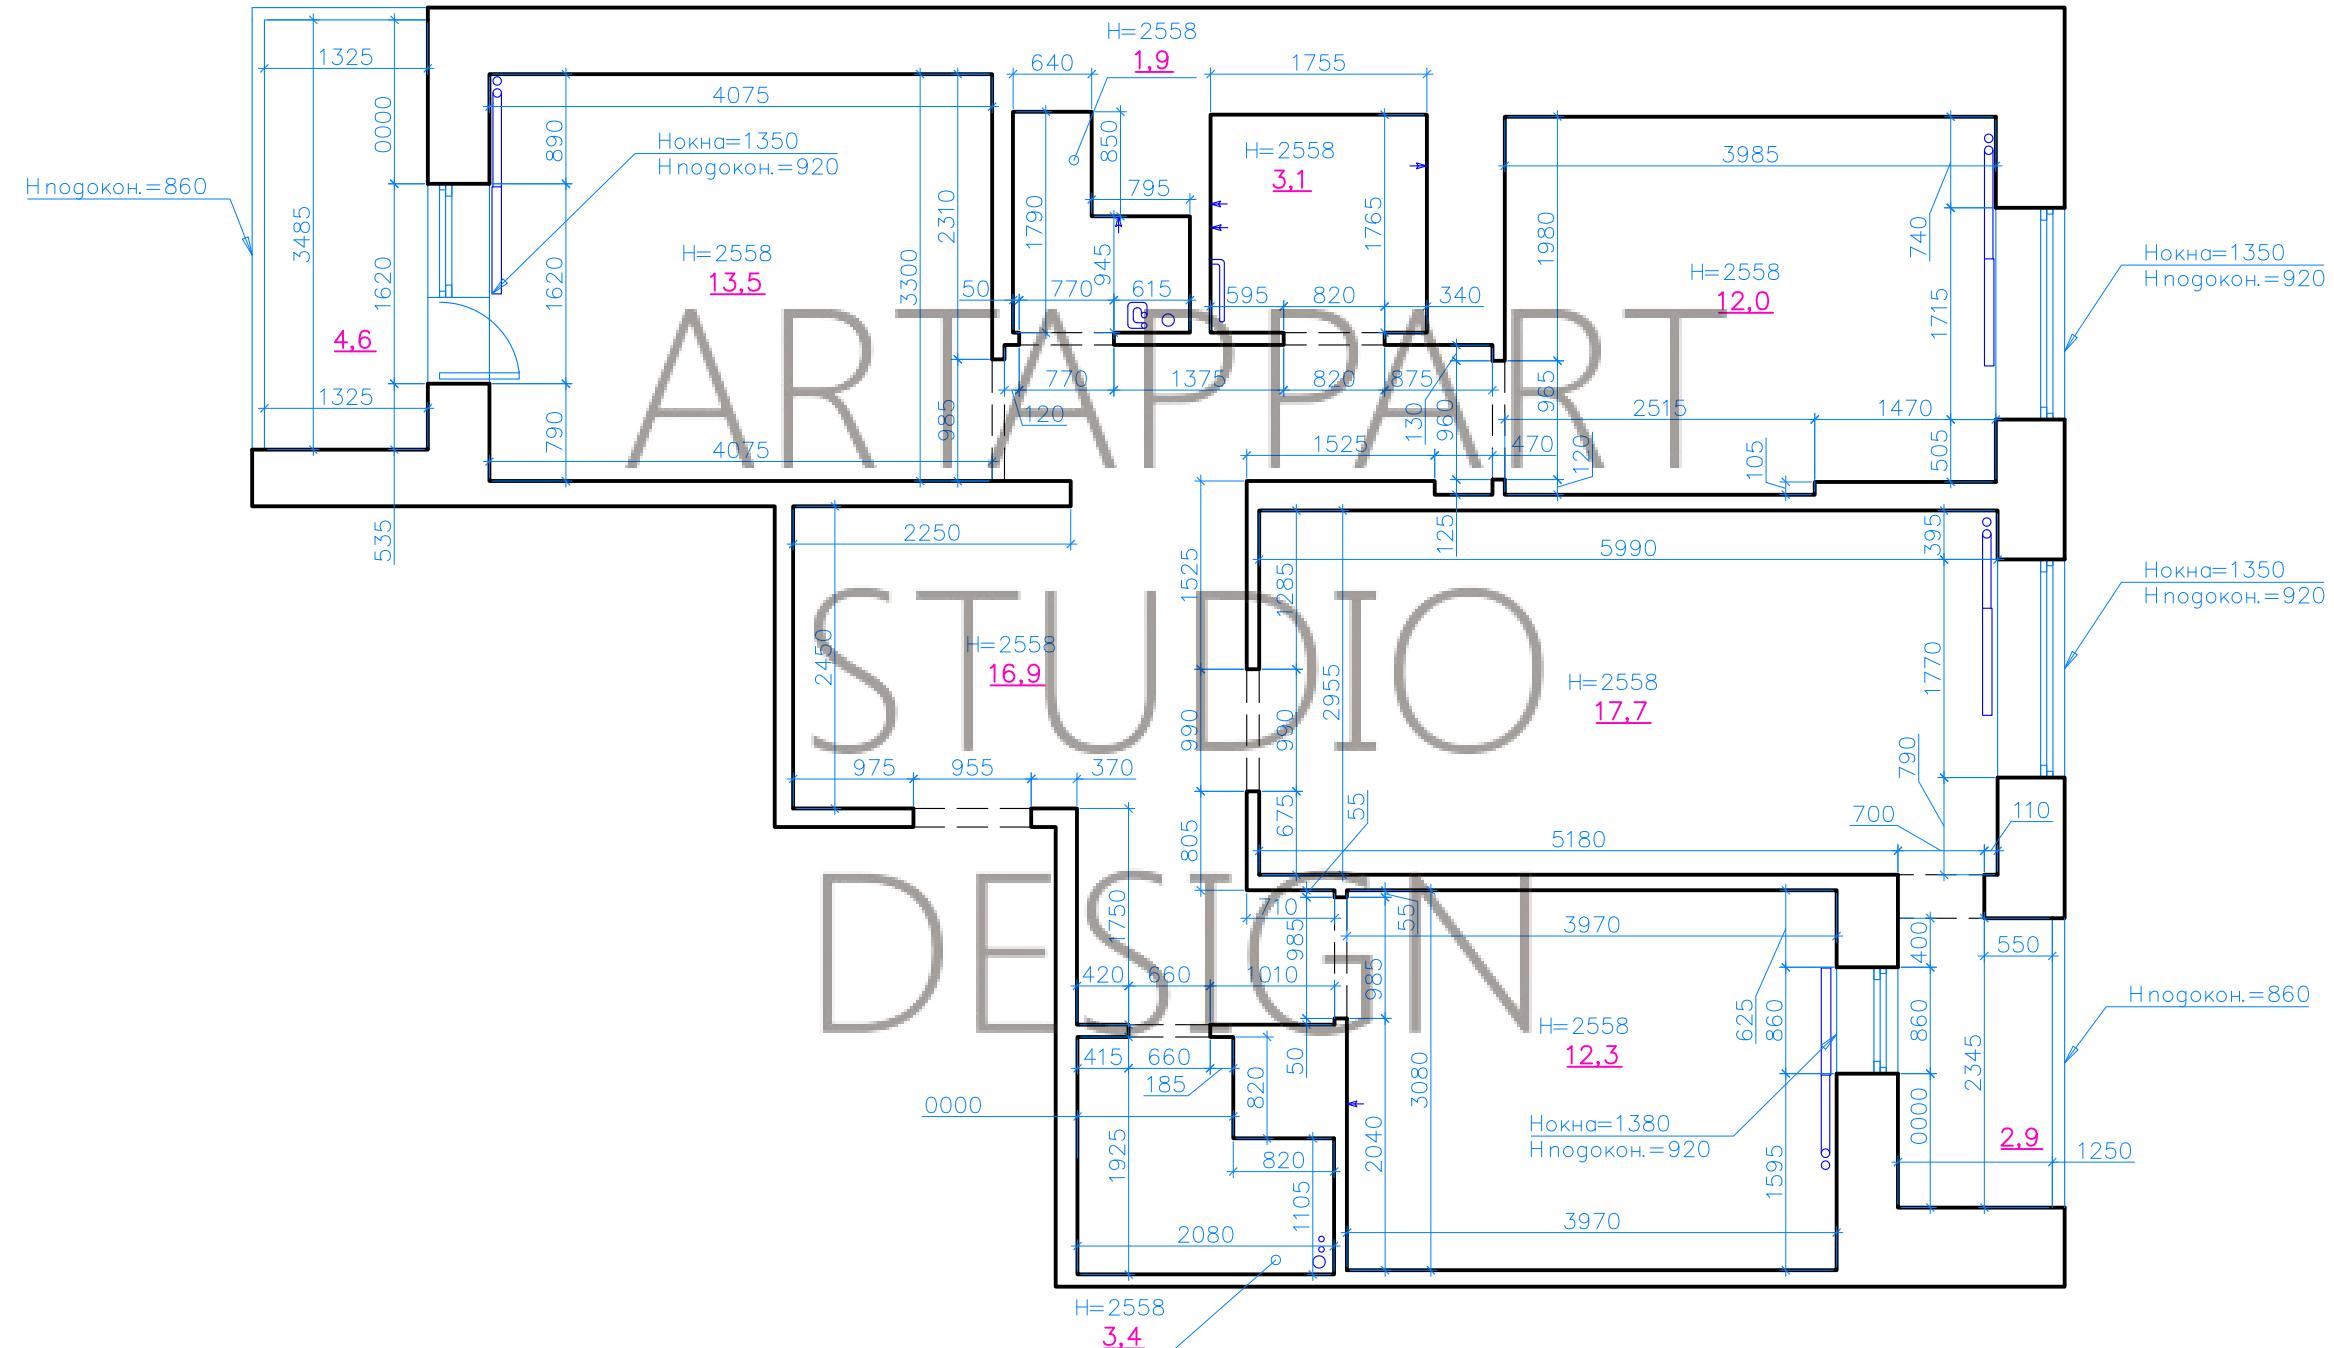


Собщ. помещений=88,3 м

Инв. № подл.	Подп. у чата	Взам. инв.
Согласовано		

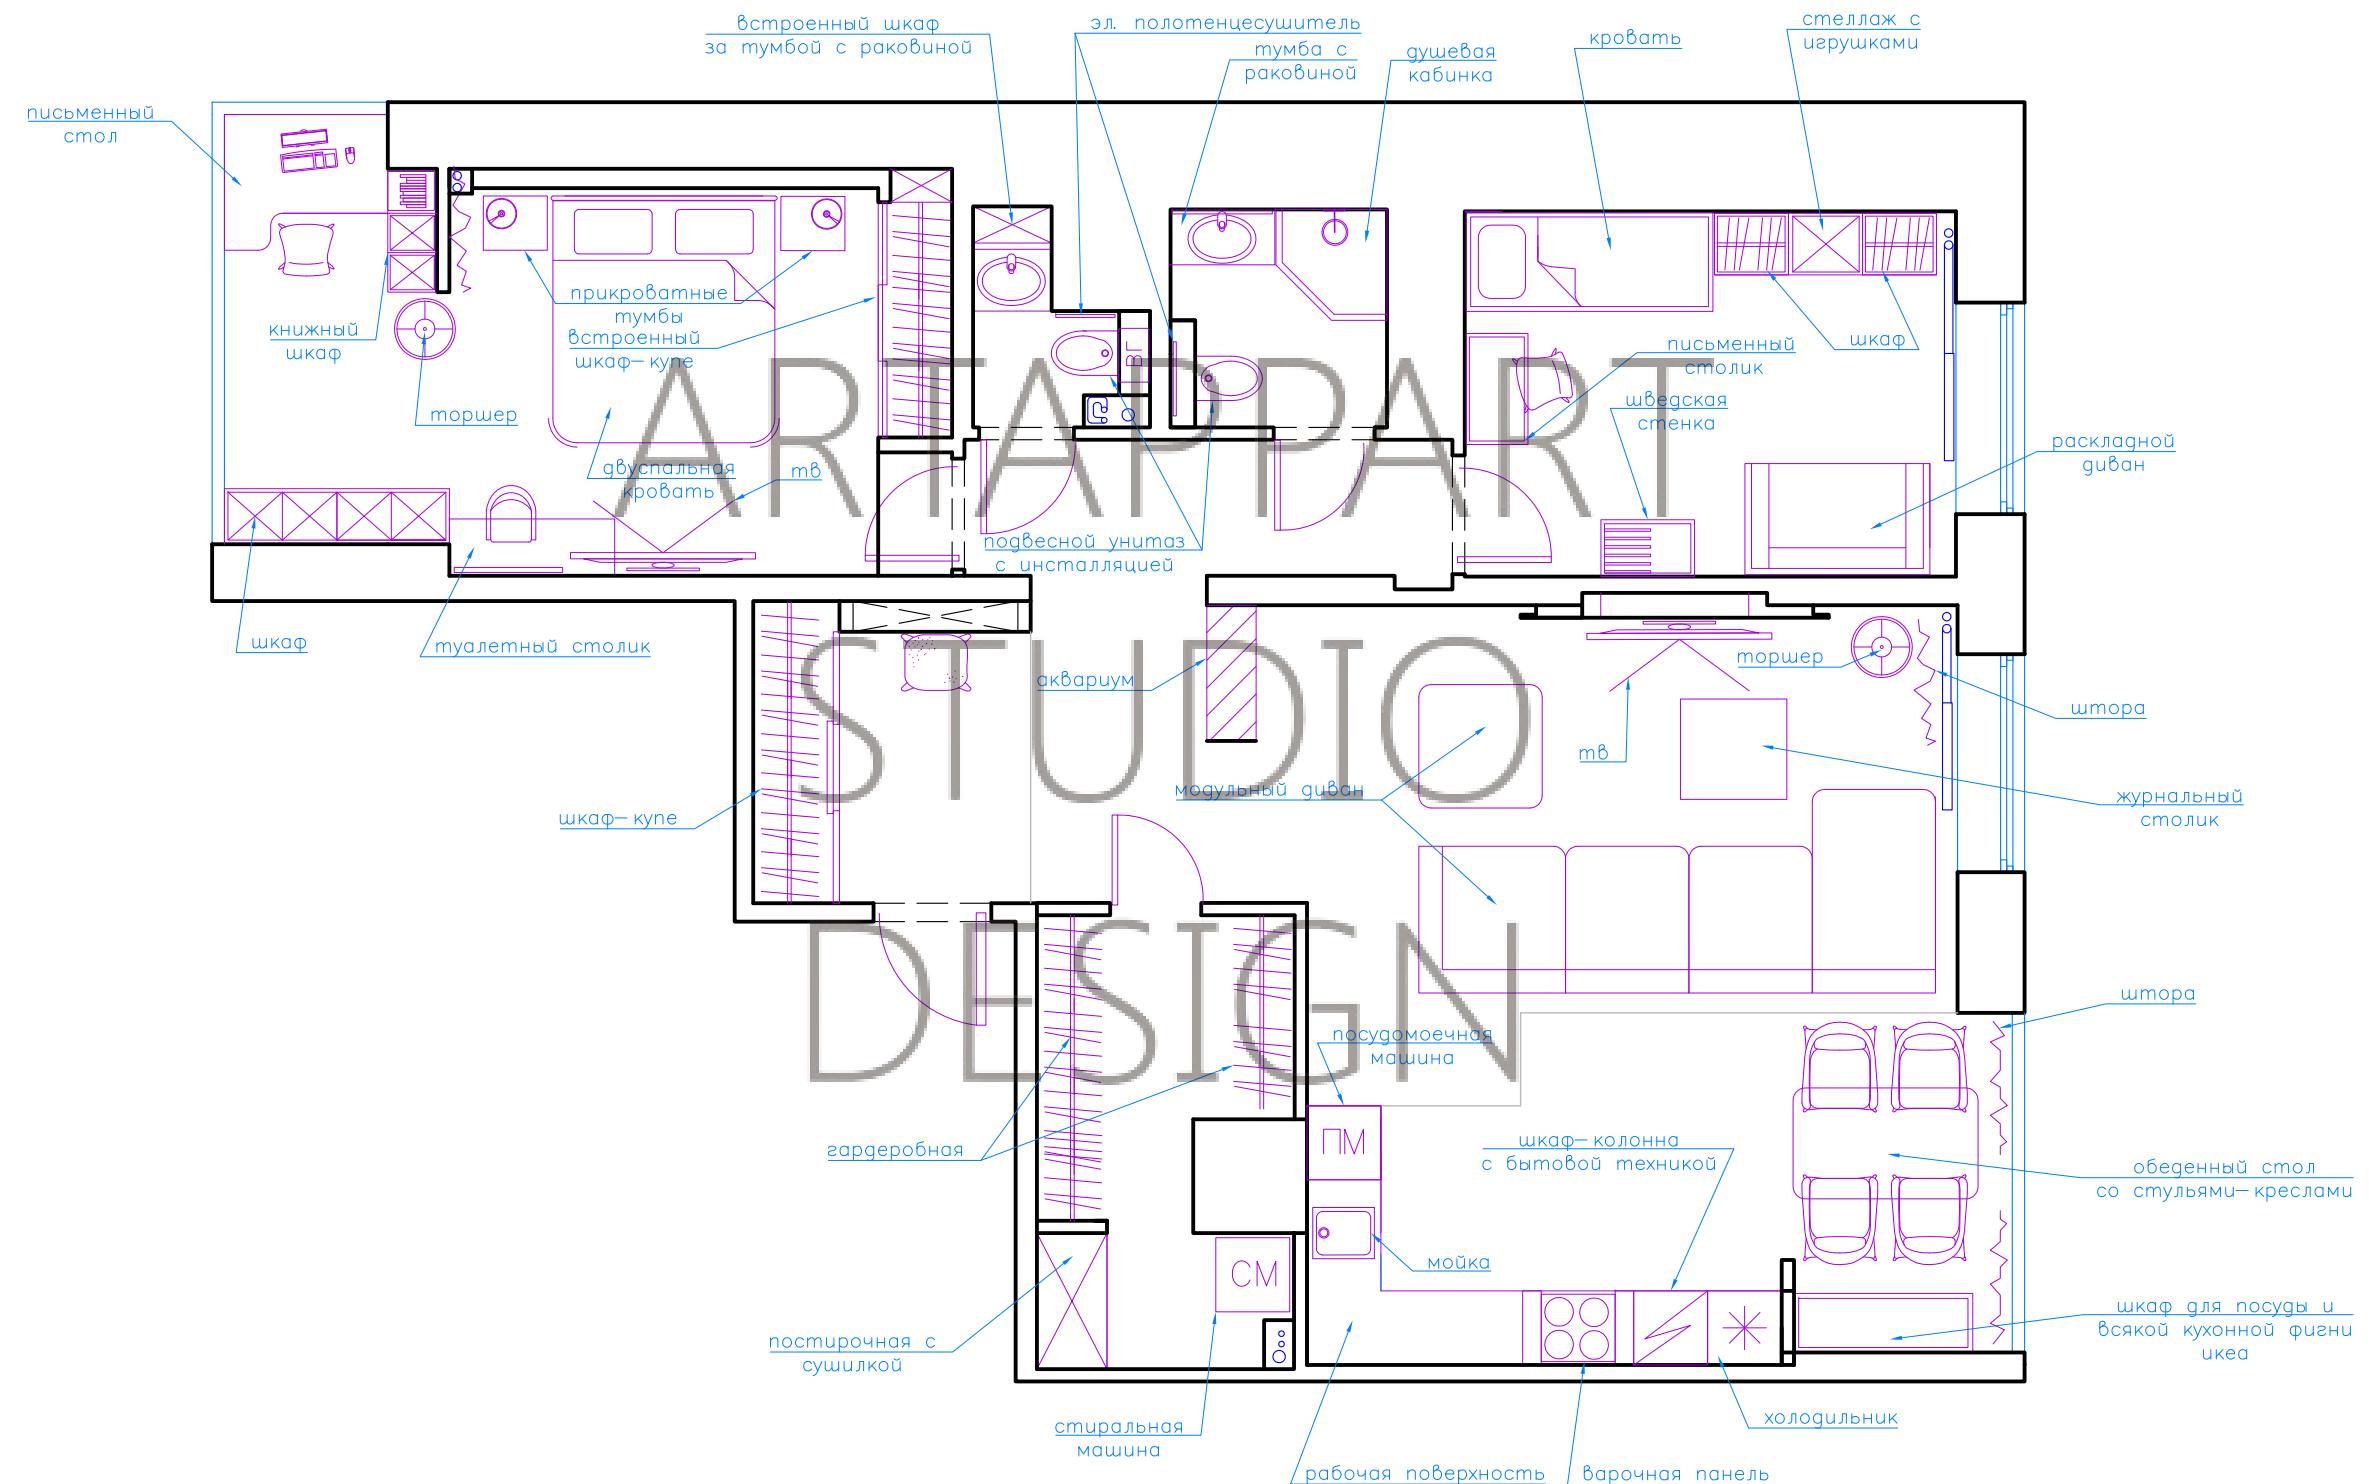

Изм.	Код уч.	Листм	№ док.	Подп.	Дата	Разработка дизайн-проекта квартиры	Стадия	Листм	Листовъ
Заказчик					2017				
Разработ.					2017		P		
						План расположения мебели и оборудования			
						М 1: 60			

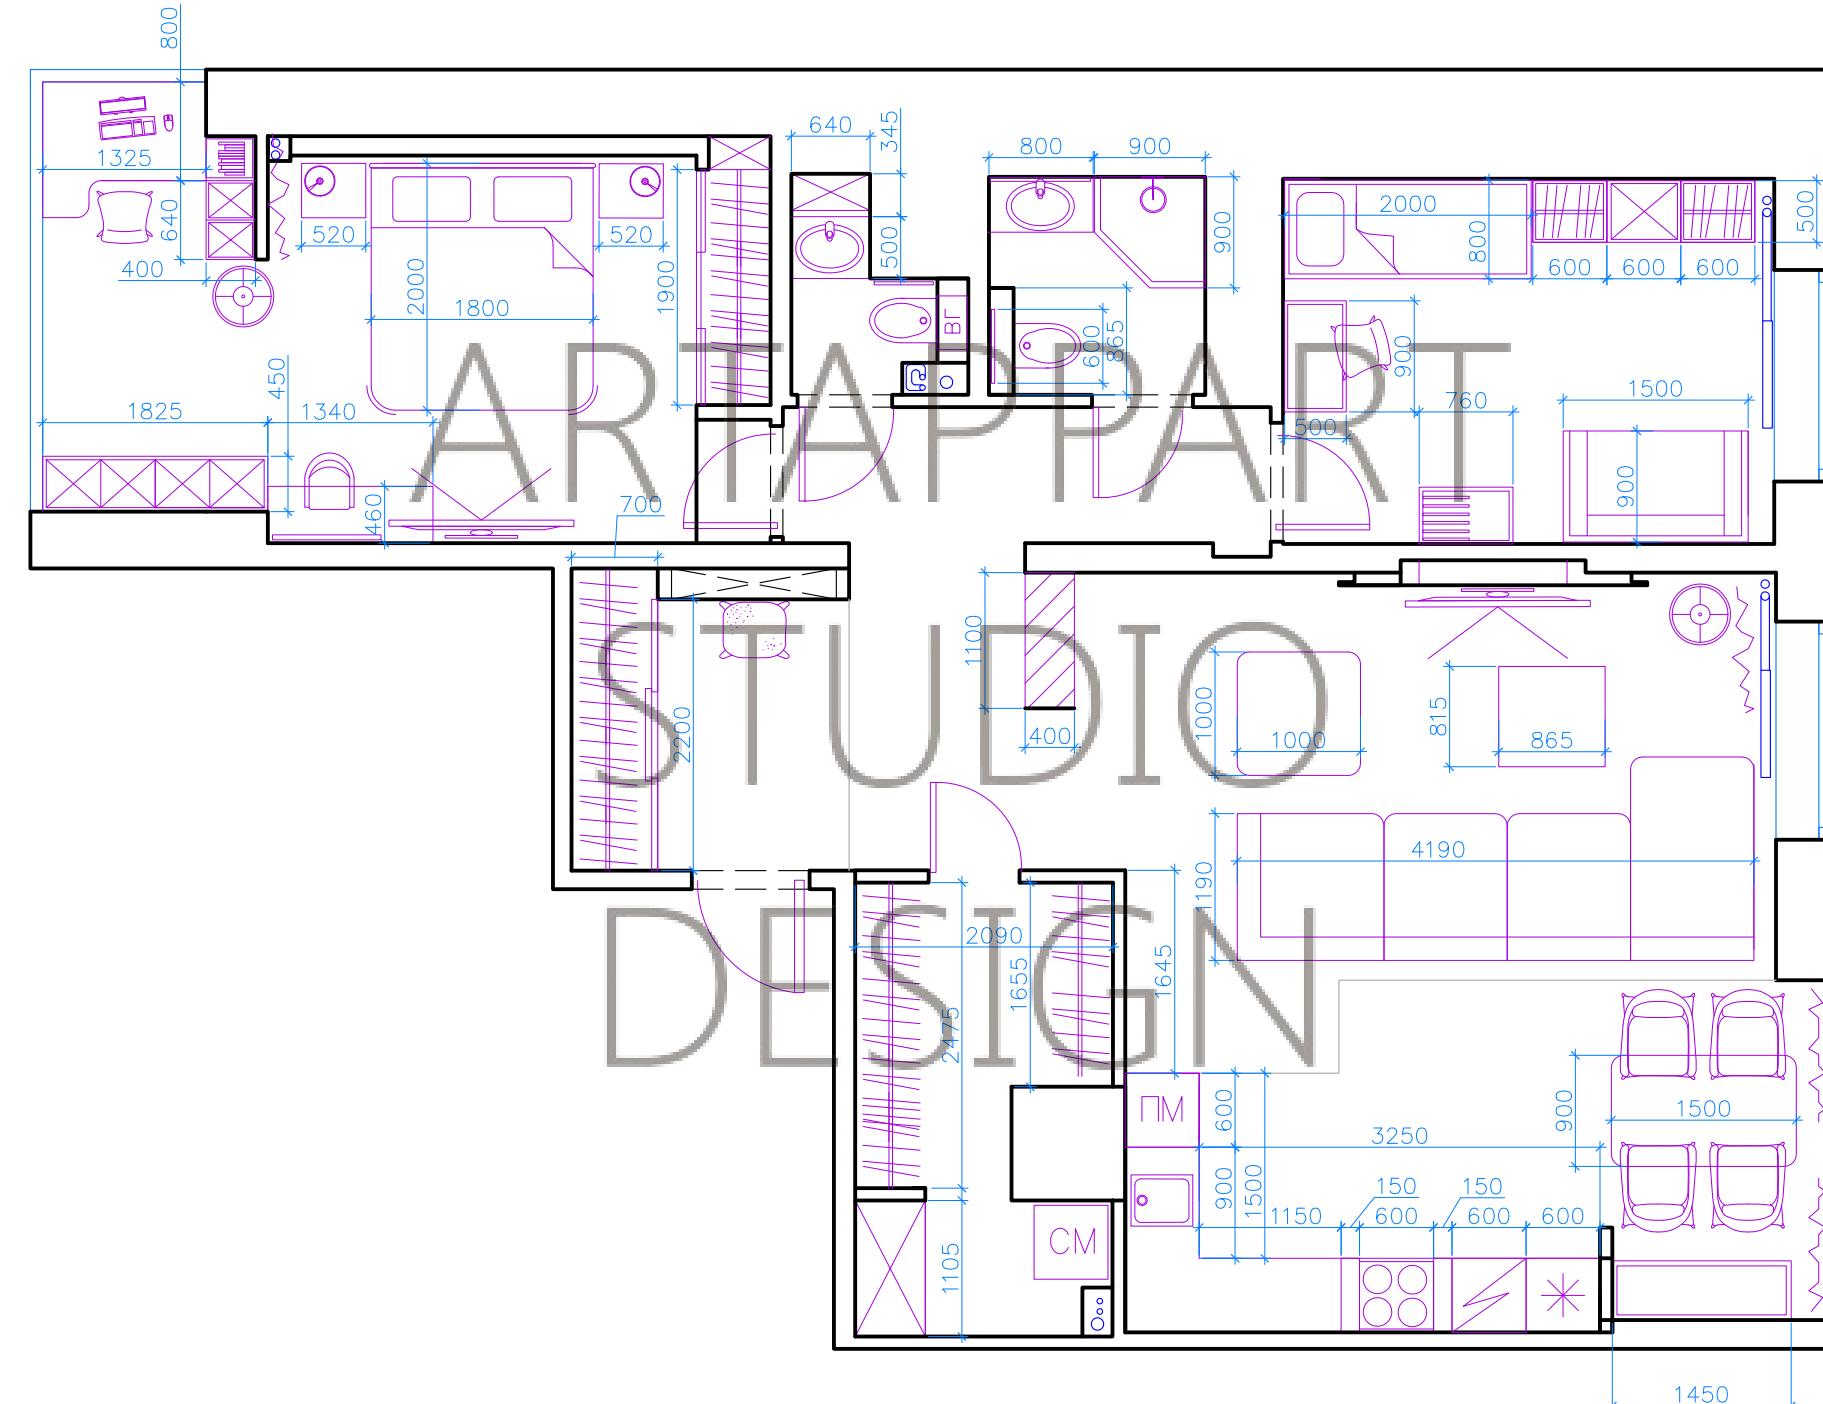

Согласовано

Инв. № подп.


Подп. и дата

Взам. инв.

Изм.	Кол. уч.	Листм	№ док.	Подп.	Дата	Разработка дизайн-проекта квартиры	Стадия	Листм	Листов
Заказчик					2017				
Разработ.					2017	Схема расстановки мебели с указанием основных размеров	P		
						M 1:60			



ARTAPPART
DESIGN
STUDIO

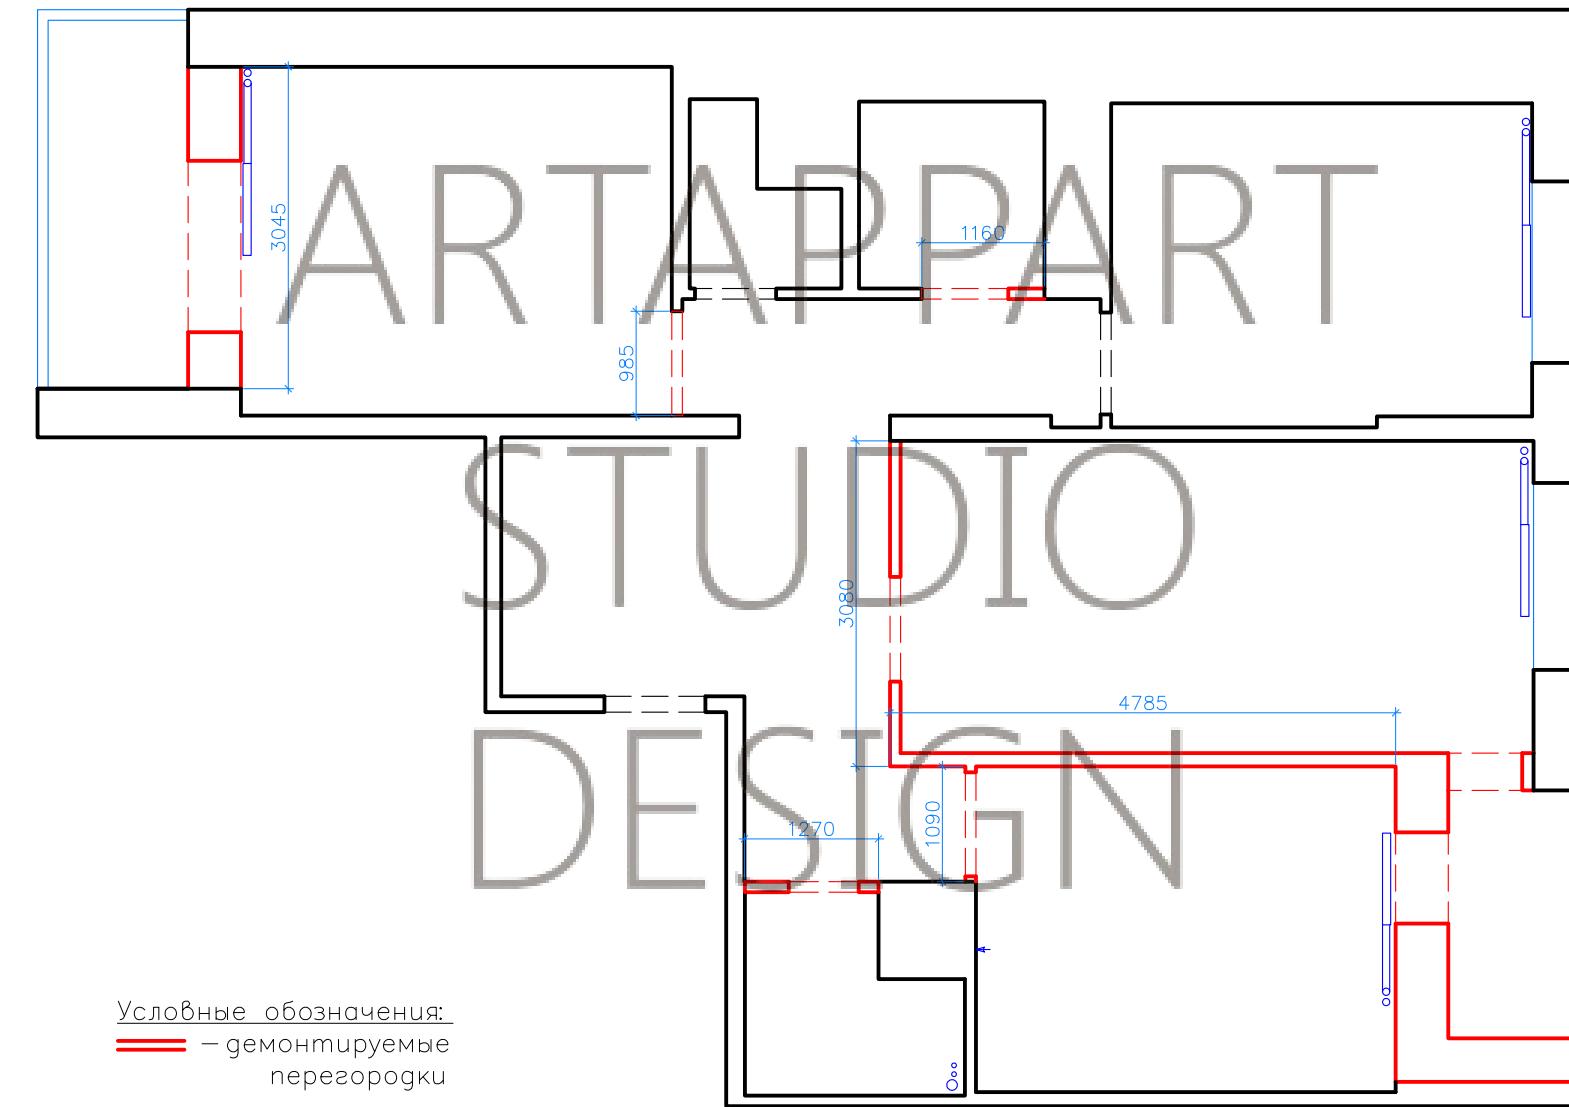

Инв. № подп.	Подп. и дата	Взам. инв.


Изм.	Кол. уч.	Листм	№ док.	Подп.	Дата	Разработка дизайн-проекта квартиры	Стадия	Листм	Листов
Заказчик					2017		P		
Разработ.					2017	План демонтируемых перегородок			
						М 1:60			



ARTAPPART
DESIGN
STUDIO

Инв № подп	Подп и дата	Взам. инв

Согласовано

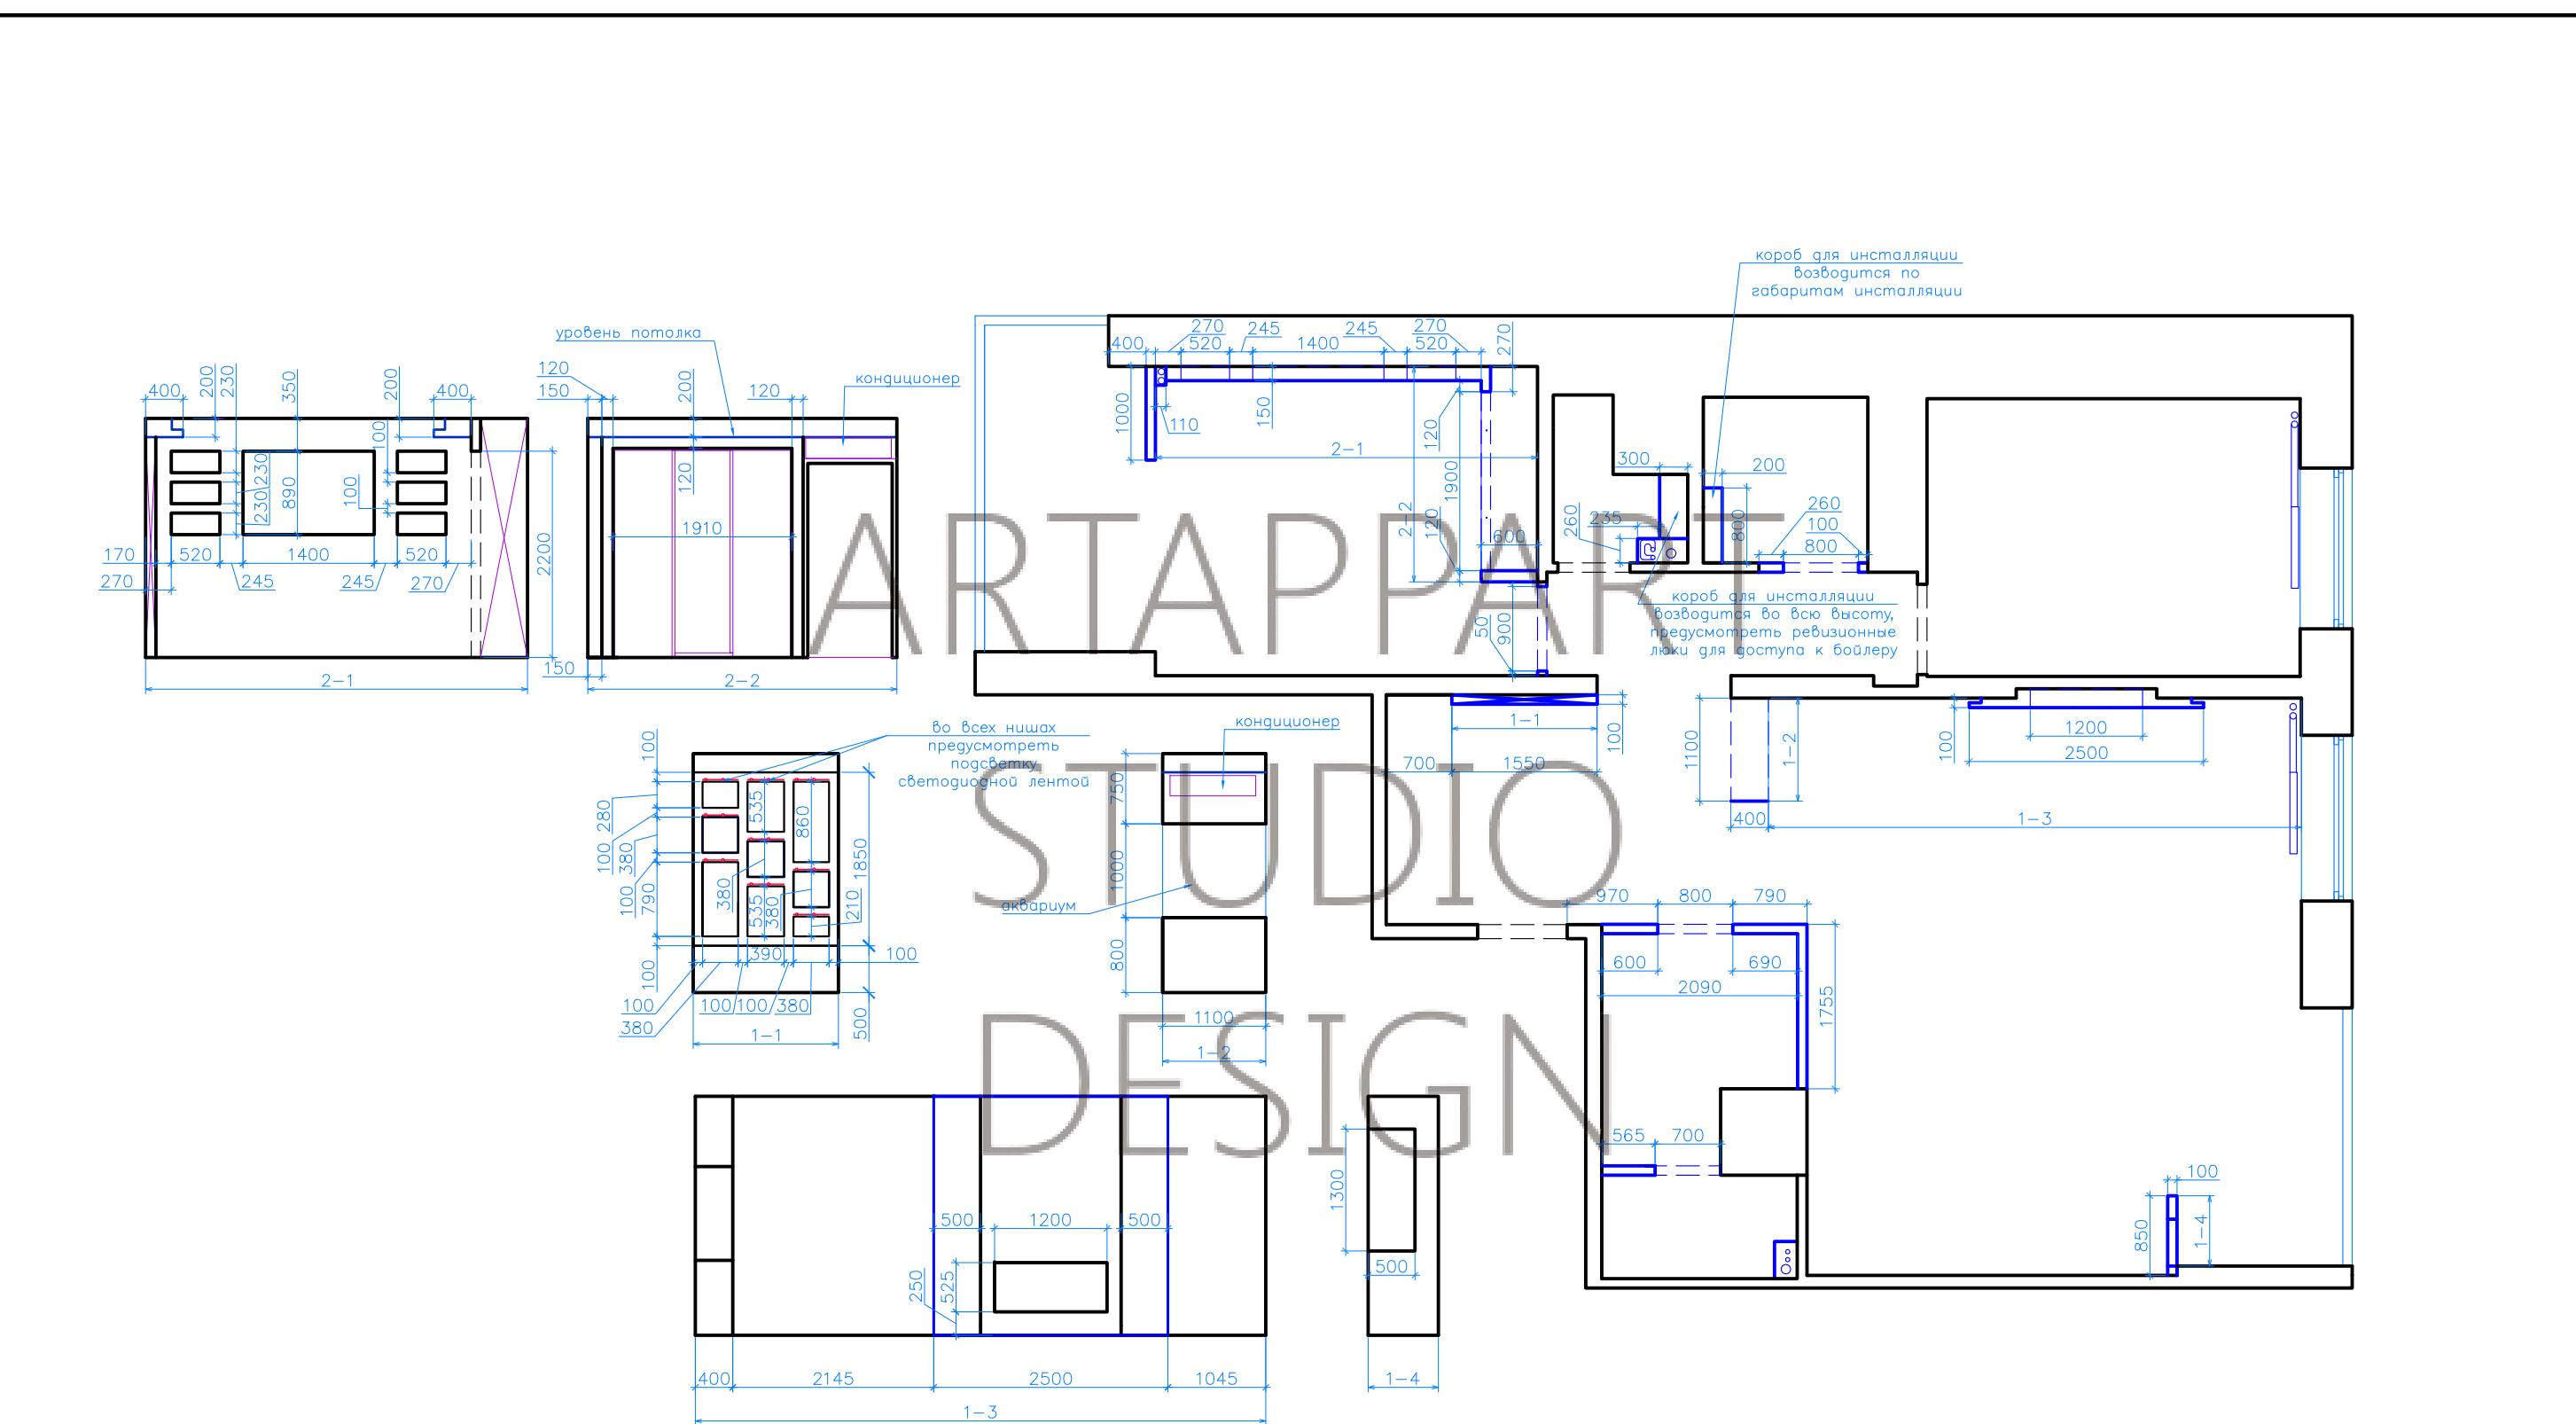

Условные обозначения:

— возводимые перегородки


Примечание:

1. Все существующие проемы выровнять по высоте до отметки 2070 от УЧП (за уровень чистового пола принимается пол после стяжки и укладки напольного покрытия)
2. Предусмотреть установку фильтров водоснабжения и ревизионных люков.
3. Предусмотреть устройство вентиляции в санузлах
4. Разводка коммуникаций для систем кондиционирования выполняется предварительно, по проекту систем кондиционирования.

Изм.	Кол. уч	Лист	№ док	Подп.	Дата	Разработка дизайн-проекта квартиры	Стадия	Лист	Листов
Заказчик					2017				
Разработ.					2017	План возводимых перегородок и коробов ГКЛ	P		
						М 1: 70			



ARTAPPART
DESIGN
STUDIO

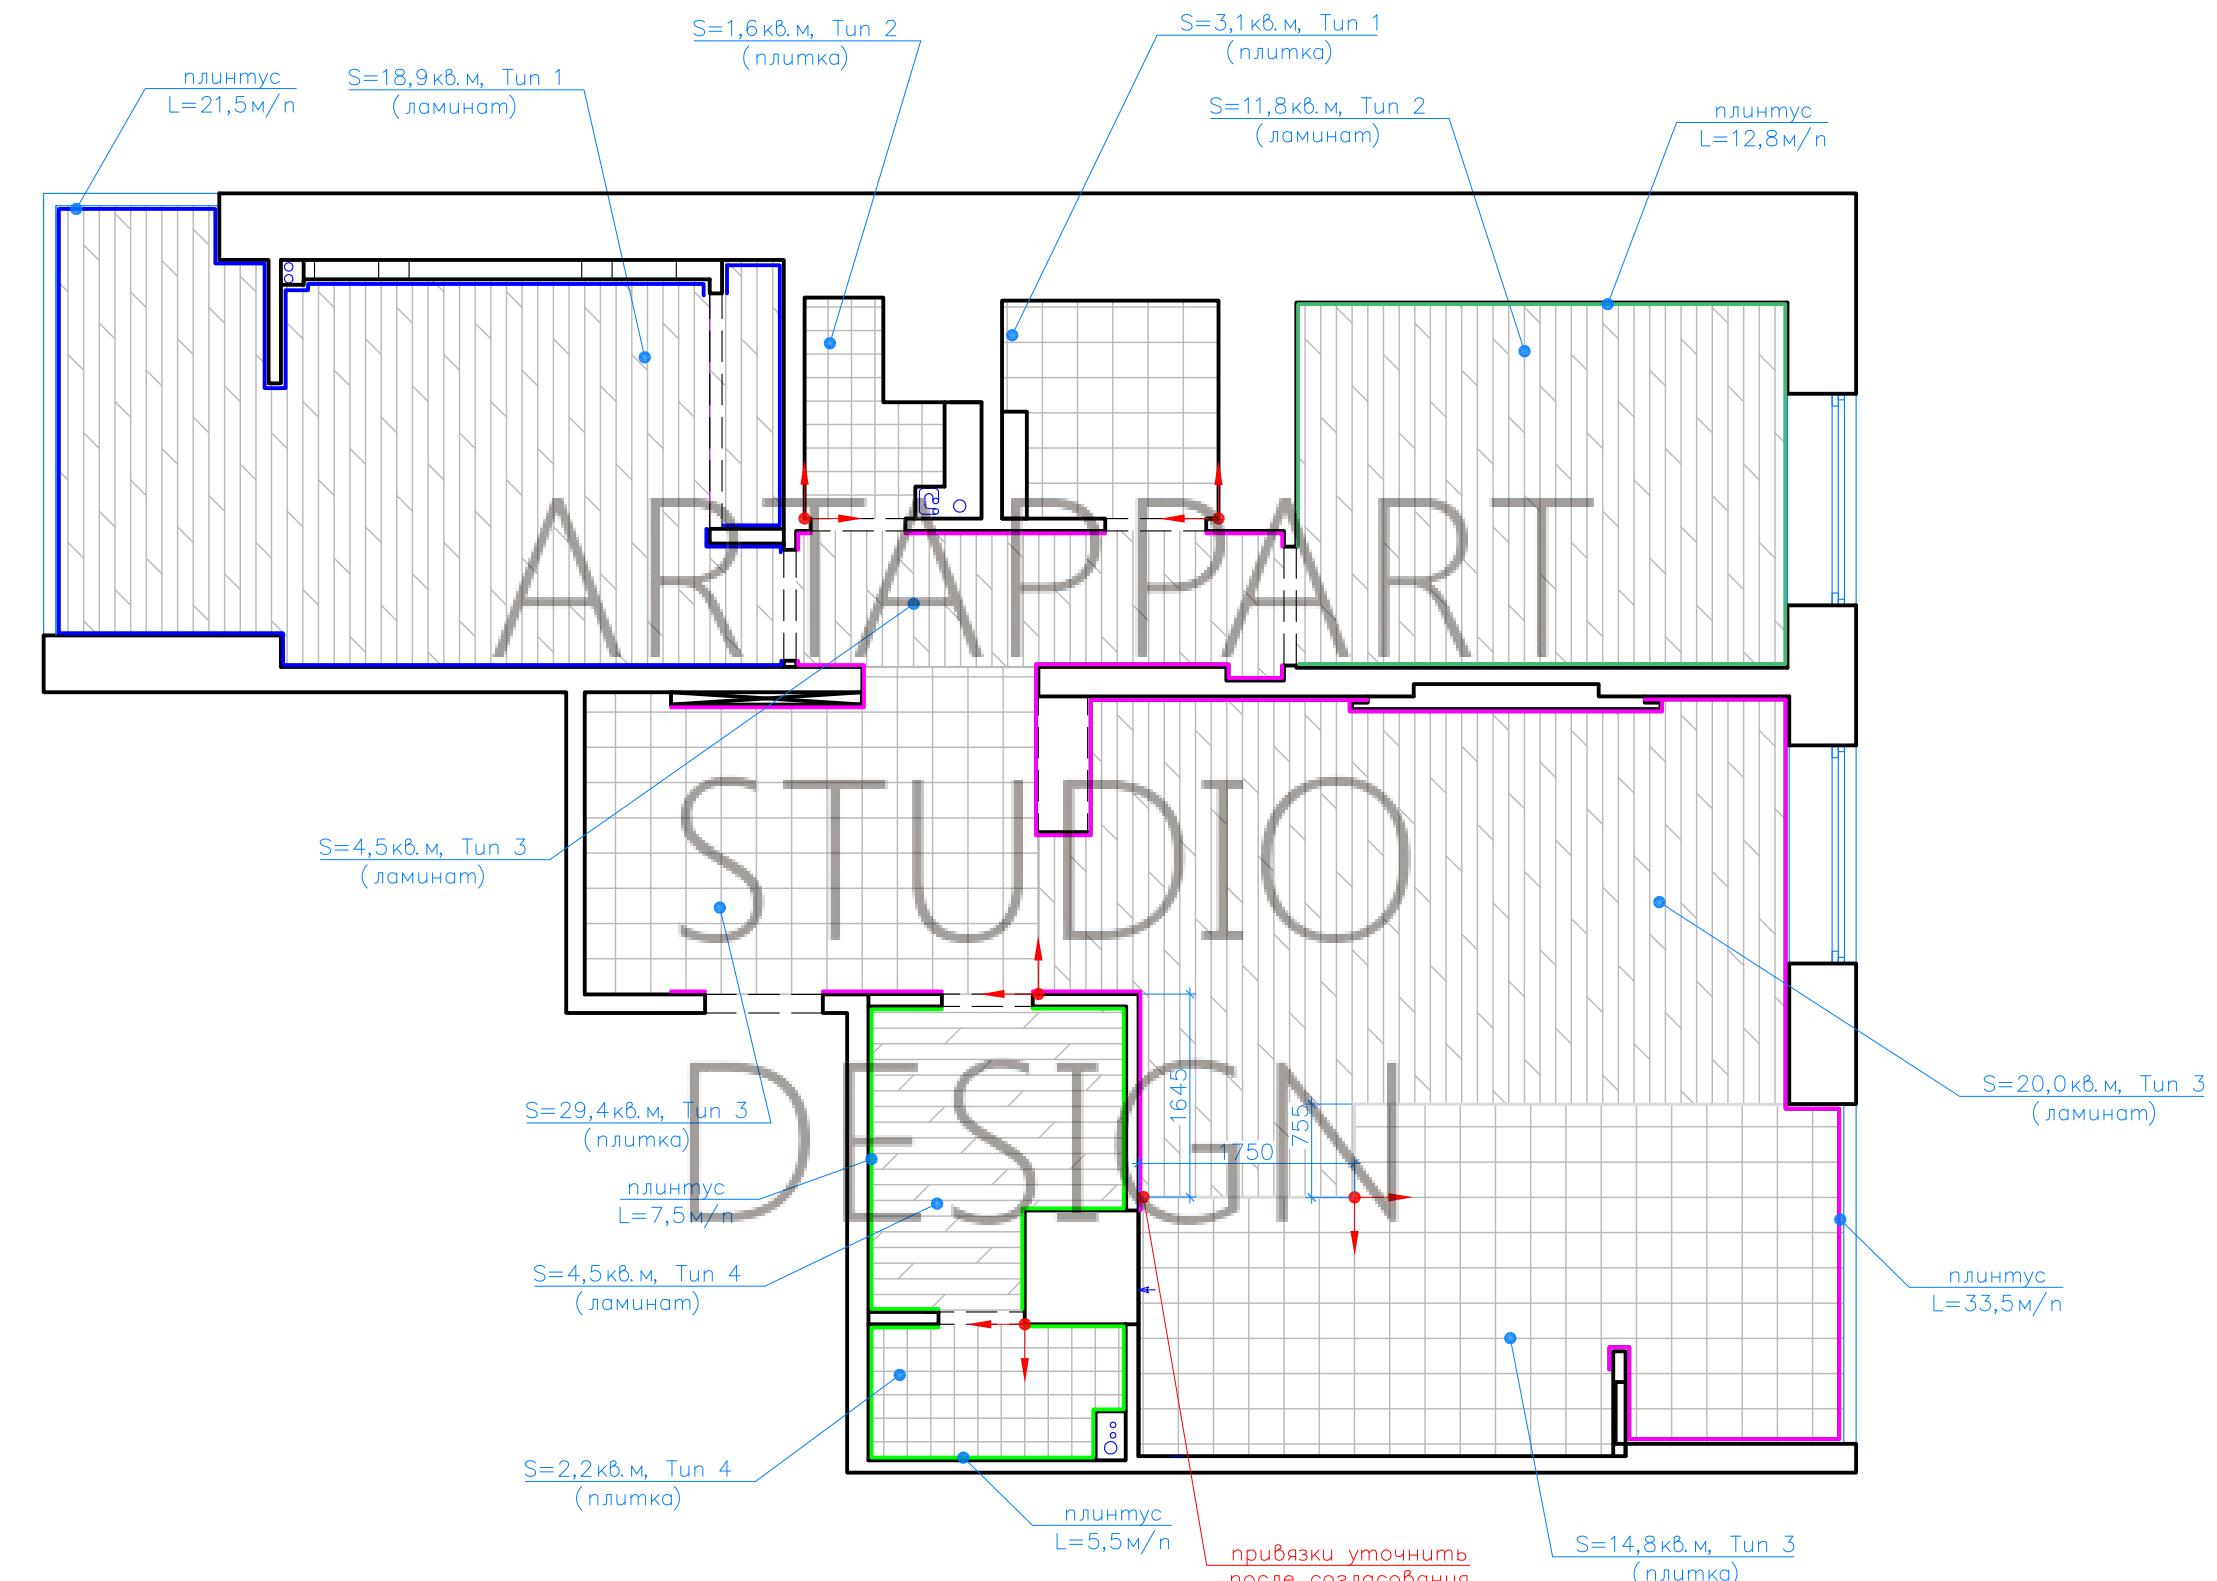

Инв № подп	Подп	Идент. подп	Взам. инв
------------	------	-------------	-----------


Примечание:

Площади покрытий даны без учета запаса.

Изм.	Кол. уч	Листм	№ док	Подп.	Дата	Разработка дизайн-проекта квартиры	Стадия	Листм	Листмов
Заказчик					2017				
Разработ.					2017				

План полов и напольных покрытий
М 1:60

ARTAPPART DESIGN STUDIO

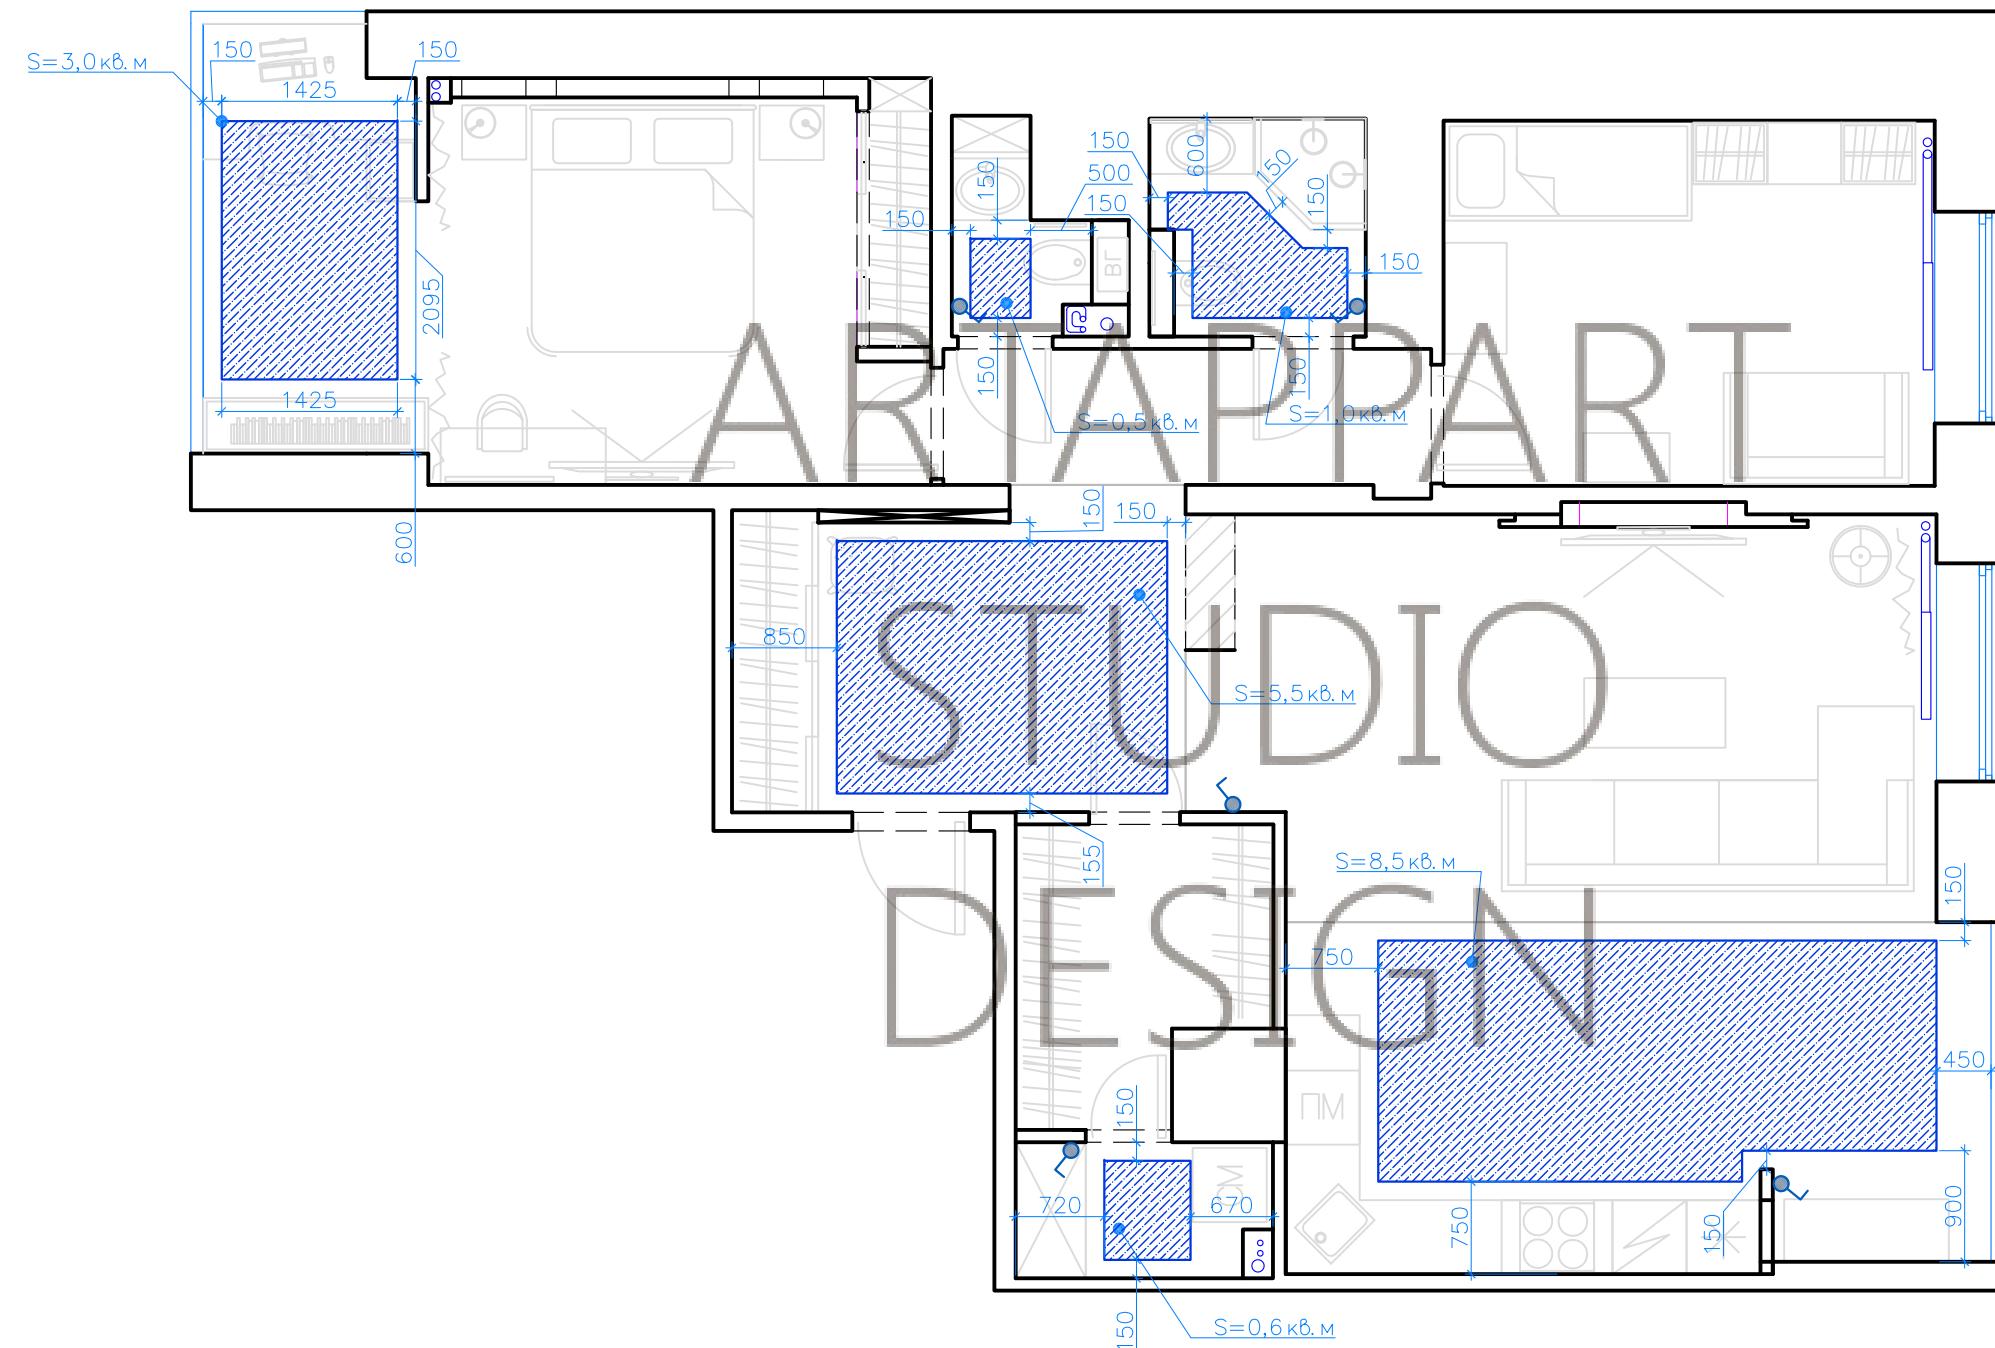


Условные обозначения:

- регулятор электрического теплого пола

Примечание:

- Границы расположения теплого пола удалены от напольных элементов мебели, стен и прочих конструкций на 100мм, если не указано иное.
 - Терморегуляторы расположить на высоте 400мм на оснащении электроустановочного оборудования, если не указано иное.
 - Все терморегуляторы установить посередине простенка, либо на расстоянии 250 мм от угла, если не указано иное.

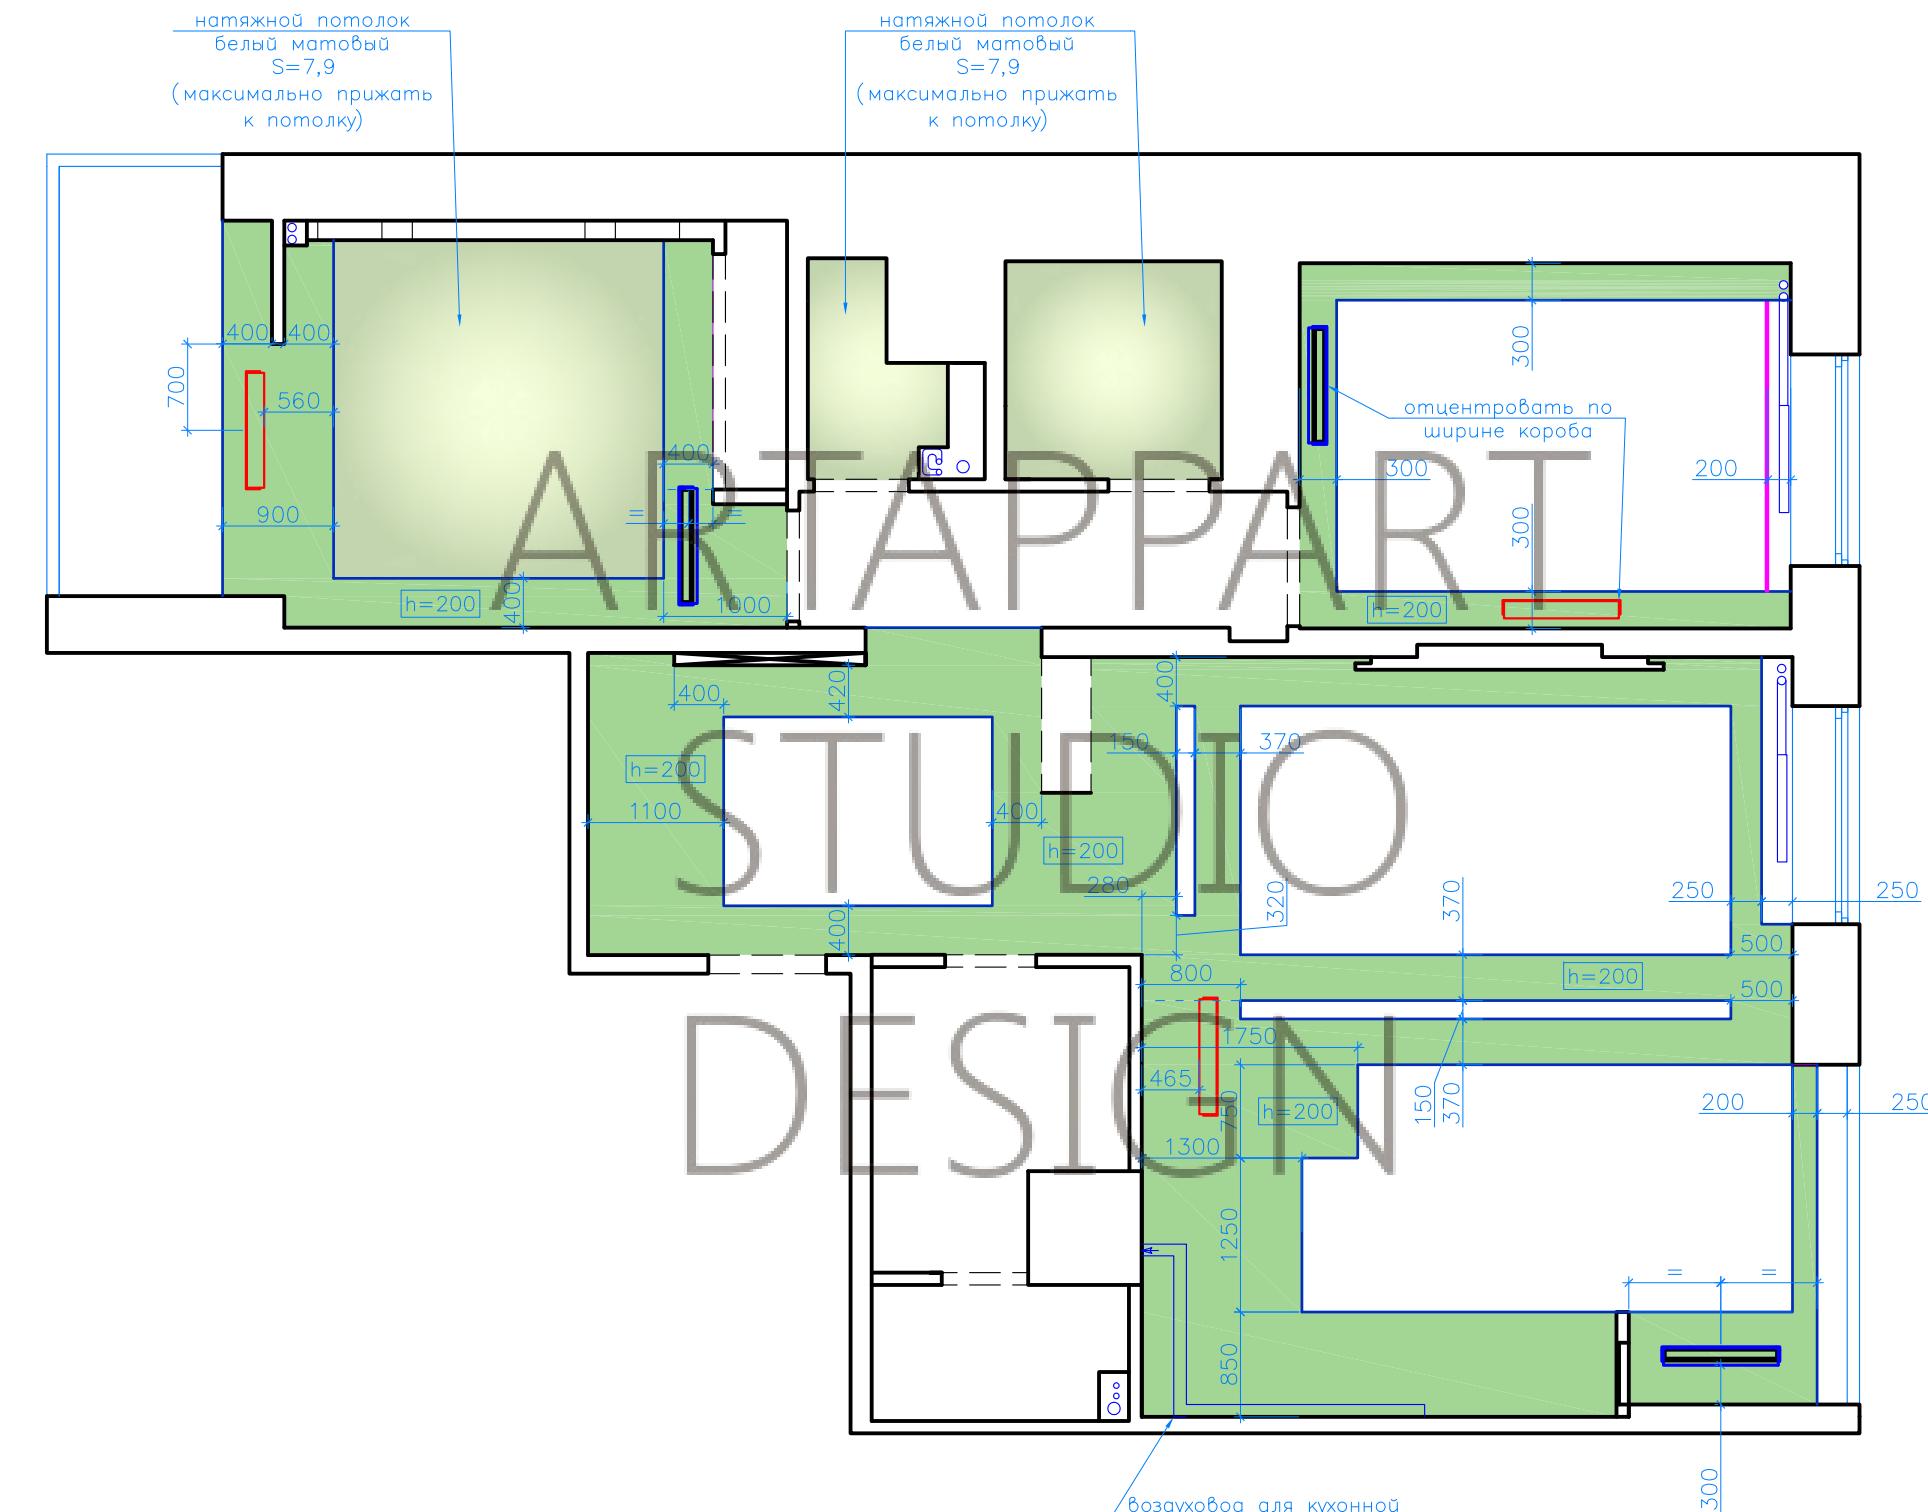

Условные обозначения

— подшивной потолок ГК

— закладная ГКЛ для потолочного карниза

— натяжной потоло

Примечание

1. Все покрытия белого цвета, если не указано иное.
 2. За исходный уровень принят уровень потолка с учетом проведенных мероприятий по выравниванию и звукоизоляции.
 3. Натяжные потолки монтируются на минимально возможном расстоянии от перекрытия, если не указано иное.

Согласовано

Инф. № по делу	Подп. и дата	Взам. инф.
----------------	--------------	------------

бра отцентровать по нишам
h=1000

встроенные точечные светильники в нишах

во всех нишах предусмотреть подсветку светодиодной лентой

2-1

1-1

1-2

h=1000


h=1500

h=1700

Условные обозначения

- | | | | |
|--|--------------------------|--|-------------------------|
| | — люстра | | — настенный светильник |
| | — светильник встроенный | | — лента светодиодная |
| | — бра/настен. светильник | | — потолочный светильник |
| | — эл. вывод | | |
| | — точечный светильник | | |

Изм.	Кол. уч	Листм	№ док	Подп.	Дата	Разработка дизайн-проекта квартиры	Стадия	Листм	Листмов
Заказчик				2017			P		
Разработ.				2017		План привязки освещительных приборов M 1:70		ARTAPPART DESIGN STUDIO	

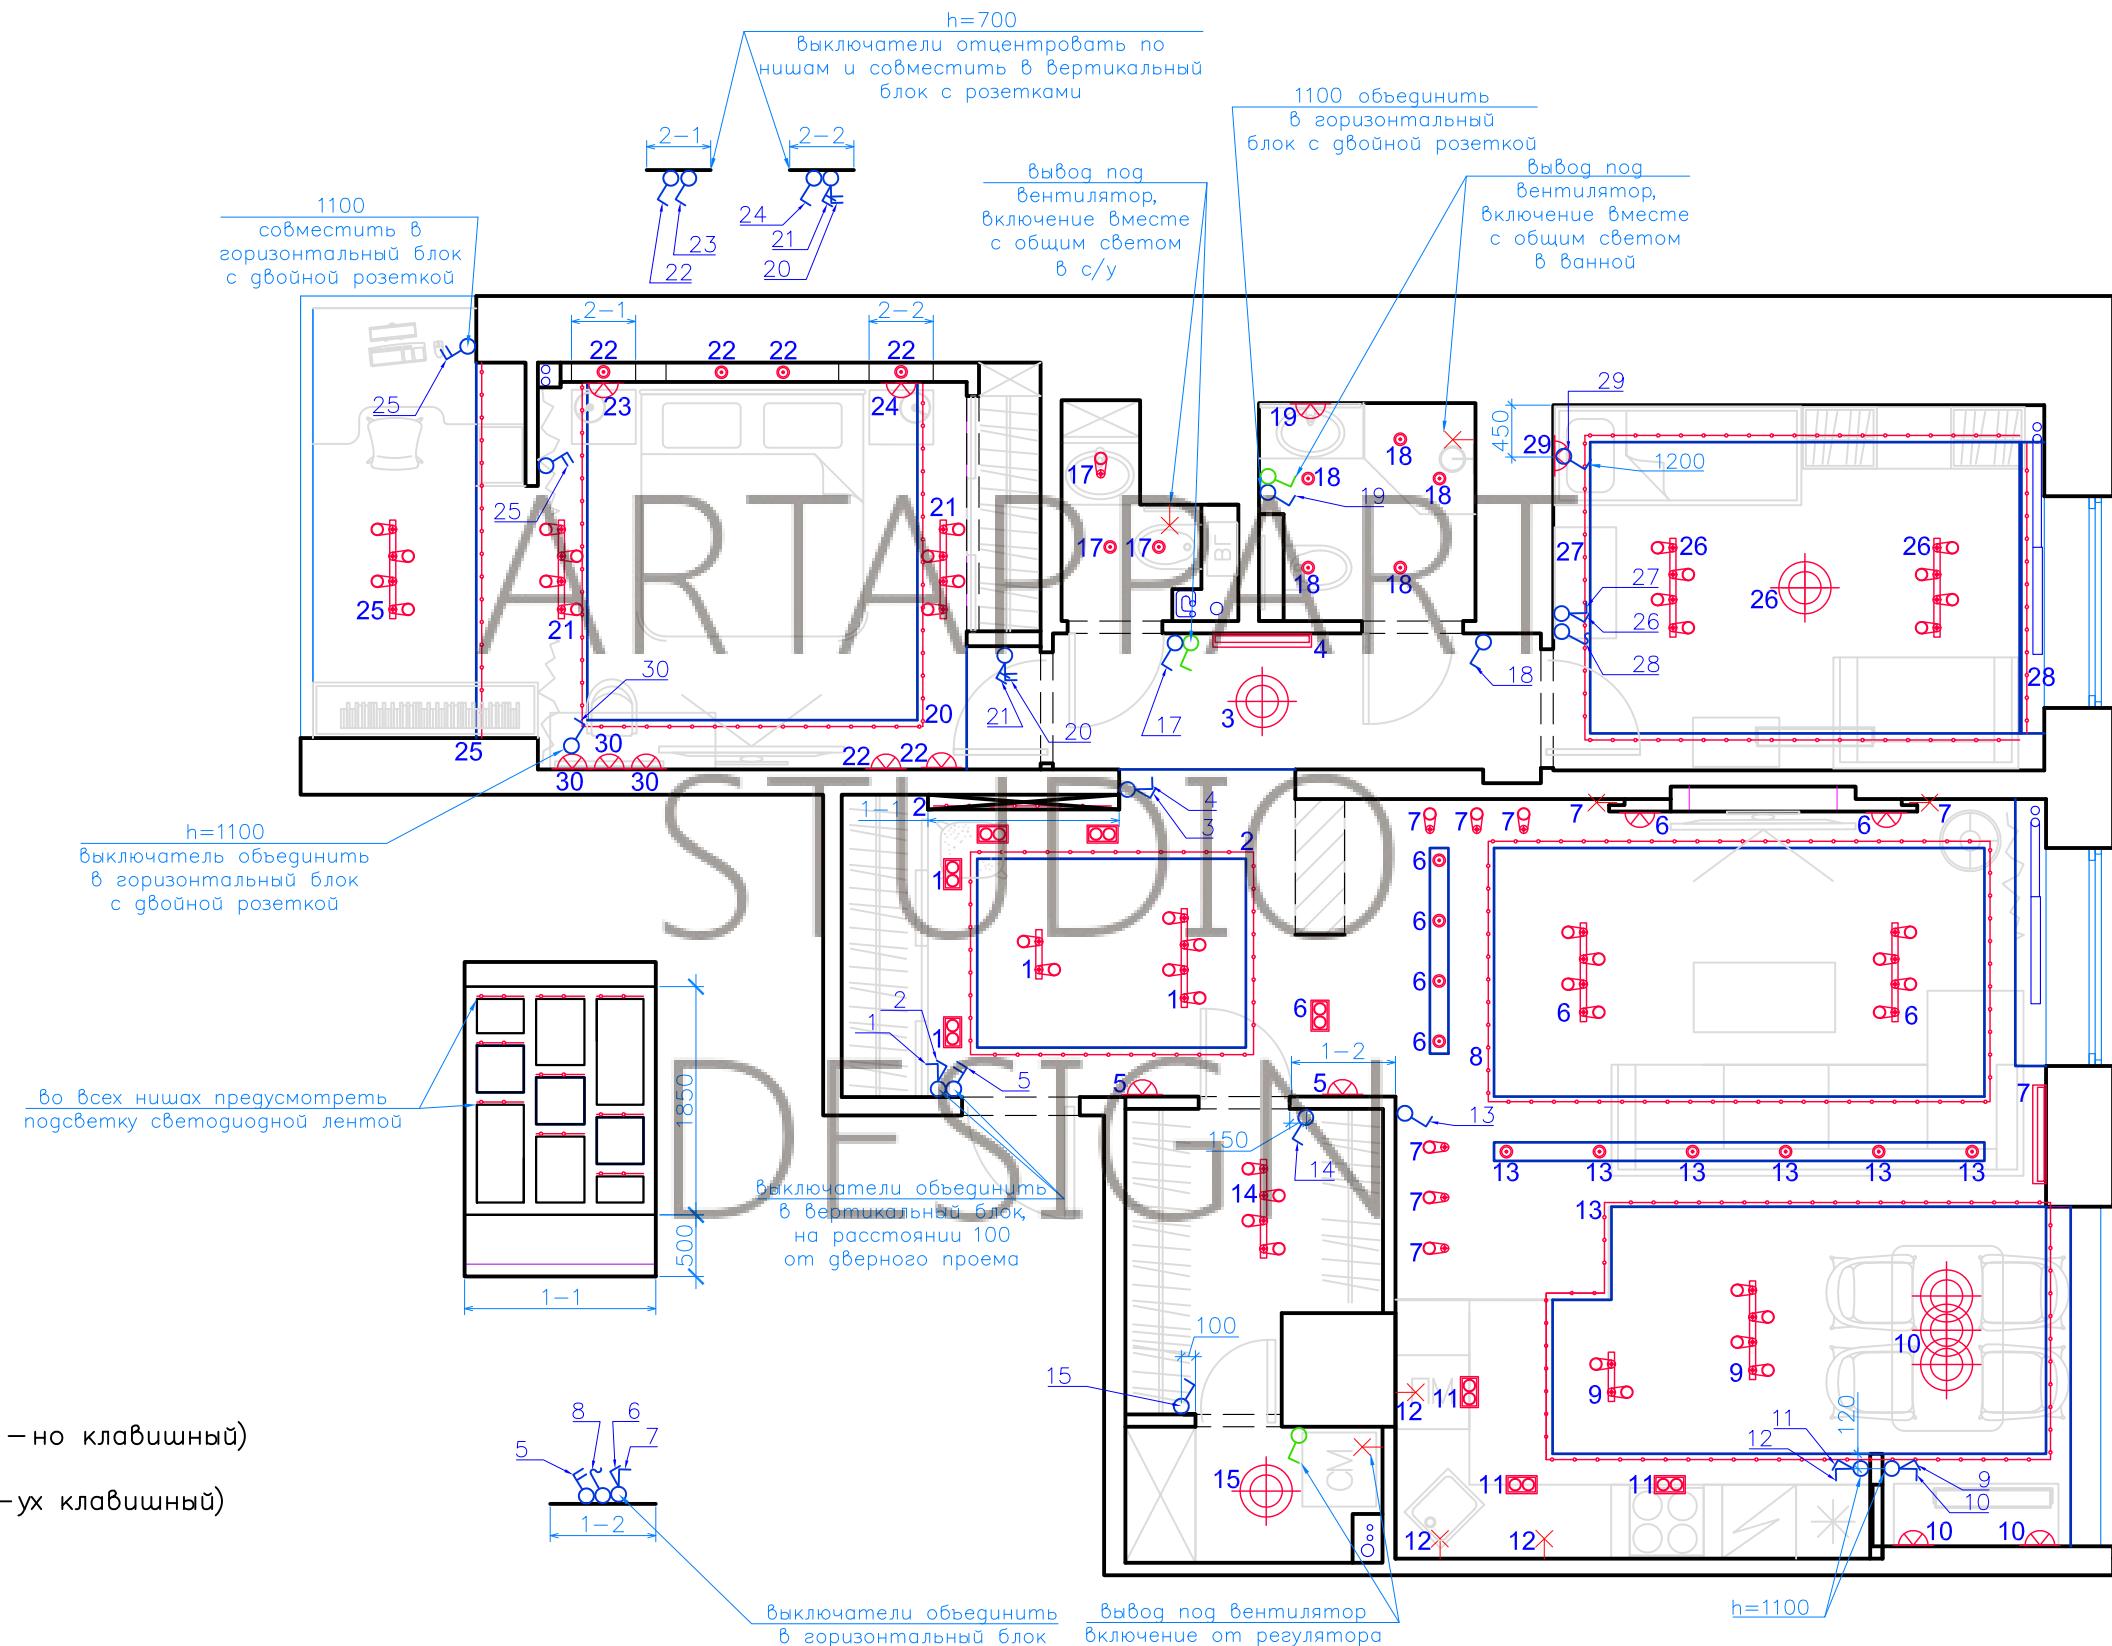


Условные обозначения

-  – выключатель (1-но клавишный)
 -  – выключатель (2-ух клавишный)
 -  – диммер
 -  – переключатель
 -  – вкл. вентиляции

Примечание:

1. Все выключатели устанавливать посередине простенка либо на расстояние 250мм от угла, если не указано иное;
 2. Высота до оси выключателя(–лей) 900мм от УЧП, если не указано иное;
 3. Количество номеров групп светильников у выключателя определяет его тип: 1–но / 2–ух клавишный;
 4. Привязки даны в мм от УЧП до осей приборов.
 5. Для возможности редактирования рекомендуется оставлять выводы достаточной длины.

Изм.	Кол. уч.	Листм	№ док.	Подп.	Дата	Разработка дизайн-проекта квартиры	Стадия	Листм	Листов
Заказчик					2017				
Разработ.					2017		P		
						План разводки осветительных приборов на выключатели М 1: 70			
								ARTAPPART DESIGN STUDIO	

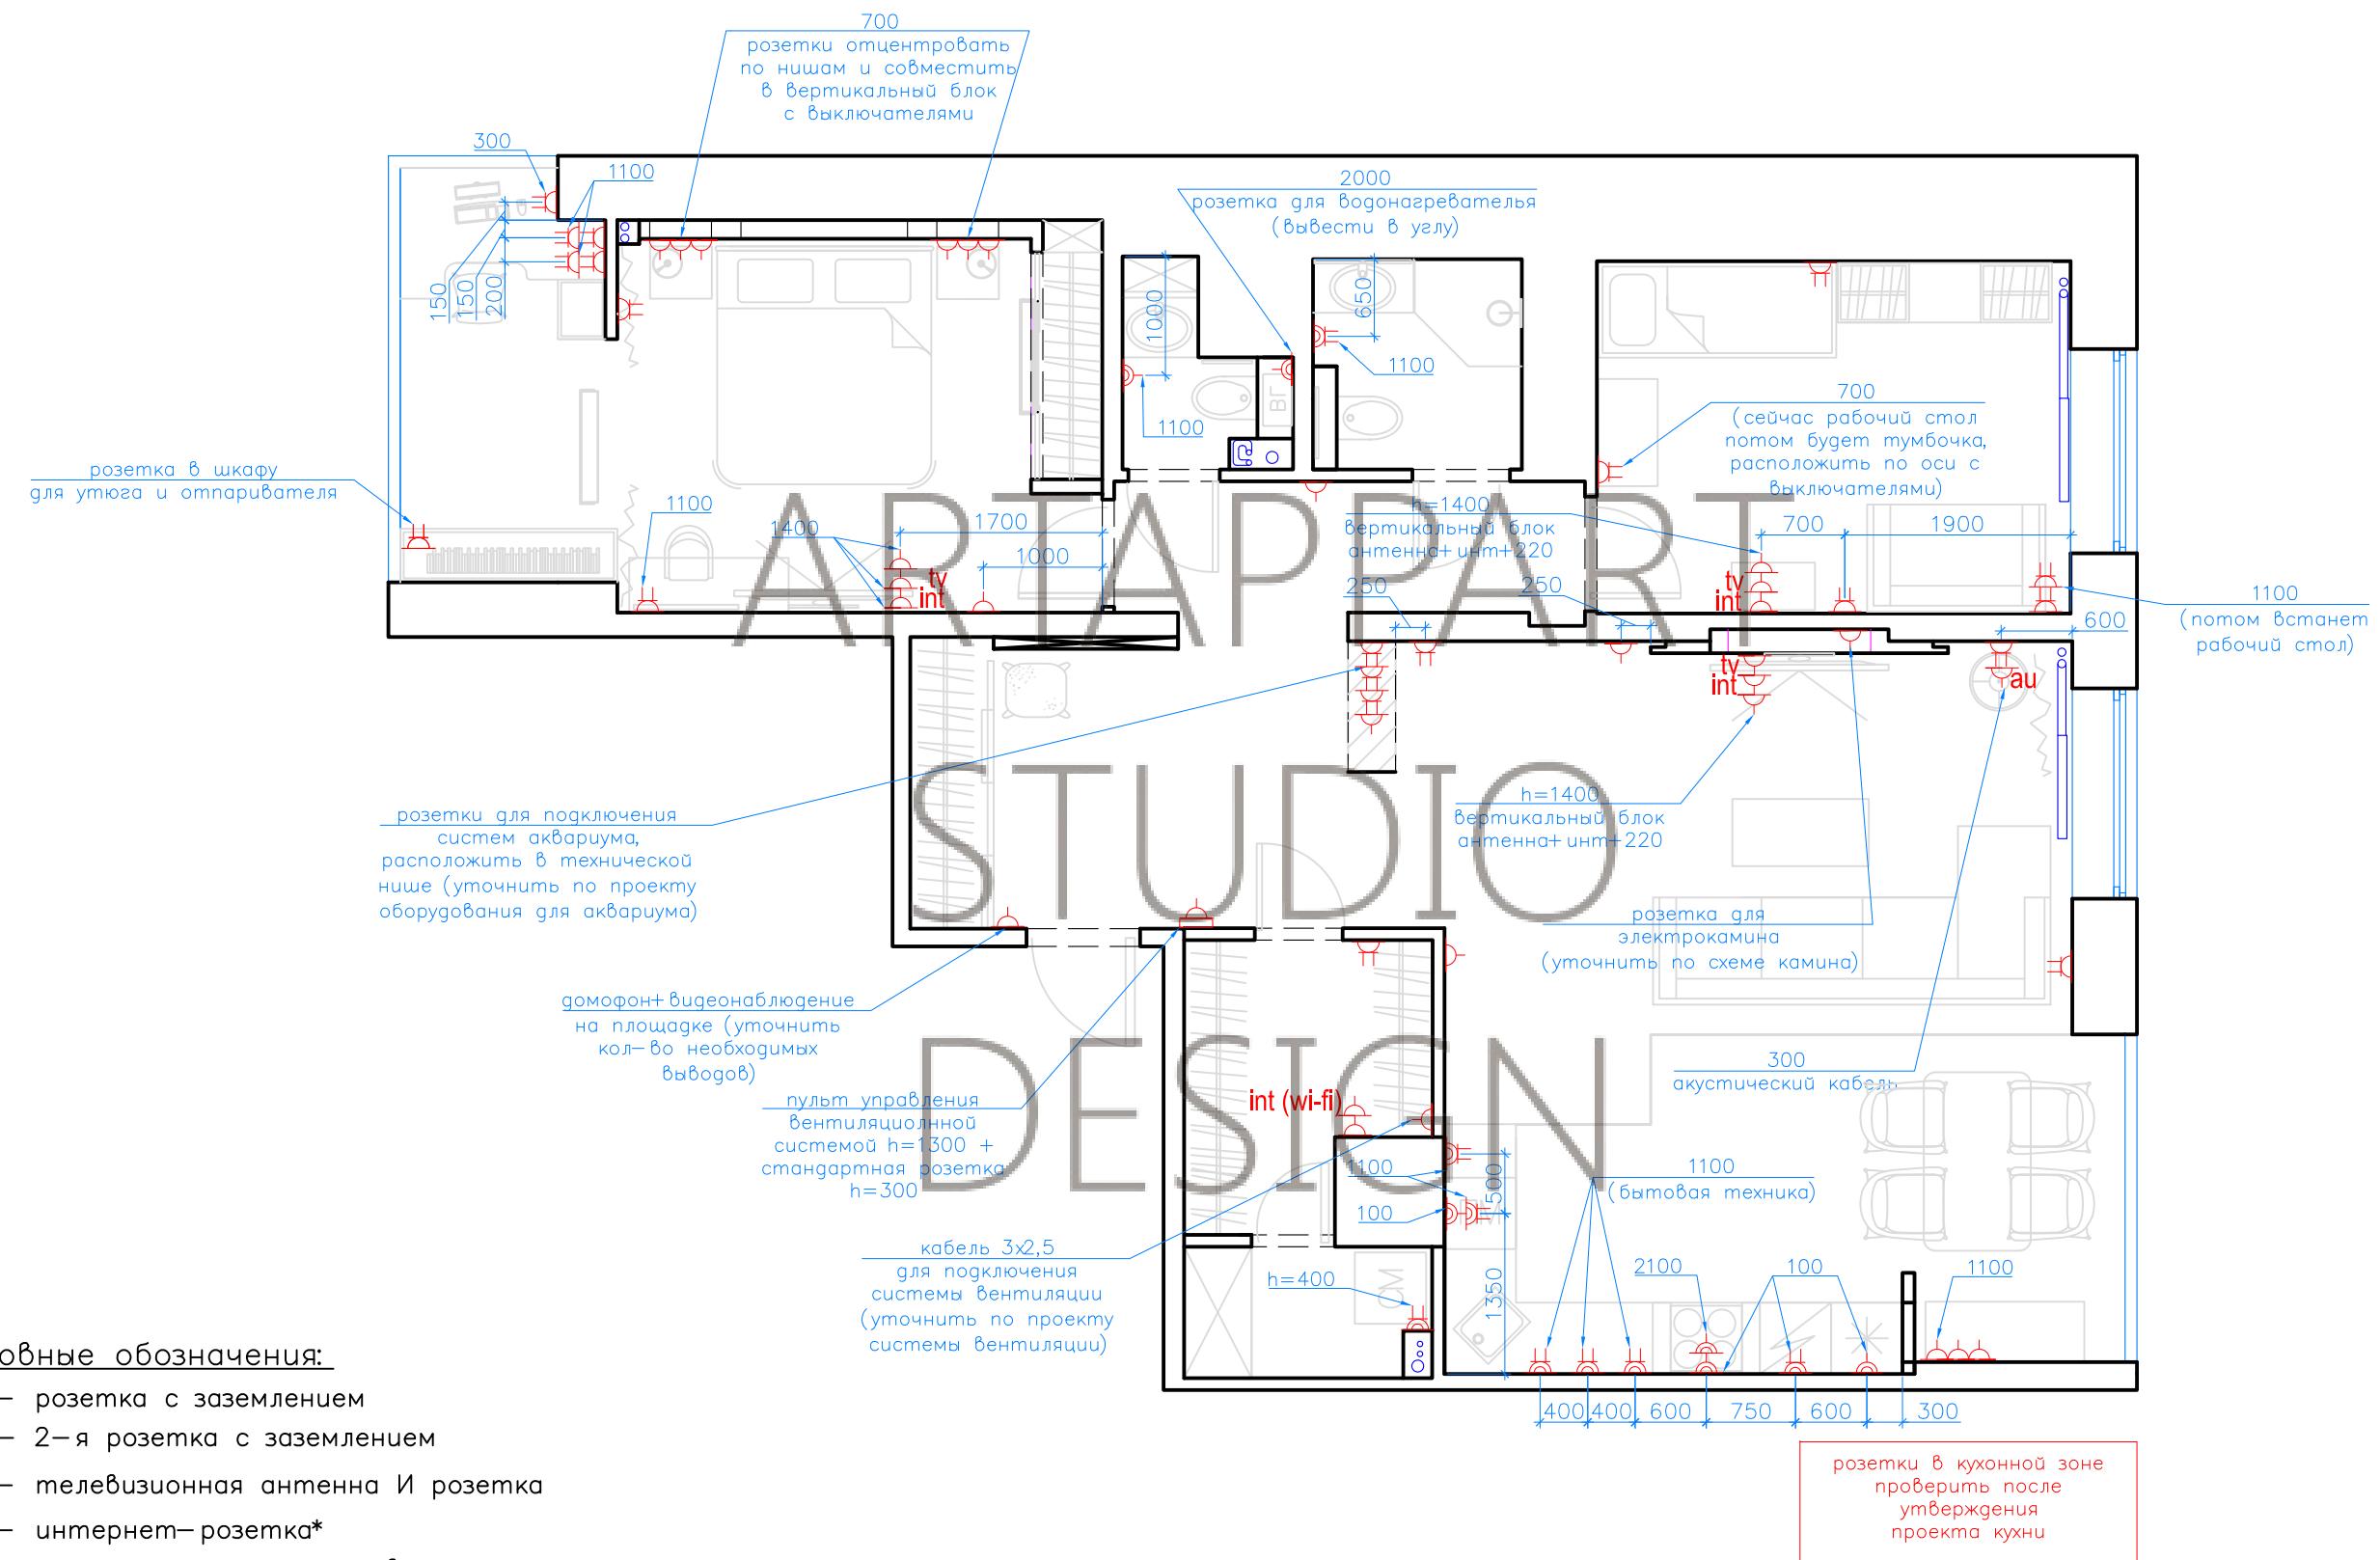

Условные обозначения

 – розетка с заземлением

 – 2-я розетка с заземлением

 – телевизионная антенна И розетка

 – интернет-розетка

 – розетка с заземлением Влагостойк.

 – 2-я розетка с заземлением

 – вывод акустического кабеля


↓ = эл. Выброс

Примечание:

1. Все розетки, кроме обозначенных, установить на высоте 300 мм от УЧП.
 2. Розетки располагать посередине проспенка либо на расстоянии 250 мм от угла, если привязки не указаны;
 3. Привязки даны в мм от УЧП до осей приборов.
 4. Для возможности редактирования рекомендуется оставлять выводы достаточной длины.


Изм.	Код уч.	Листм	№ док.	Подп.	Дата	Разработка дизайн-проекта квартиры	Статус	Листм	Листмов
Заказчик				2017			P		
Разработ				2017					
						План электрики и электропроводов М 1:60		ARTAPPART DESIGN STUDIO	

The image shows a technical drawing of a cabinet assembly. The drawing includes a top view of the cabinet's footprint and a front view showing the cabinet's height and depth. The cabinet is divided into sections labeled 1-2, 1-3, and 1-4. A detailed side view on the right shows the cabinet's profile with dimensions: height 2160, depth 500, and width 850. The cabinet is labeled with the text 'ARTAPPART STUDIO DESIGN' and includes a small detail of a handle labeled '2'.

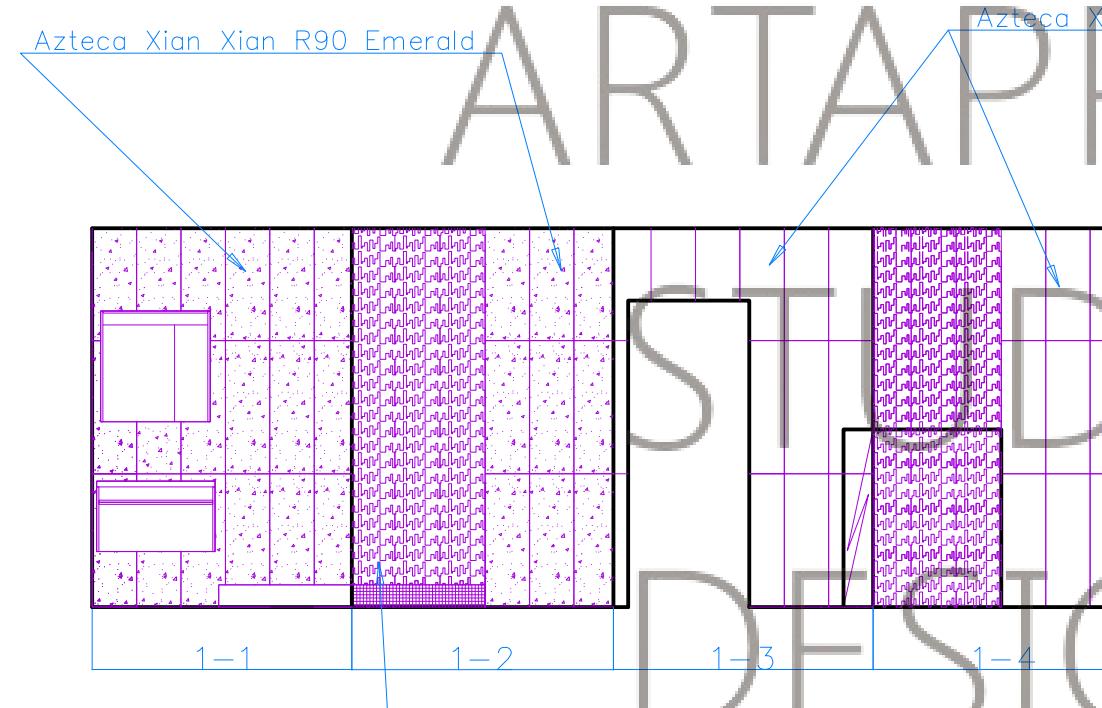

Azteca Xian Xian R90 Emerc

Azteca Xian Xian R90

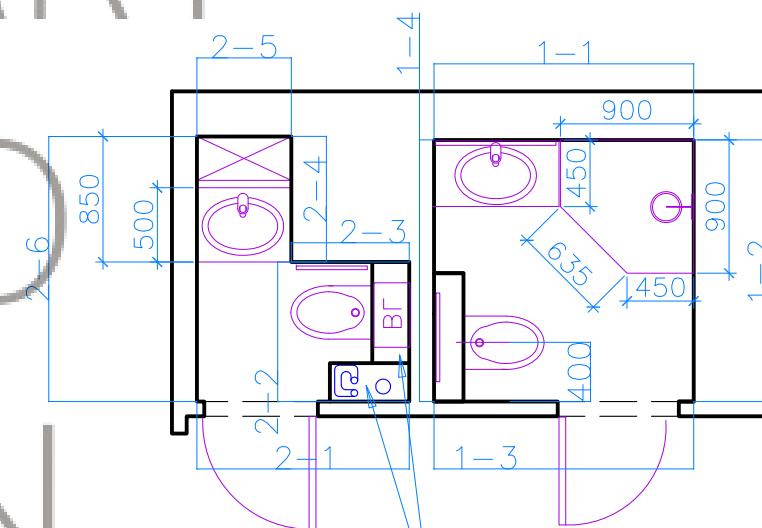

короб с трубами
до потолка,
инсталляция до 1200

Изм.	Кол. уч	Лист	№ док	Подп.	Дата					
Заказчик				2017		Разработка дизайн-проекта квартиры		Стадия	Лист	Листов
Разработ.				2017				P		
						M 1: 50		 ARTAPPART DESIGN STUDIO		

Изм.	Код. уч.	Листм	№ док.	Подп.	Дата	Разработка дизайн-проекта квартиры	Стадия	Листм	Листовъ
Заказчик					2017	Развертки по стенам, ванная комната и санузел M 1: 50	Р		
Разработ					2017				

Согласовано			

1 вариант



Плитка декор
Italon
Размер: 40x80

Плитка напольная
Italon
Размер: 40x160

3 вариант



Плитка напольная
41zero42 Futura
Размер: 15x15

Плитка настенная
41zero42 Futura
Размер: 15x15



Плитка настенная
Italon
Размер: 40x80

STUDIO

2 вариант



Плитка декор
Italon
Размер: 20x80

Плитка настенная
Equipe Chevron
Размер: 5,2x18,6

Плитка настенная
Equipe Chevron
Размер: 10,7x12,4

Изм.	Кол. уч	Листм	№ док	Подп.	Дата	Разработка дизайн-проекта квартиры	Стадия	Листм	Листмов
Заказчик					2017		P		
Разработ.					2017				

Примечание:

Данные коллажи представлены для примера, не относятся к приложенной рабочей документации.


Согласовано			

1 вариант



Плитка настенная
Керамика Марazzi Рафаль
Размер: 300x895

2 вариант

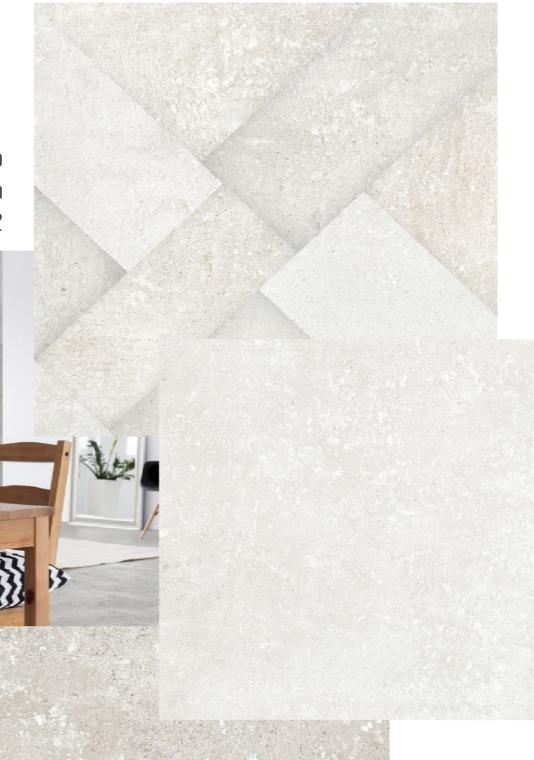

Плитка декор
Absolut Keramika Luzon
Размер: 592x592

3 вариант



Плитка декор
Equipe Misco
Размер: 200x200

Плитка настенная
Equipe Misco
Размер: 200x200

Плитка напольная
Equipe Misco
Размер: 200x200

Примечание:
Данные коллажи представлены для примера, не относятся к приложенной
рабочей документации.

KARTAPPART

STUDIO



Плитка напольная
Absolut Keramika Luzon
Размер: 592x592

Изм.	Кол. уч	Лист	№ док	Подп.	Дата	Разработка дизайн-проекта квартиры	Стадия	Лист	Листов
Заказчик					2017		P		
Разработ.					2017				