



## Дизайн проект "Стандартный"

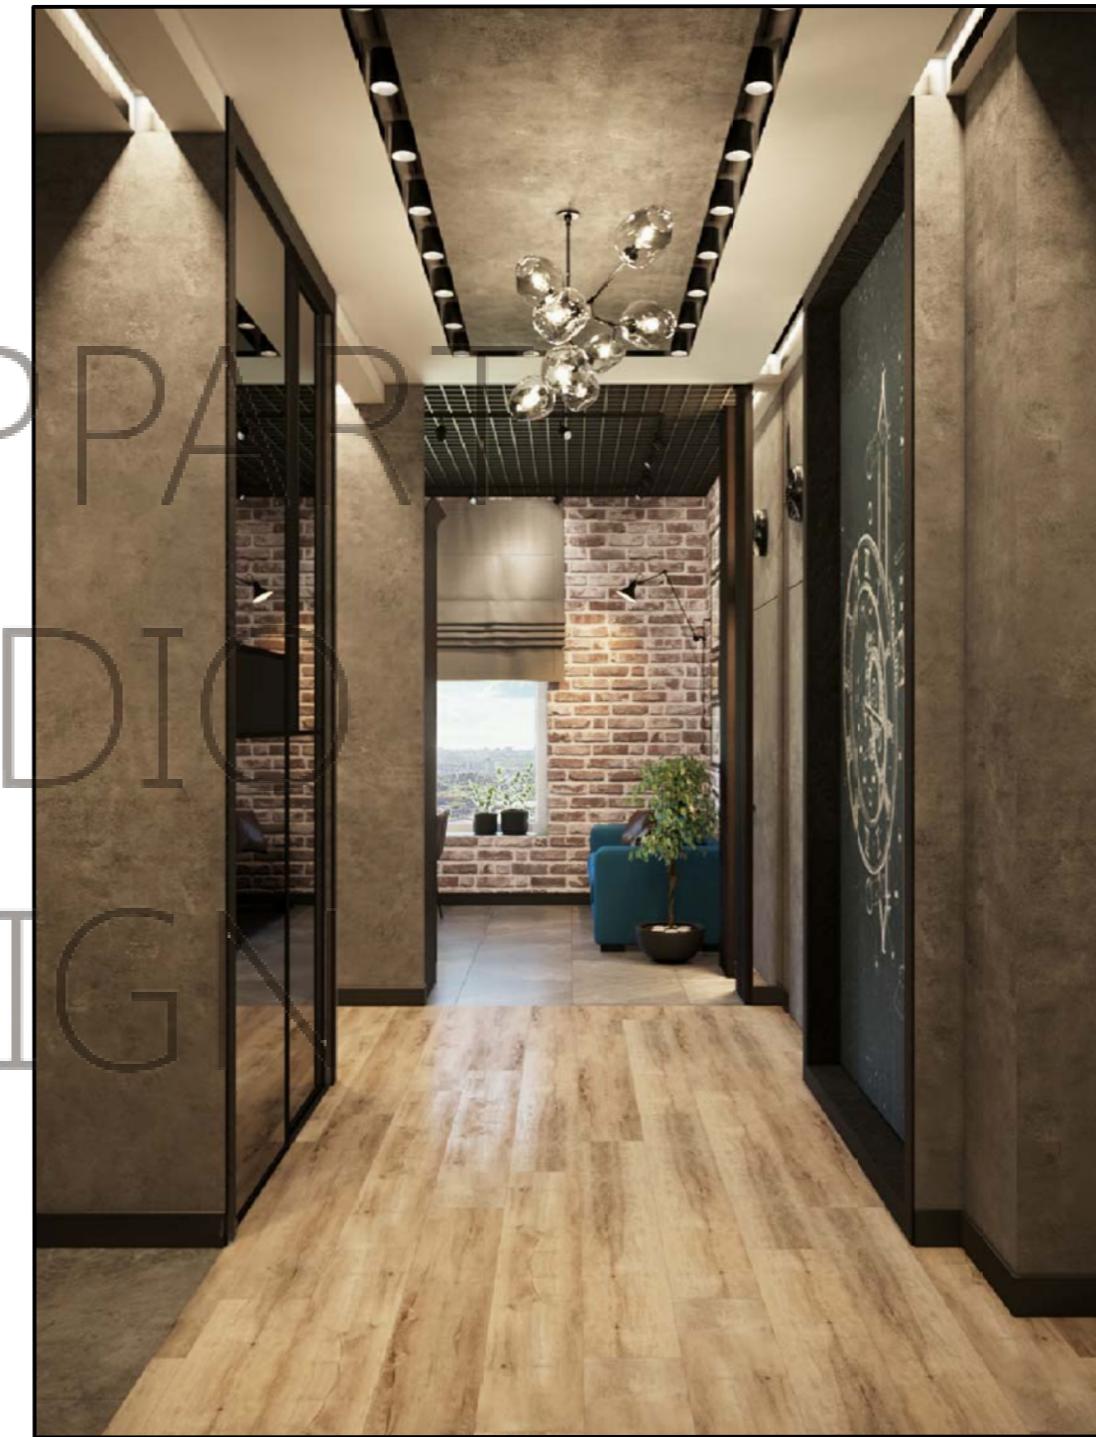










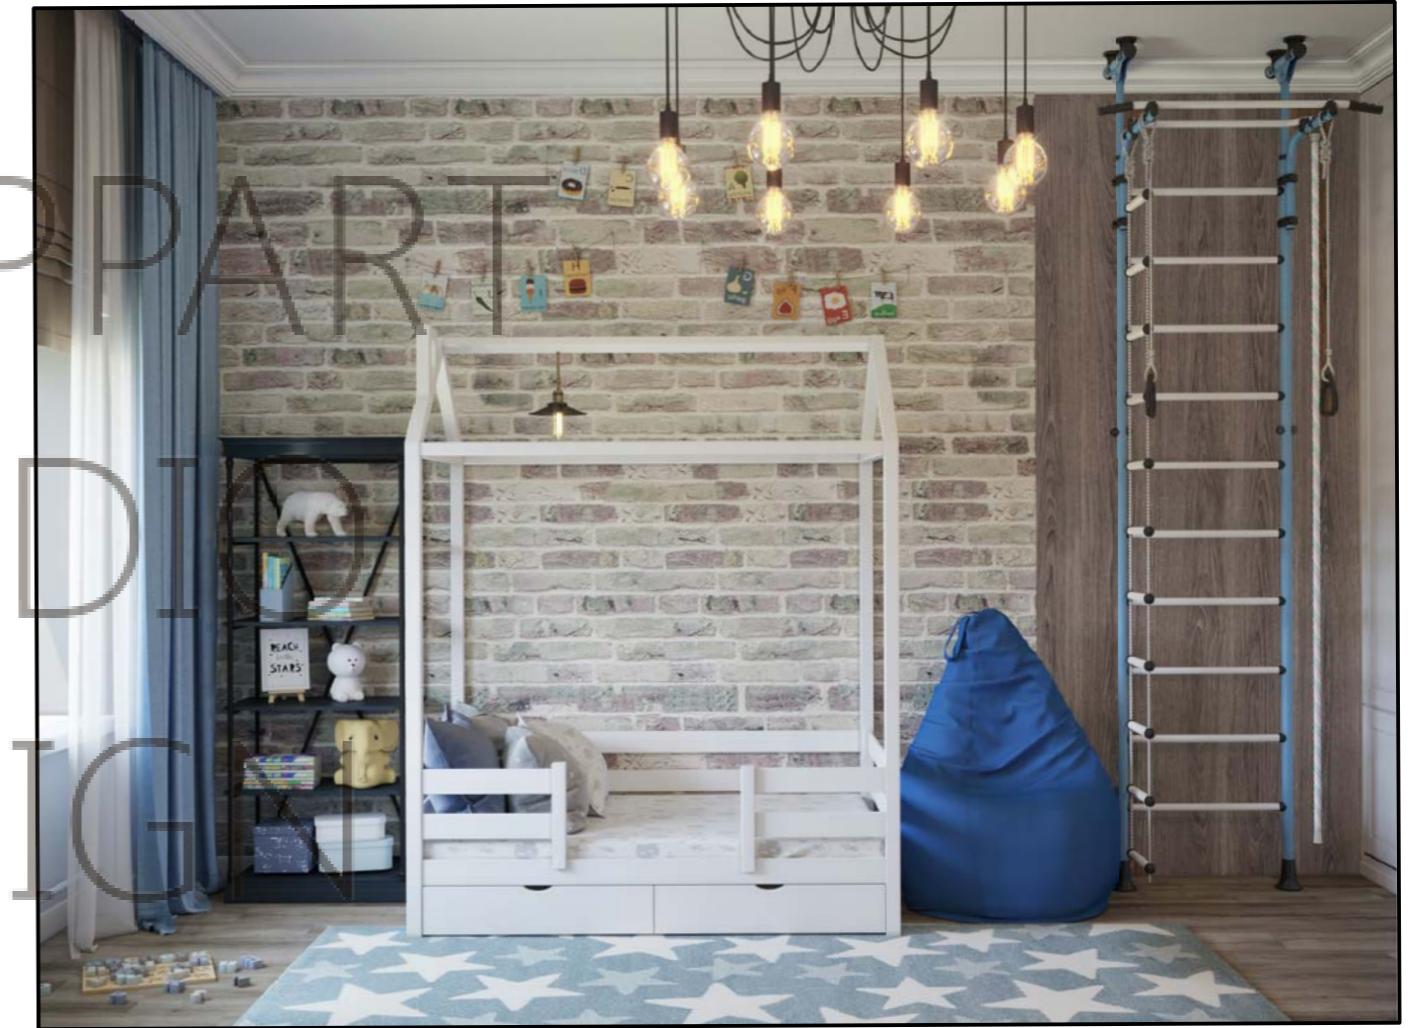








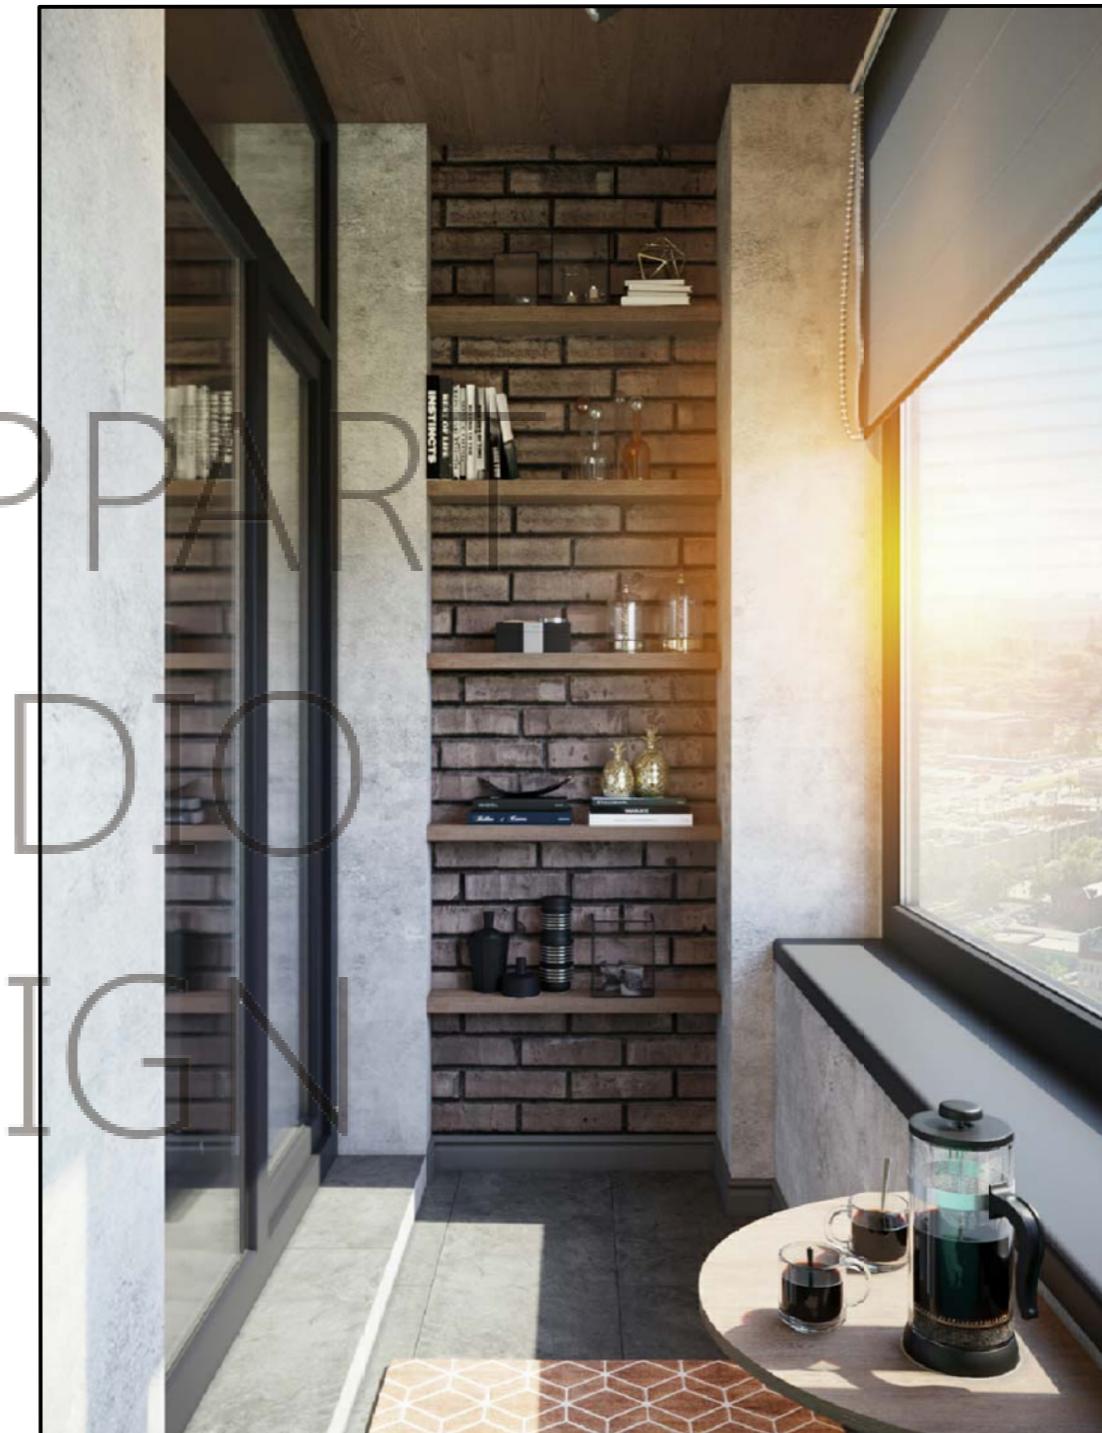

ARTAPAR  
STUDIO  
DESIGN

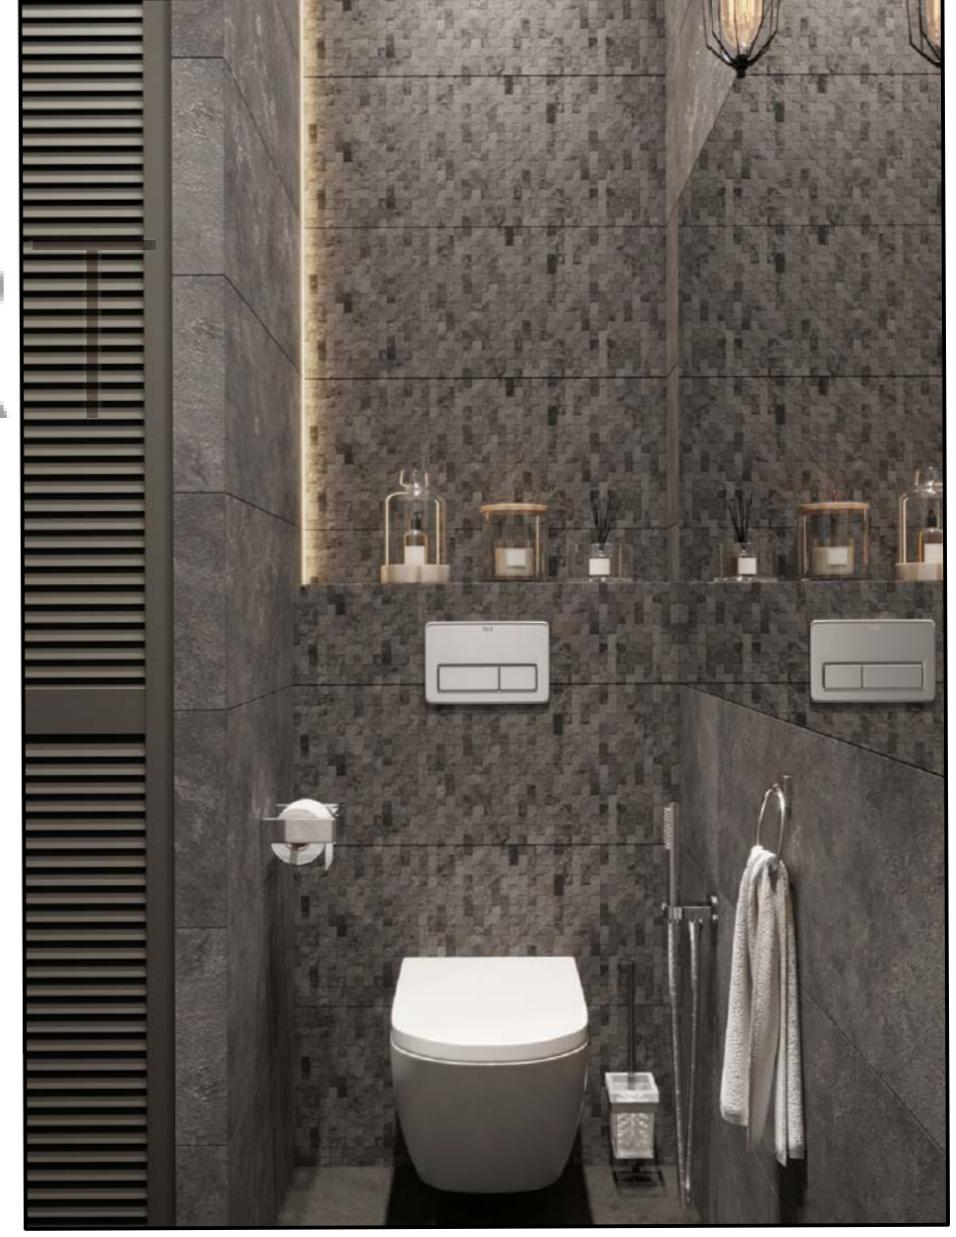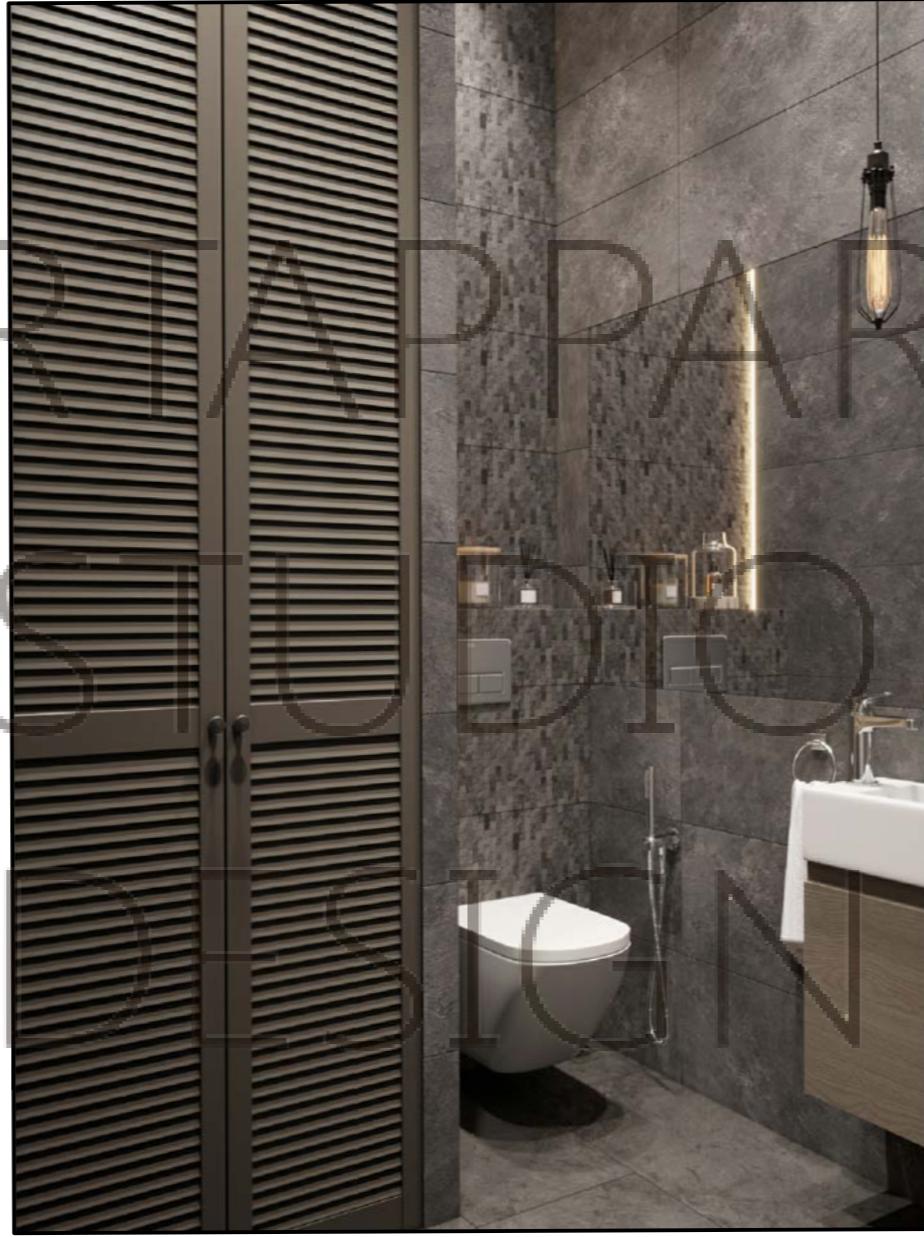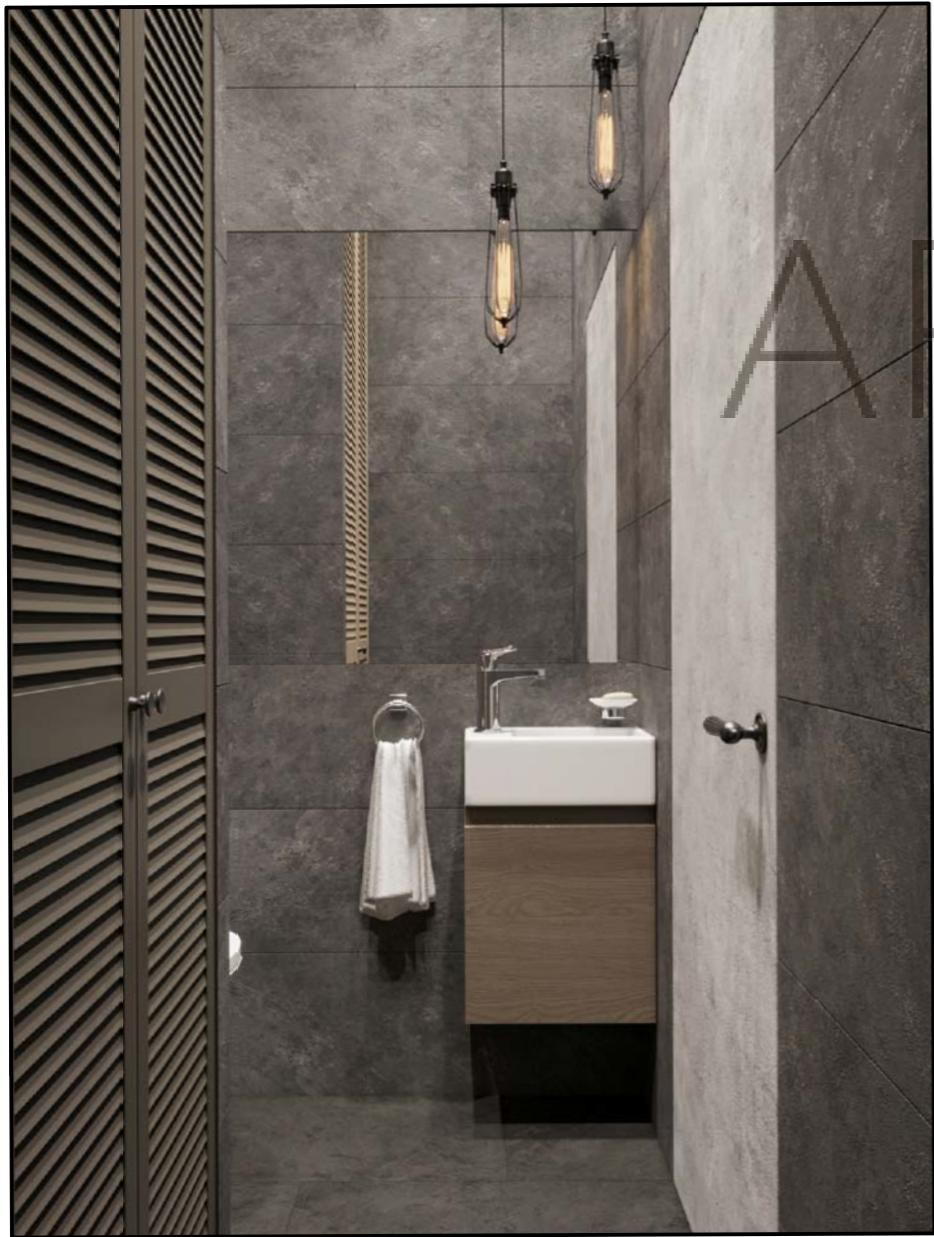

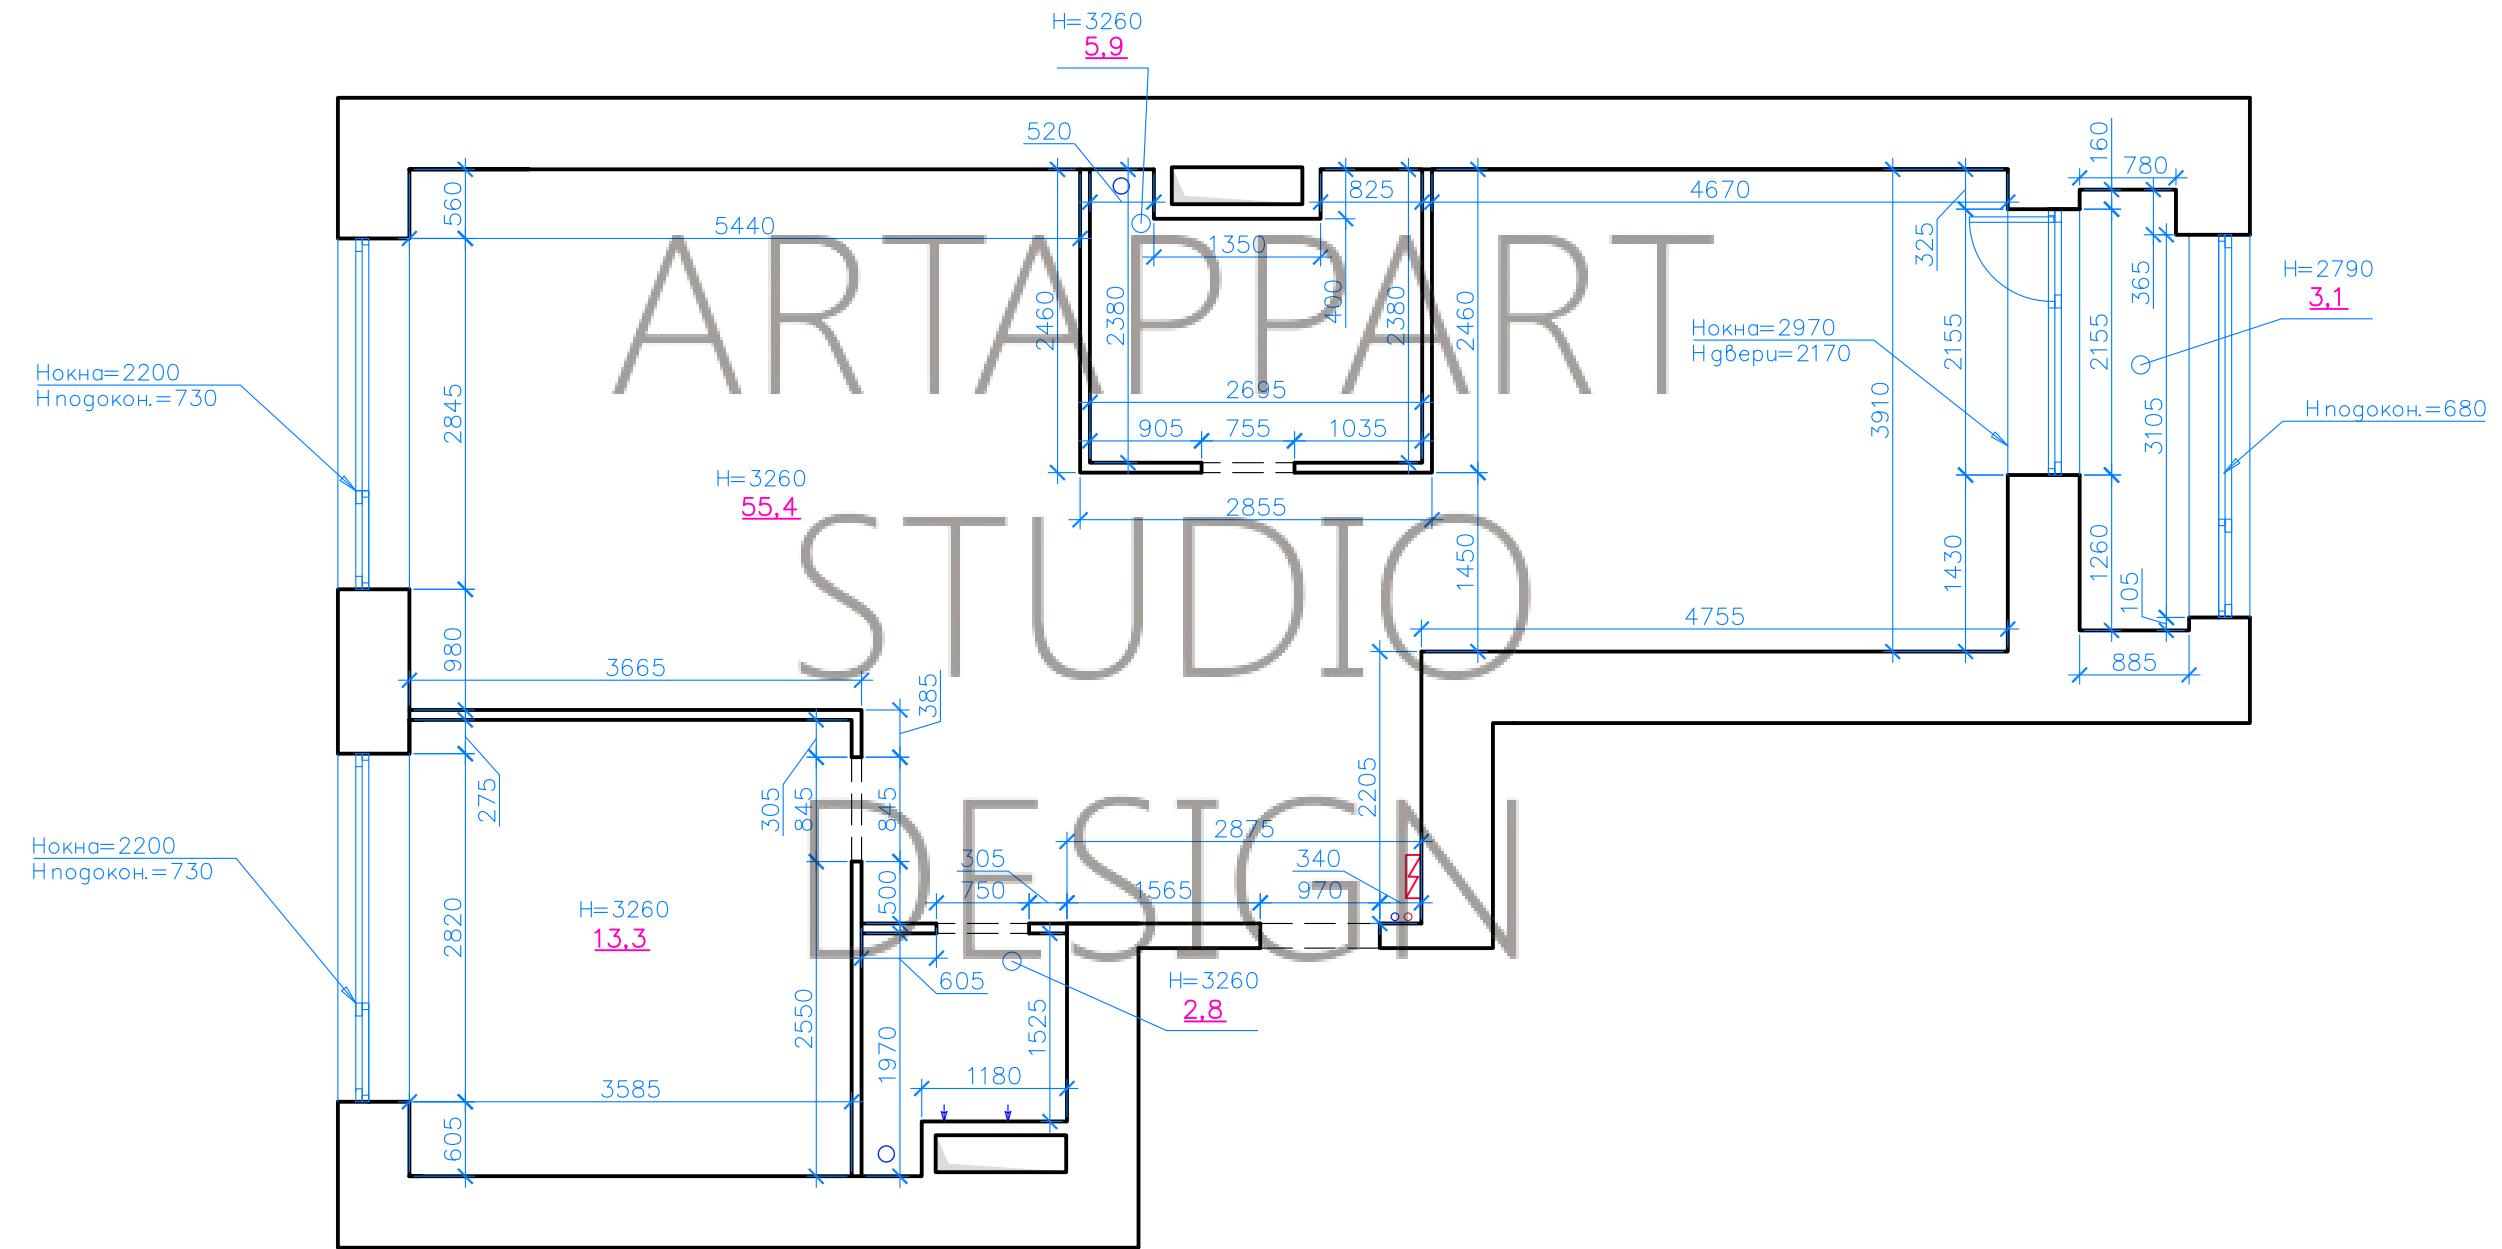

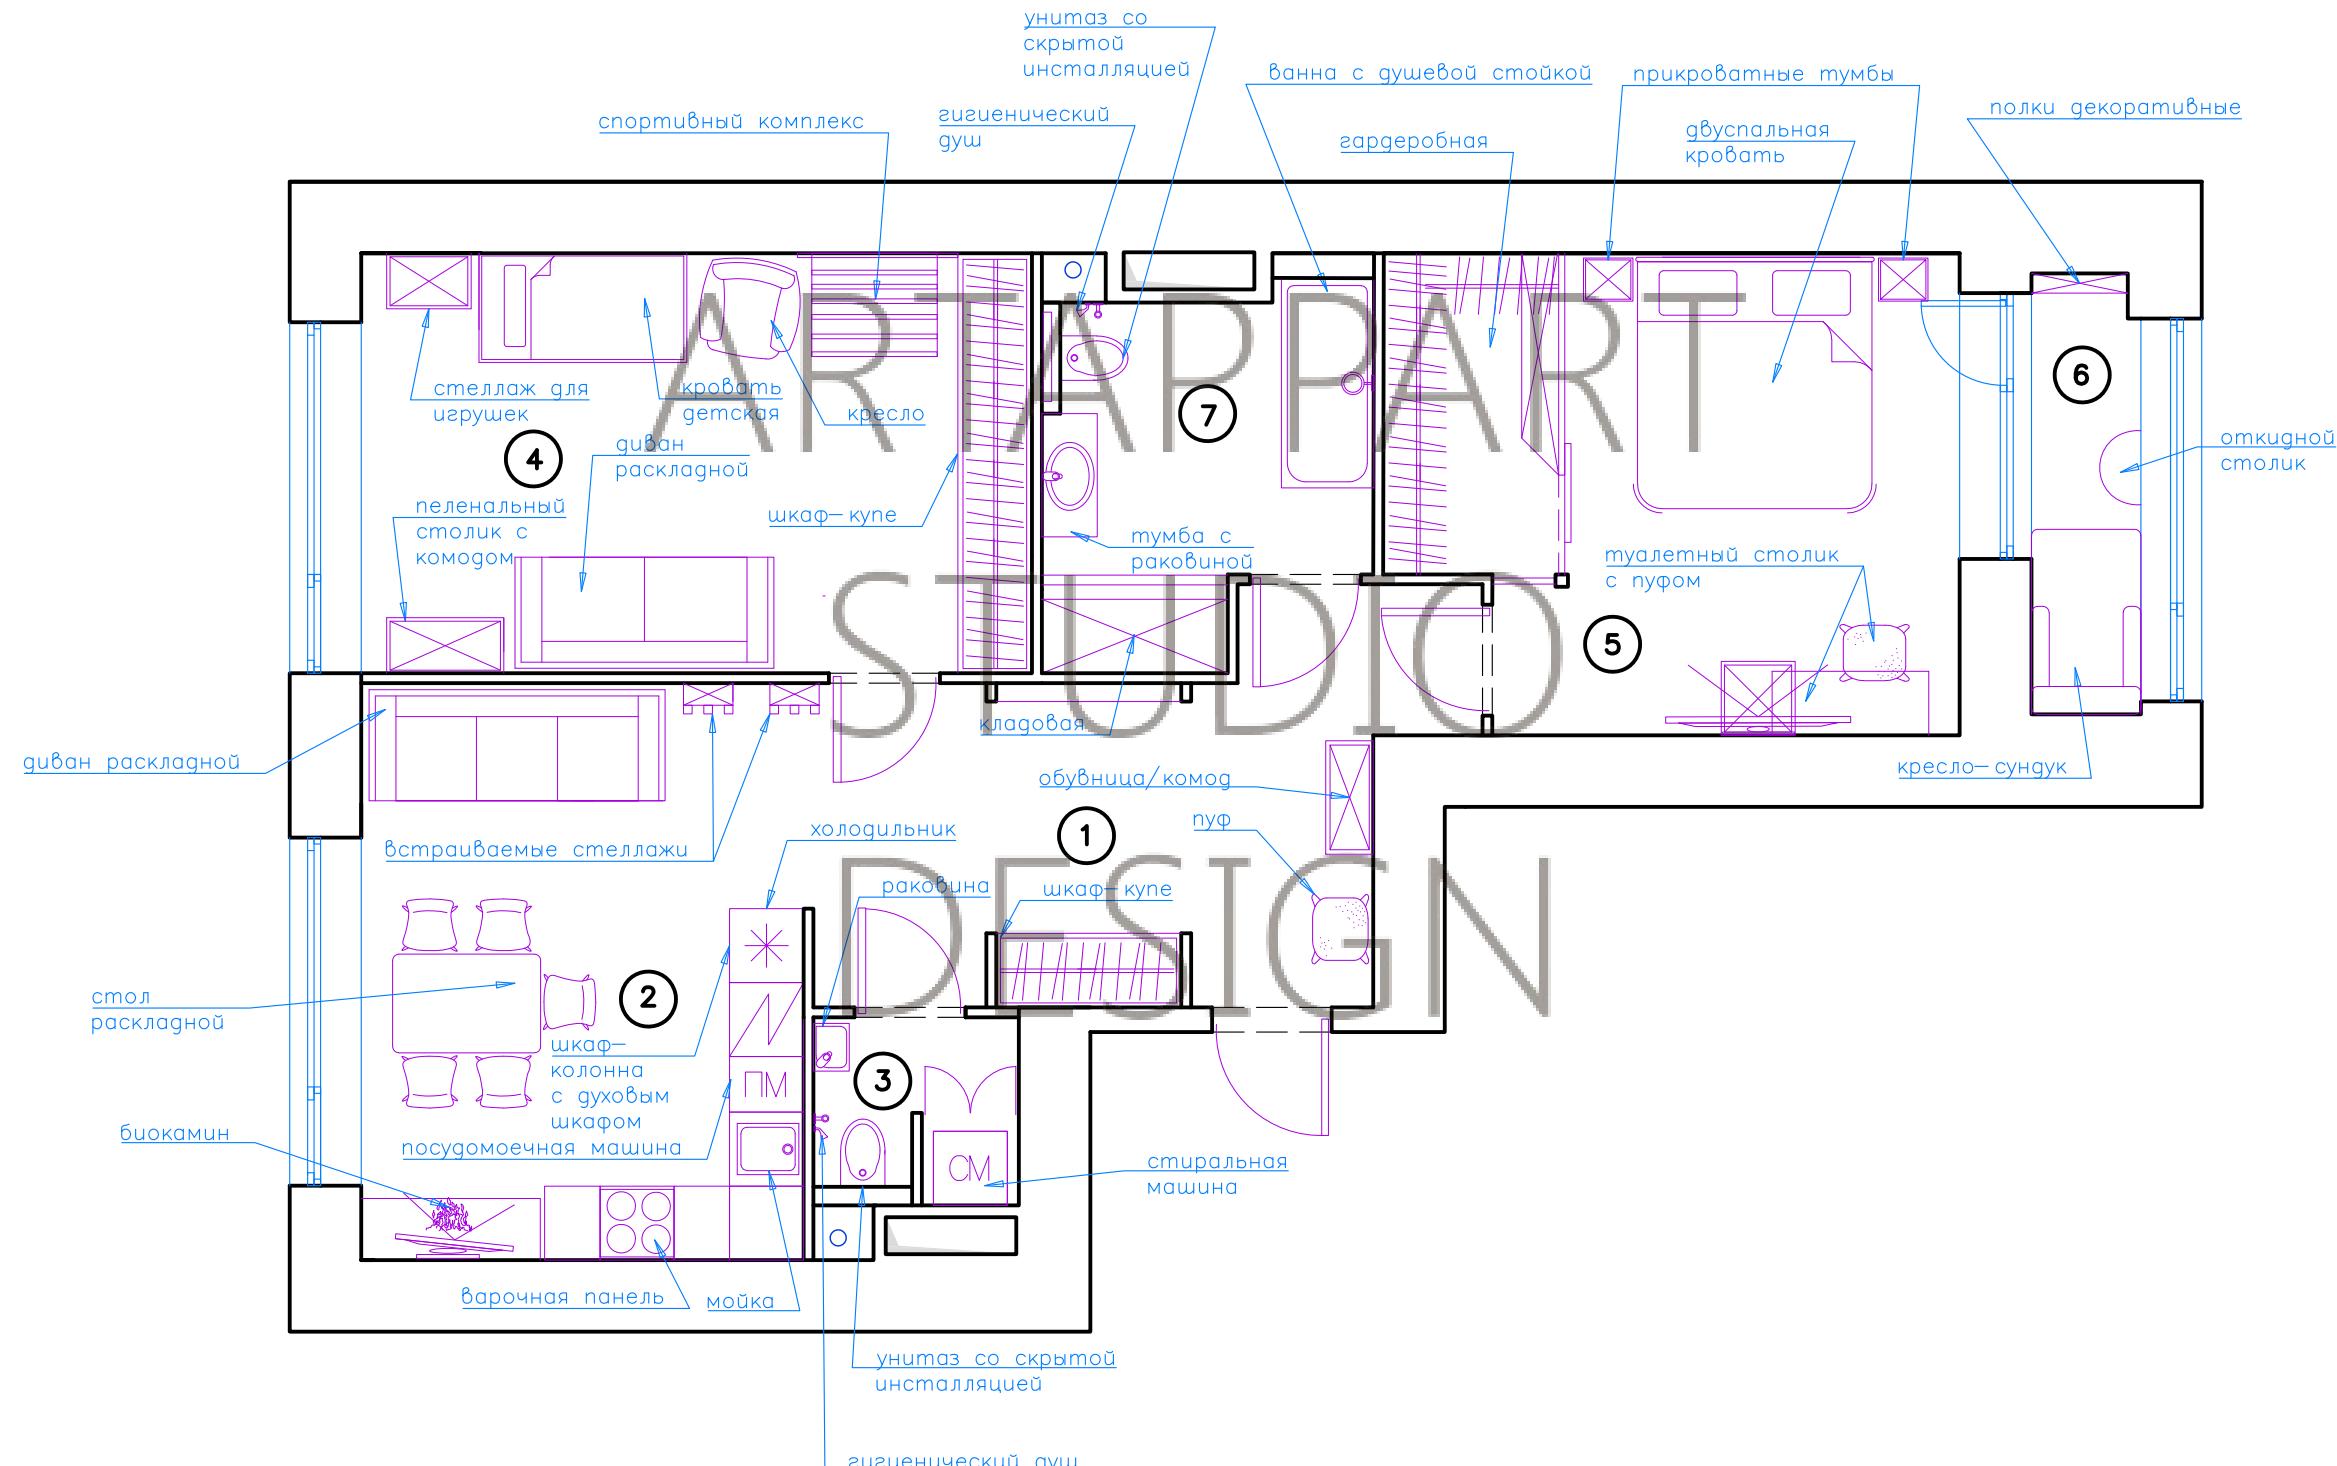

Экспликация:


- 1) Прихожая
- 2) Гостиная-кухня
- 3) Санузел
- 4) Детская
- 5) Спальня
- 6) Лоджия
- 7) Ванная комната

Изм.	Кол. уч.	Лист	№ док.	Подп.	Дата	Разработка дизайн-проекта квартиры	Стадия	Лист	Листов
Заказчик					2019				
Разработ.					2019	План расположения мебели и оборудования	Р		

План расположения мебели и оборудования  
М 1:60



ARTAPPART  
DESIGN  
STUDIO

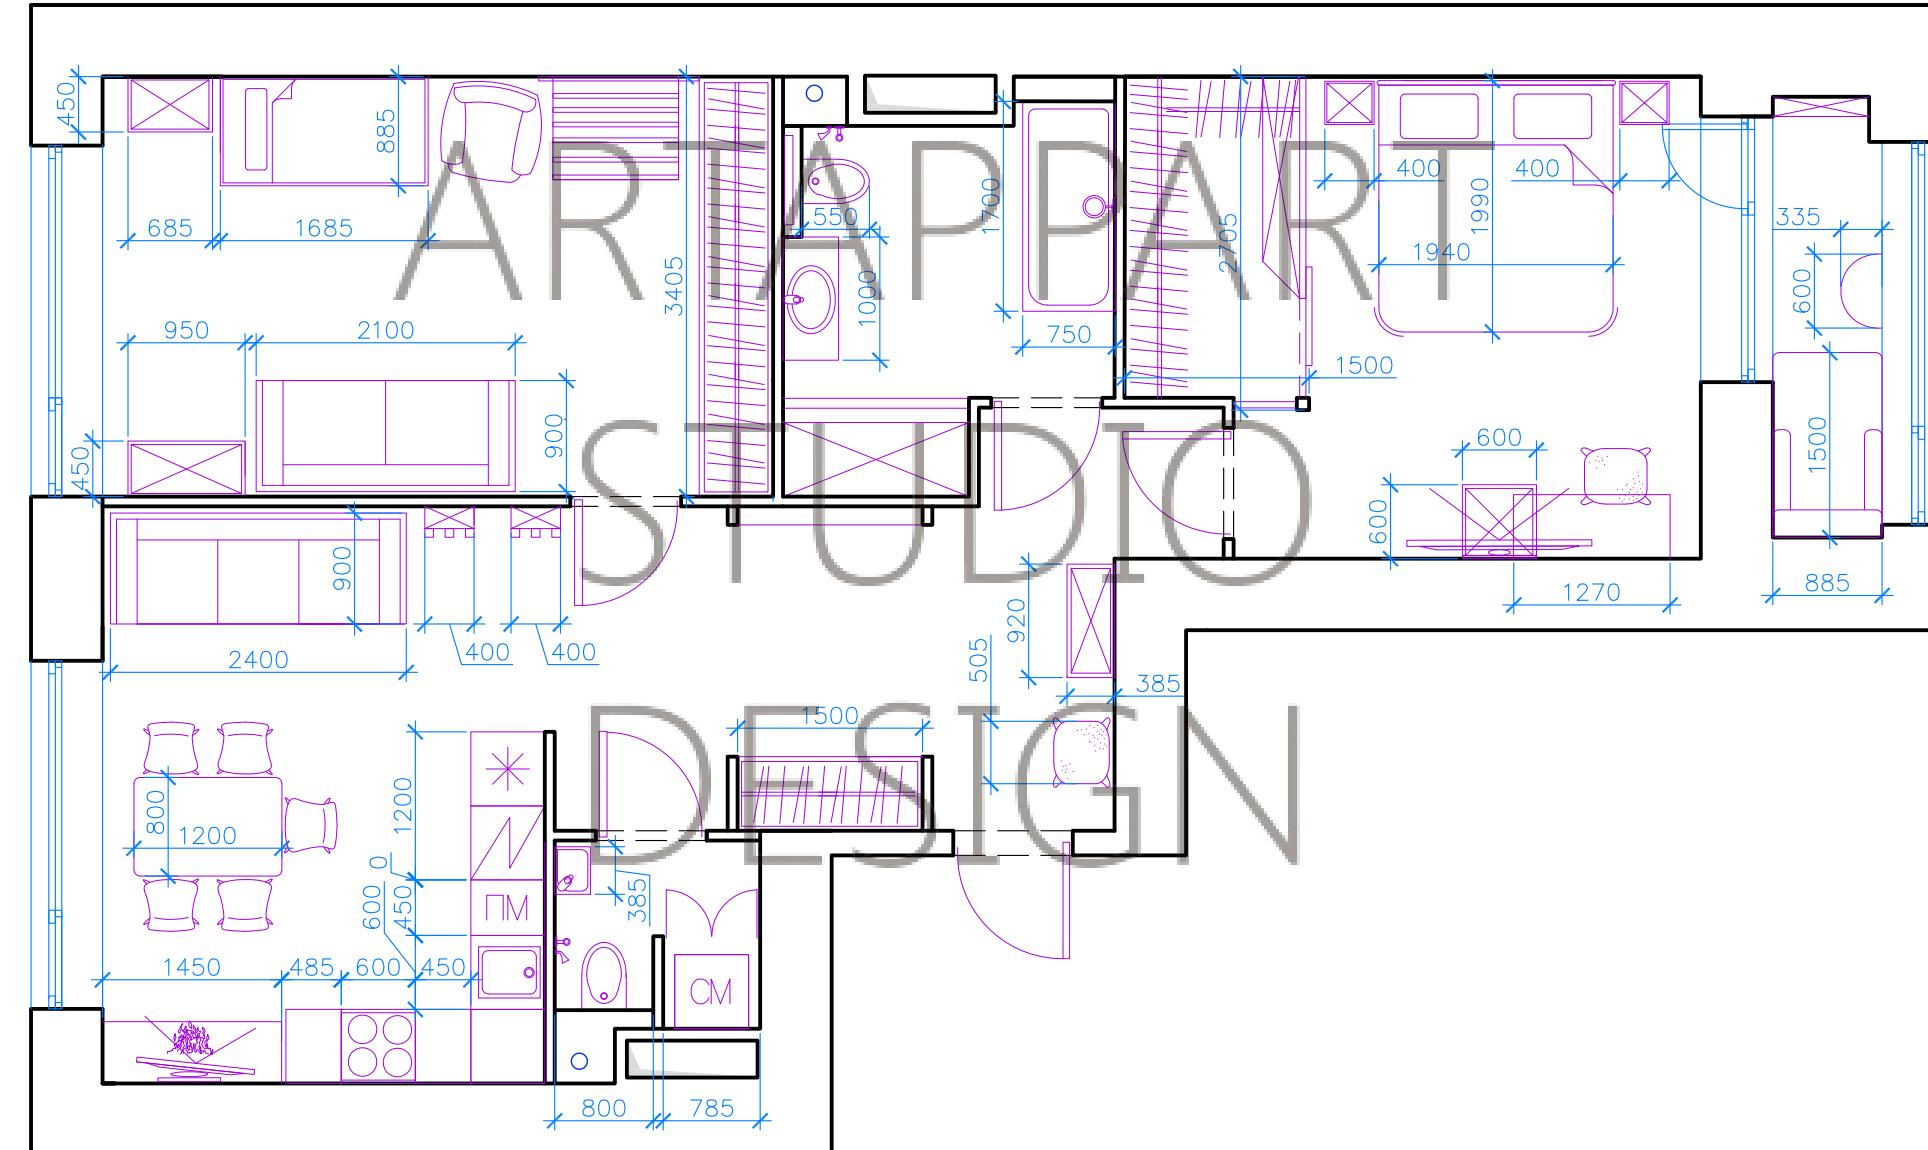


Инв. № подп.	Подп. и дата	Взам. инв.

Изм.	Кол. уч.	Листм	№ док.	Подп.	Дата	Разработка дизайн-проекта квартиры	Стадия	Листм	Листов
Заказчик					2019		P		
Разработ.					2019	Схема планировки с указанием основных размеров			
						M 1:60			



ARTAPPART  
DESIGN  
STUDIO

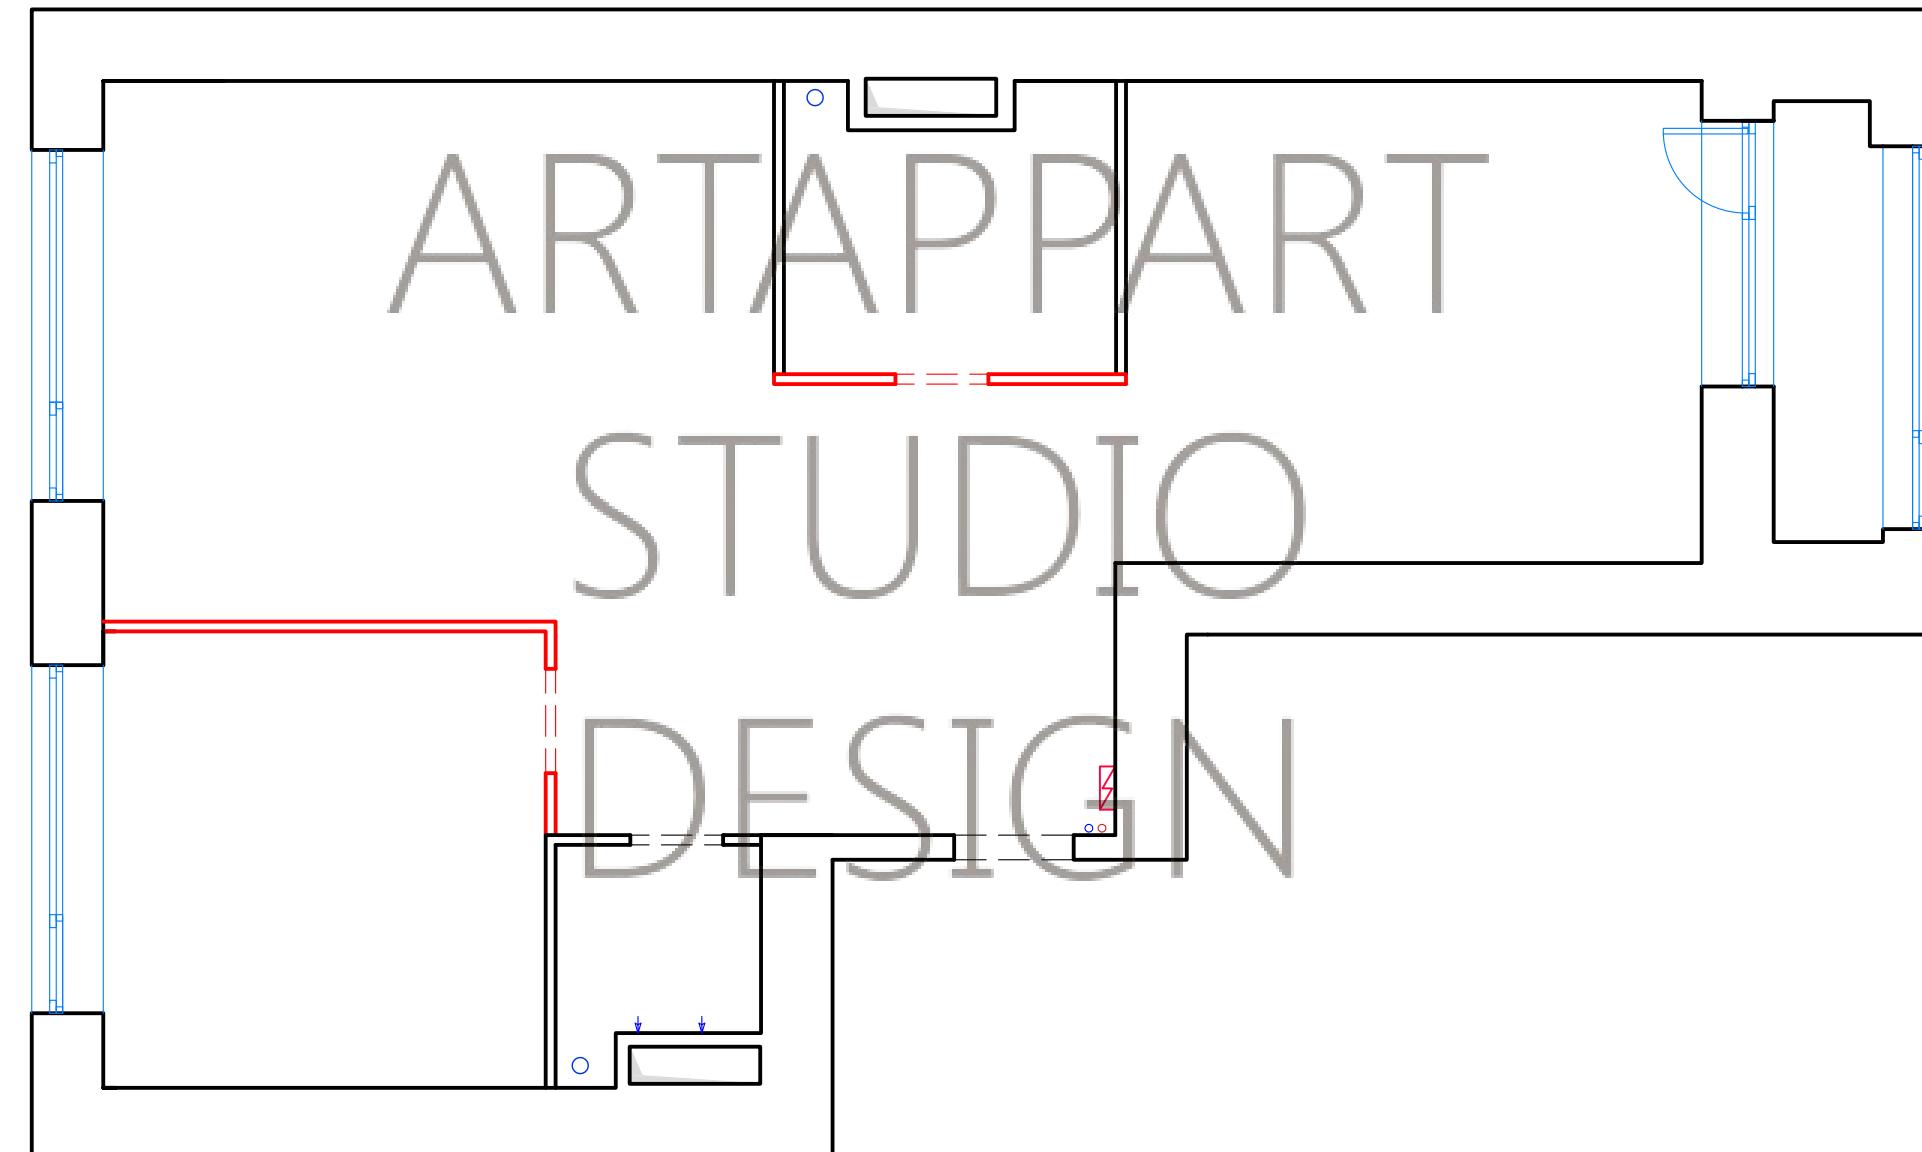

Инв. № подп.	Подп. и дата	Взам. инв.

Условные обозначения:  
===== — демонтируемые  
 перегородки

Изм.	Кол. уч.	Листм	№ док.	Подп.	Дата	Разработка дизайн-проекта квартиры	Стадия	Листм	Листов
Заказчик					2019		P		
Разработ.					2019	План демонтажа	M 1:60		



ARTAPPART  
DESIGN  
STUDIO

### Примечание:

Все возводимые перегородки выполнить из пазогребневых плинтусов толщина 80 мм, если не указано иное.

полки ГКЛ с подсветкой  
(предусмотреть пазы для установки светофильтров)

возведение опоры для последующей установки гардеробной, уточнить необходимость возведения перегородок для удешевления конструкции

A technical drawing of a rectangular frame. The outer dimensions are 200 units wide and 150 units high. A central rectangular opening is 80 units wide and 80 units high. The drawing uses blue lines on a white background with black text and arrows indicating dimensions.

размер наши тв приведен  
с учетом тв с диагональ  
50 дюймов

A technical drawing of a rectangular frame. The overall width is 1275, and the overall height is 85. The top horizontal dimension is 800, and the bottom horizontal dimension is 225. The left vertical dimension is 350, and the right vertical dimension is 400. The bottom-left corner of the frame is labeled 1000. A diagonal line is drawn from the top-left corner to the bottom-right corner, with a dimension of 50 indicated along this line. The drawing is labeled 1-1 at the bottom center.

размер наши для биокамина  
сверить с ТЗ для биотопки  
от производителя, произвести  
теплоизоляцию с применением  
материалов вермикулит или супериз  
или минерит

короб ГКЛ возводится  
в уровень с вент. шахтой,  
предусмотреть ревизионные  
люки и установку фильтров грубой  
очистки воды

Высота инсталляции – см. развернутый вкладыш по глубине короба максимально "прижать" к стене

высота инсталляции—см. развертки по глубине короб максимально "прижать" к стене


### Условные обозначения:

 – Возводимые перегородки

### Примечание:

1. Все существующие проемы выровнять по высоте до отмечки 2070 от УЧП (за уровень чистового пола принимается пол после стяжки и укладки напольного покрытия)
  2. Предусмотреть установку фильтров водоснабжения и ревизионных люков
  3. Предусмотреть устройство вентиляции в санузлах
  4. Разводка коммуникаций для систем кондиционирования выполнется предварительно, по проекту систем кондиционирования.

Изм.	Кол. уч.	Листм	№ док.	Подп.	Дата	Разработка дизайн-проекта квартиры	Стадия	Листм	Листмов
Заказчик				2019			P		
Разработ.				2019					
						План возводимых перегородок			
						M 1:60		ARTAPPART DESIGN STUDIO	

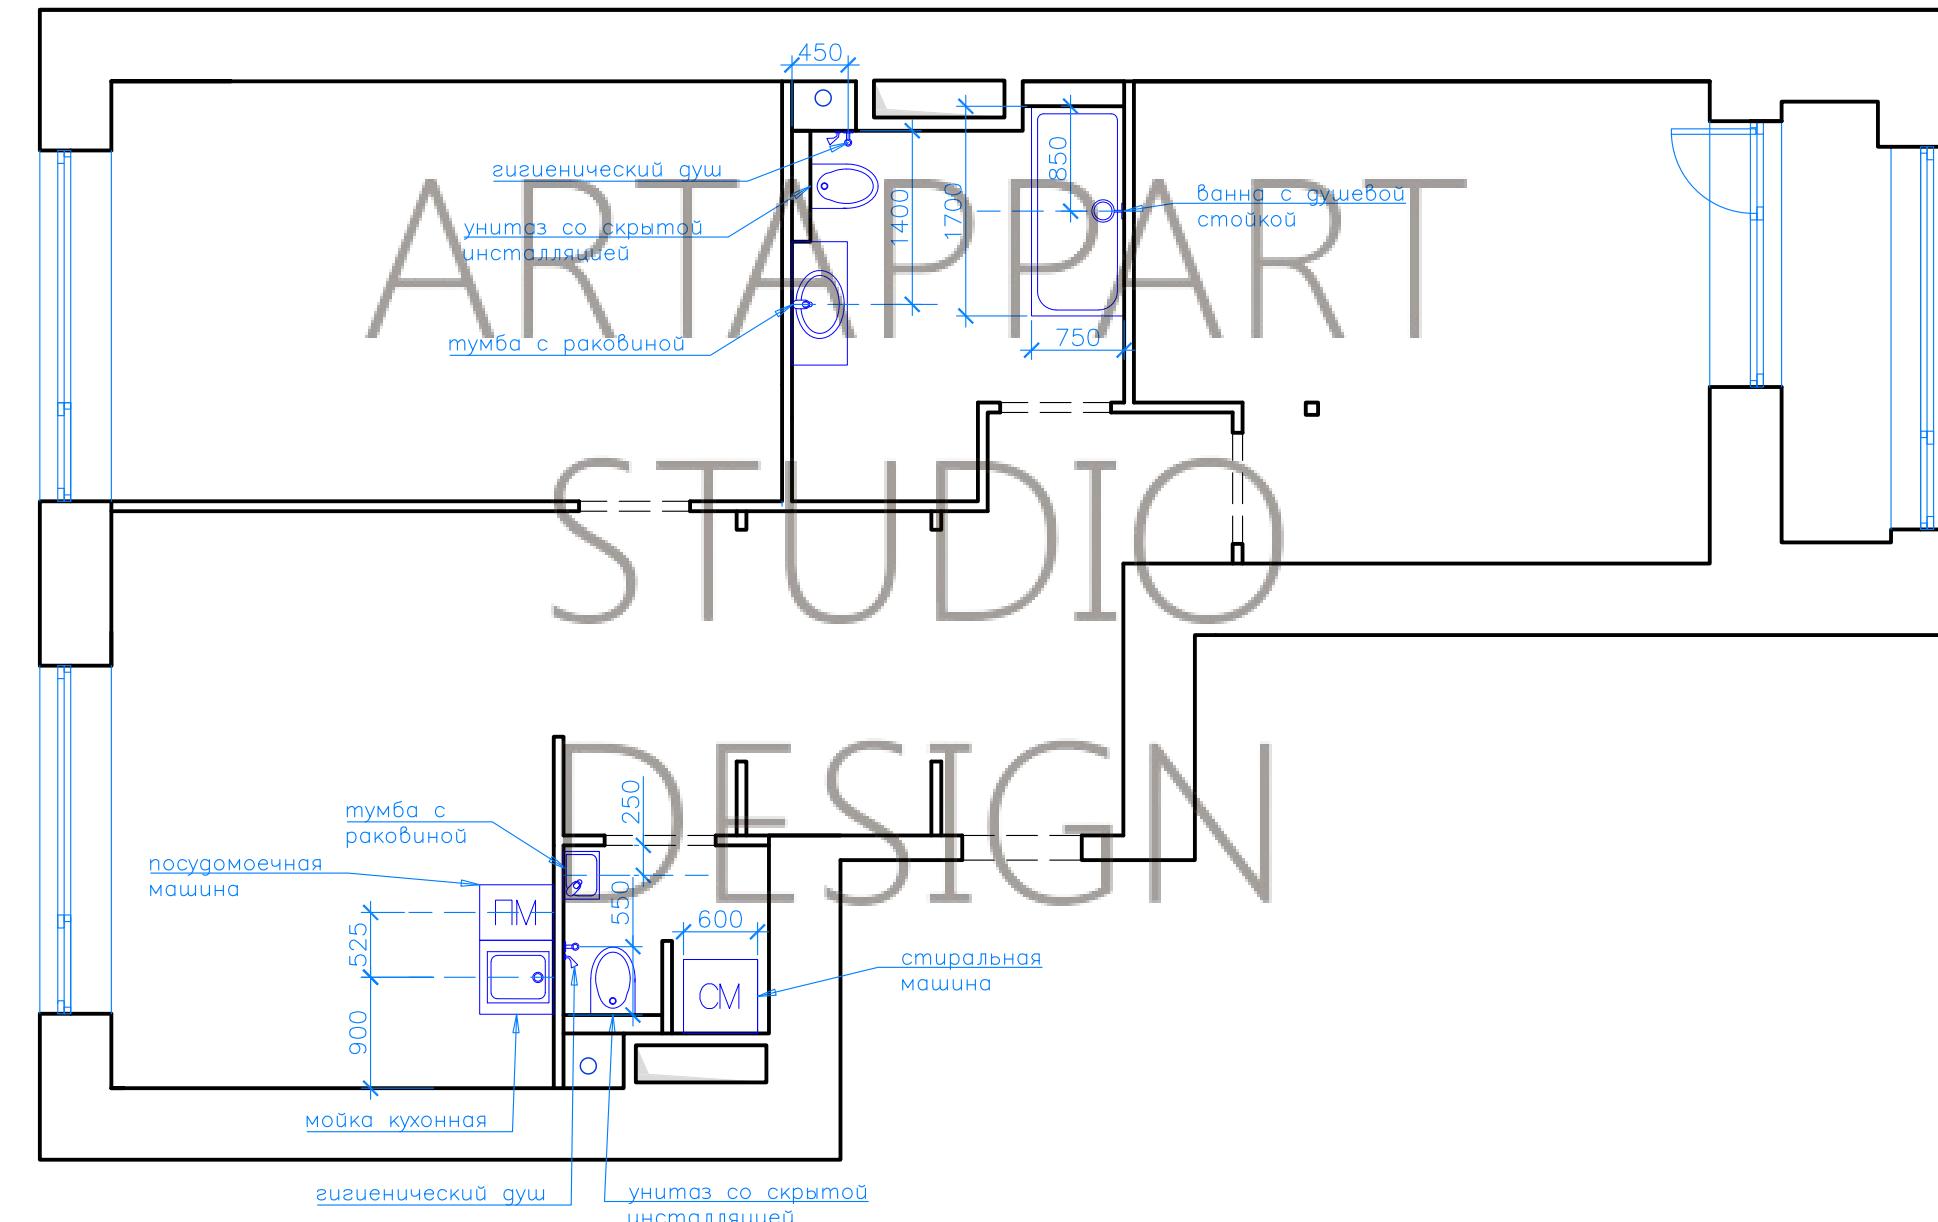


Изм.	Кол. уч.	Лист	№ док.	Подп.	Дата	Разработка дизайн-проекта квартиры	Стадия	Лист	Листов
Заказчик					2019		P		
Разработ.	.				2019				
						План расположения сан. технического оборудования			
						M 1:60			

ARTAPPART  
DESIGN  
STUDIO

Инв. № подп.	Подп. и дата	Взам. инв.

Согласовано

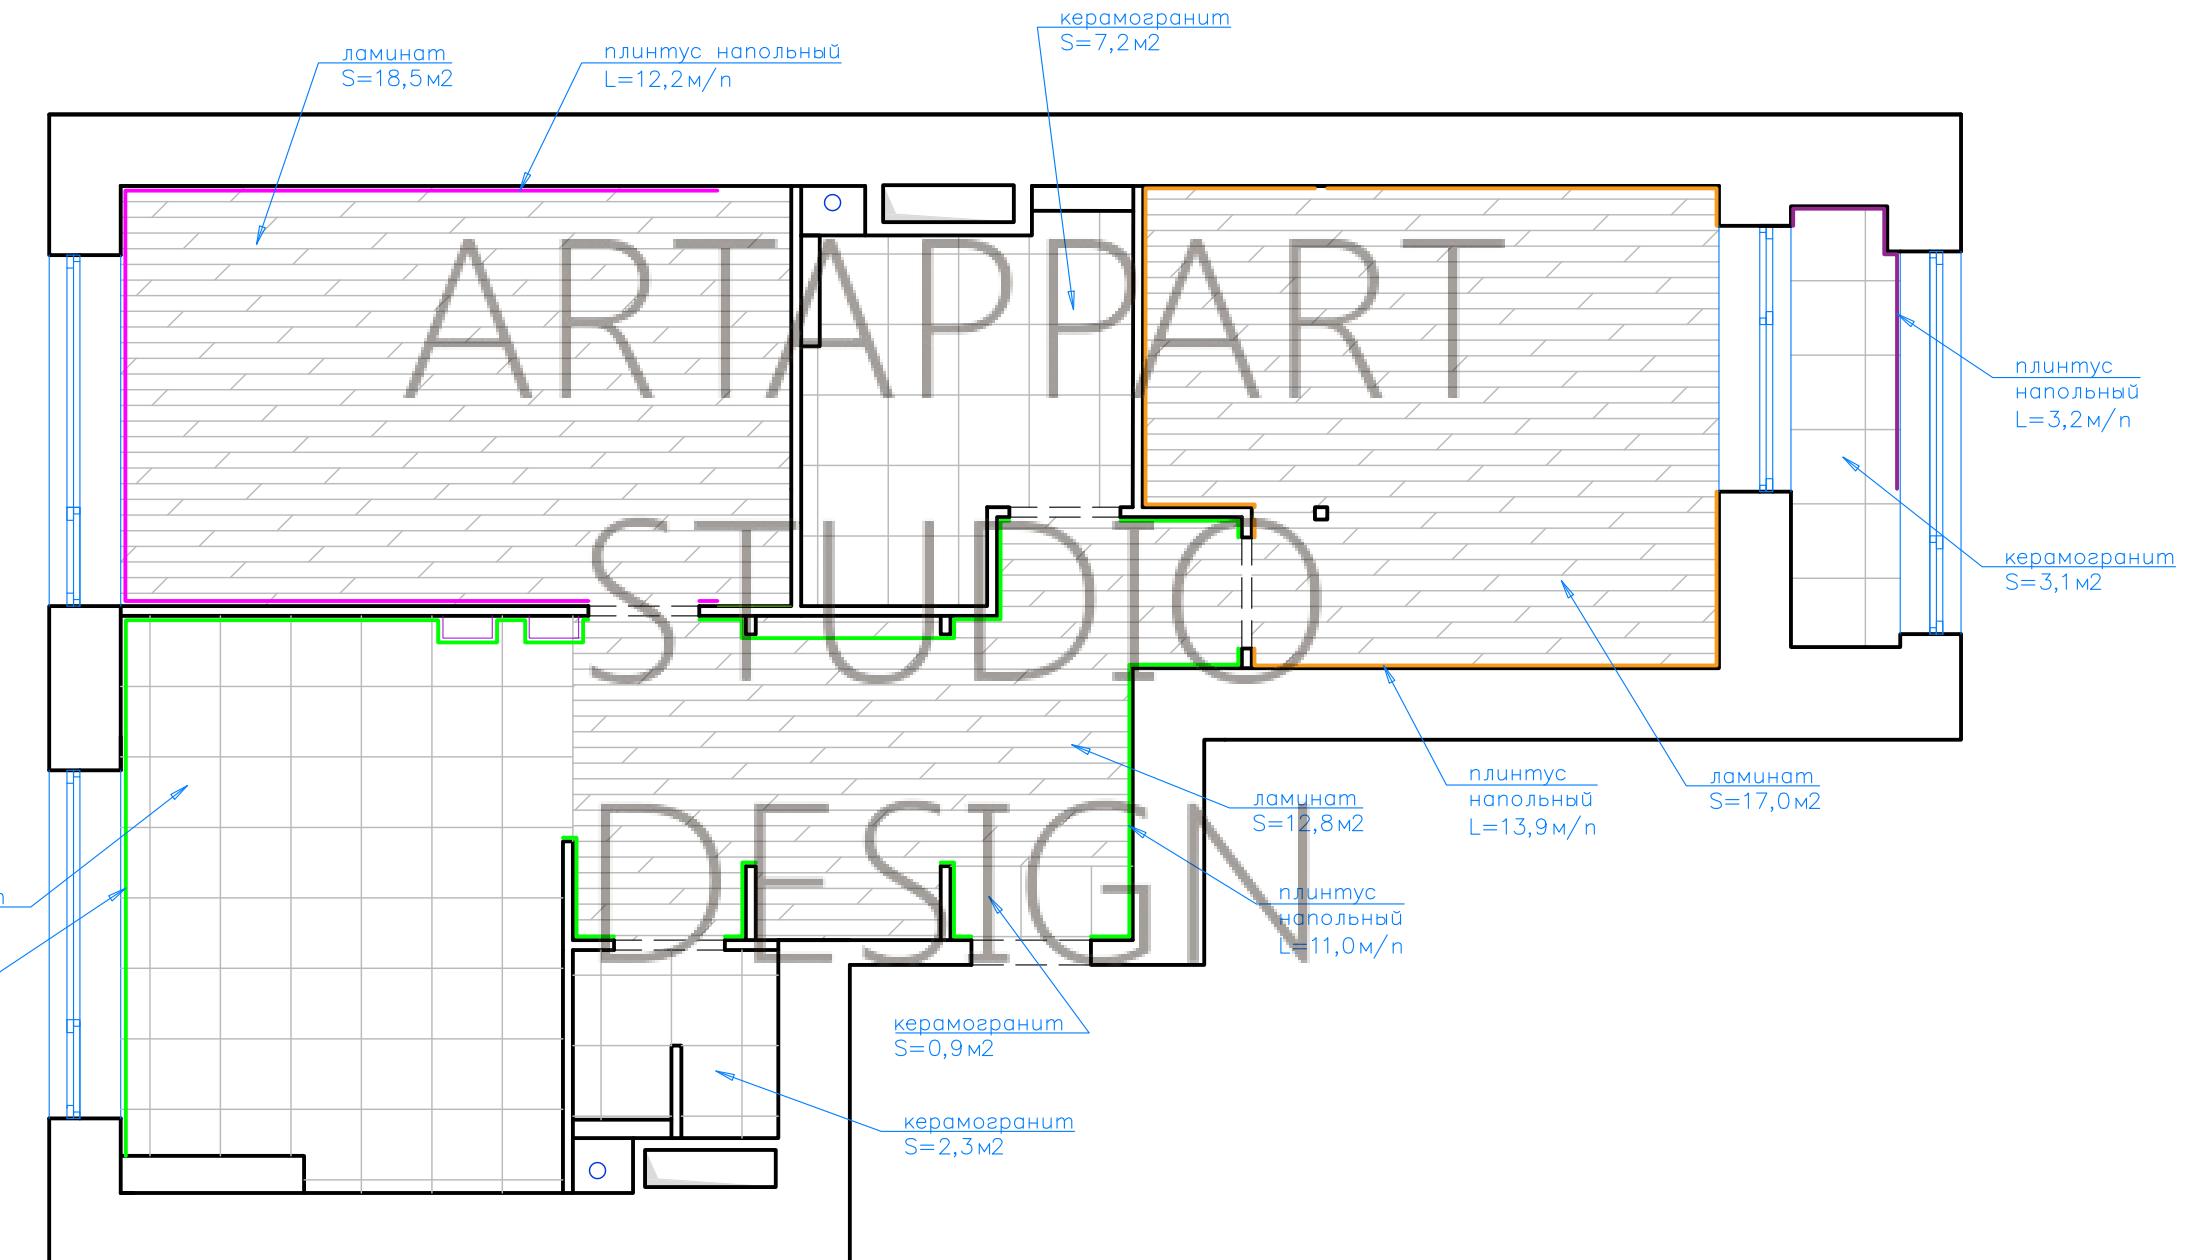


Примечание:

Площади покрытий даны без учета запаса.

Изм.	Кол. уч.	Листм	№ док.	Подп.	Дата	Разработка дизайн-проекта квартиры	Стадия	Листм	Листов
Заказчик					2019		P		
Разработ.					2019	План полов и напольных покрытий			
						M 1:60			



ARTAPPART  
DESIGN  
STUDIO

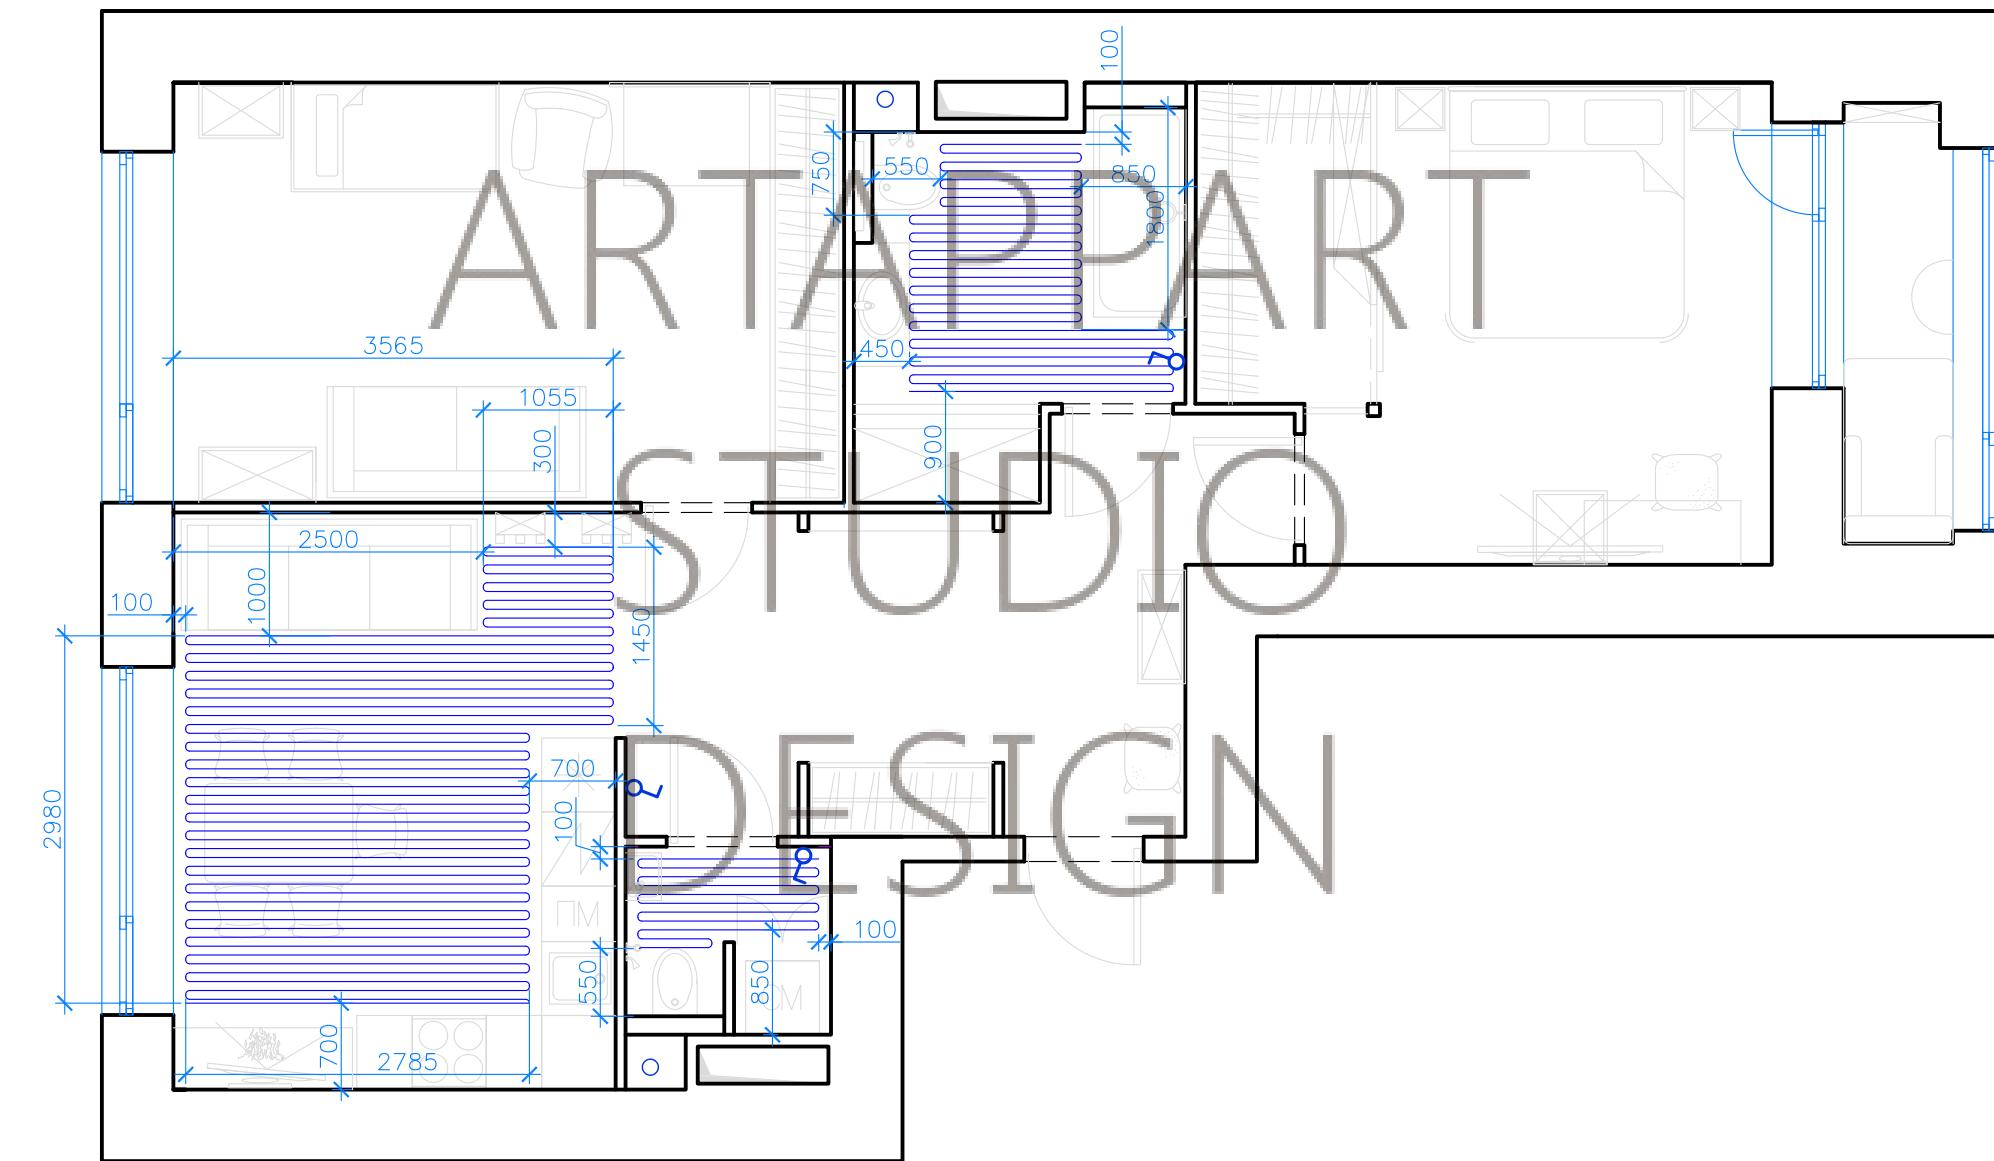


## Условные обозначения

- регулятор электрического теплого пола

### Примечание:

- Границы расположения теплого пола удалены от напольных элементов мебели, стен и прочих конструкций на 100мм, если не указано иное.
  - Терморегуляторы расположить на высоте 400мм на оснащении электроустановочного оборудования, если не указано иное.
  - Все терморегуляторы установить посередине простенка, либо на расстоянии 250 мм от угла, если не указано иное.

Изм.	Кол. уч.	Листм	№ док.	Подп.	Дата	Разработка дизайн-проекта квартиры	Стадия	Листм	Листмов
Заказчик				2019			P		
Разработ.				2019		План "теплых" полов М 1: 60			

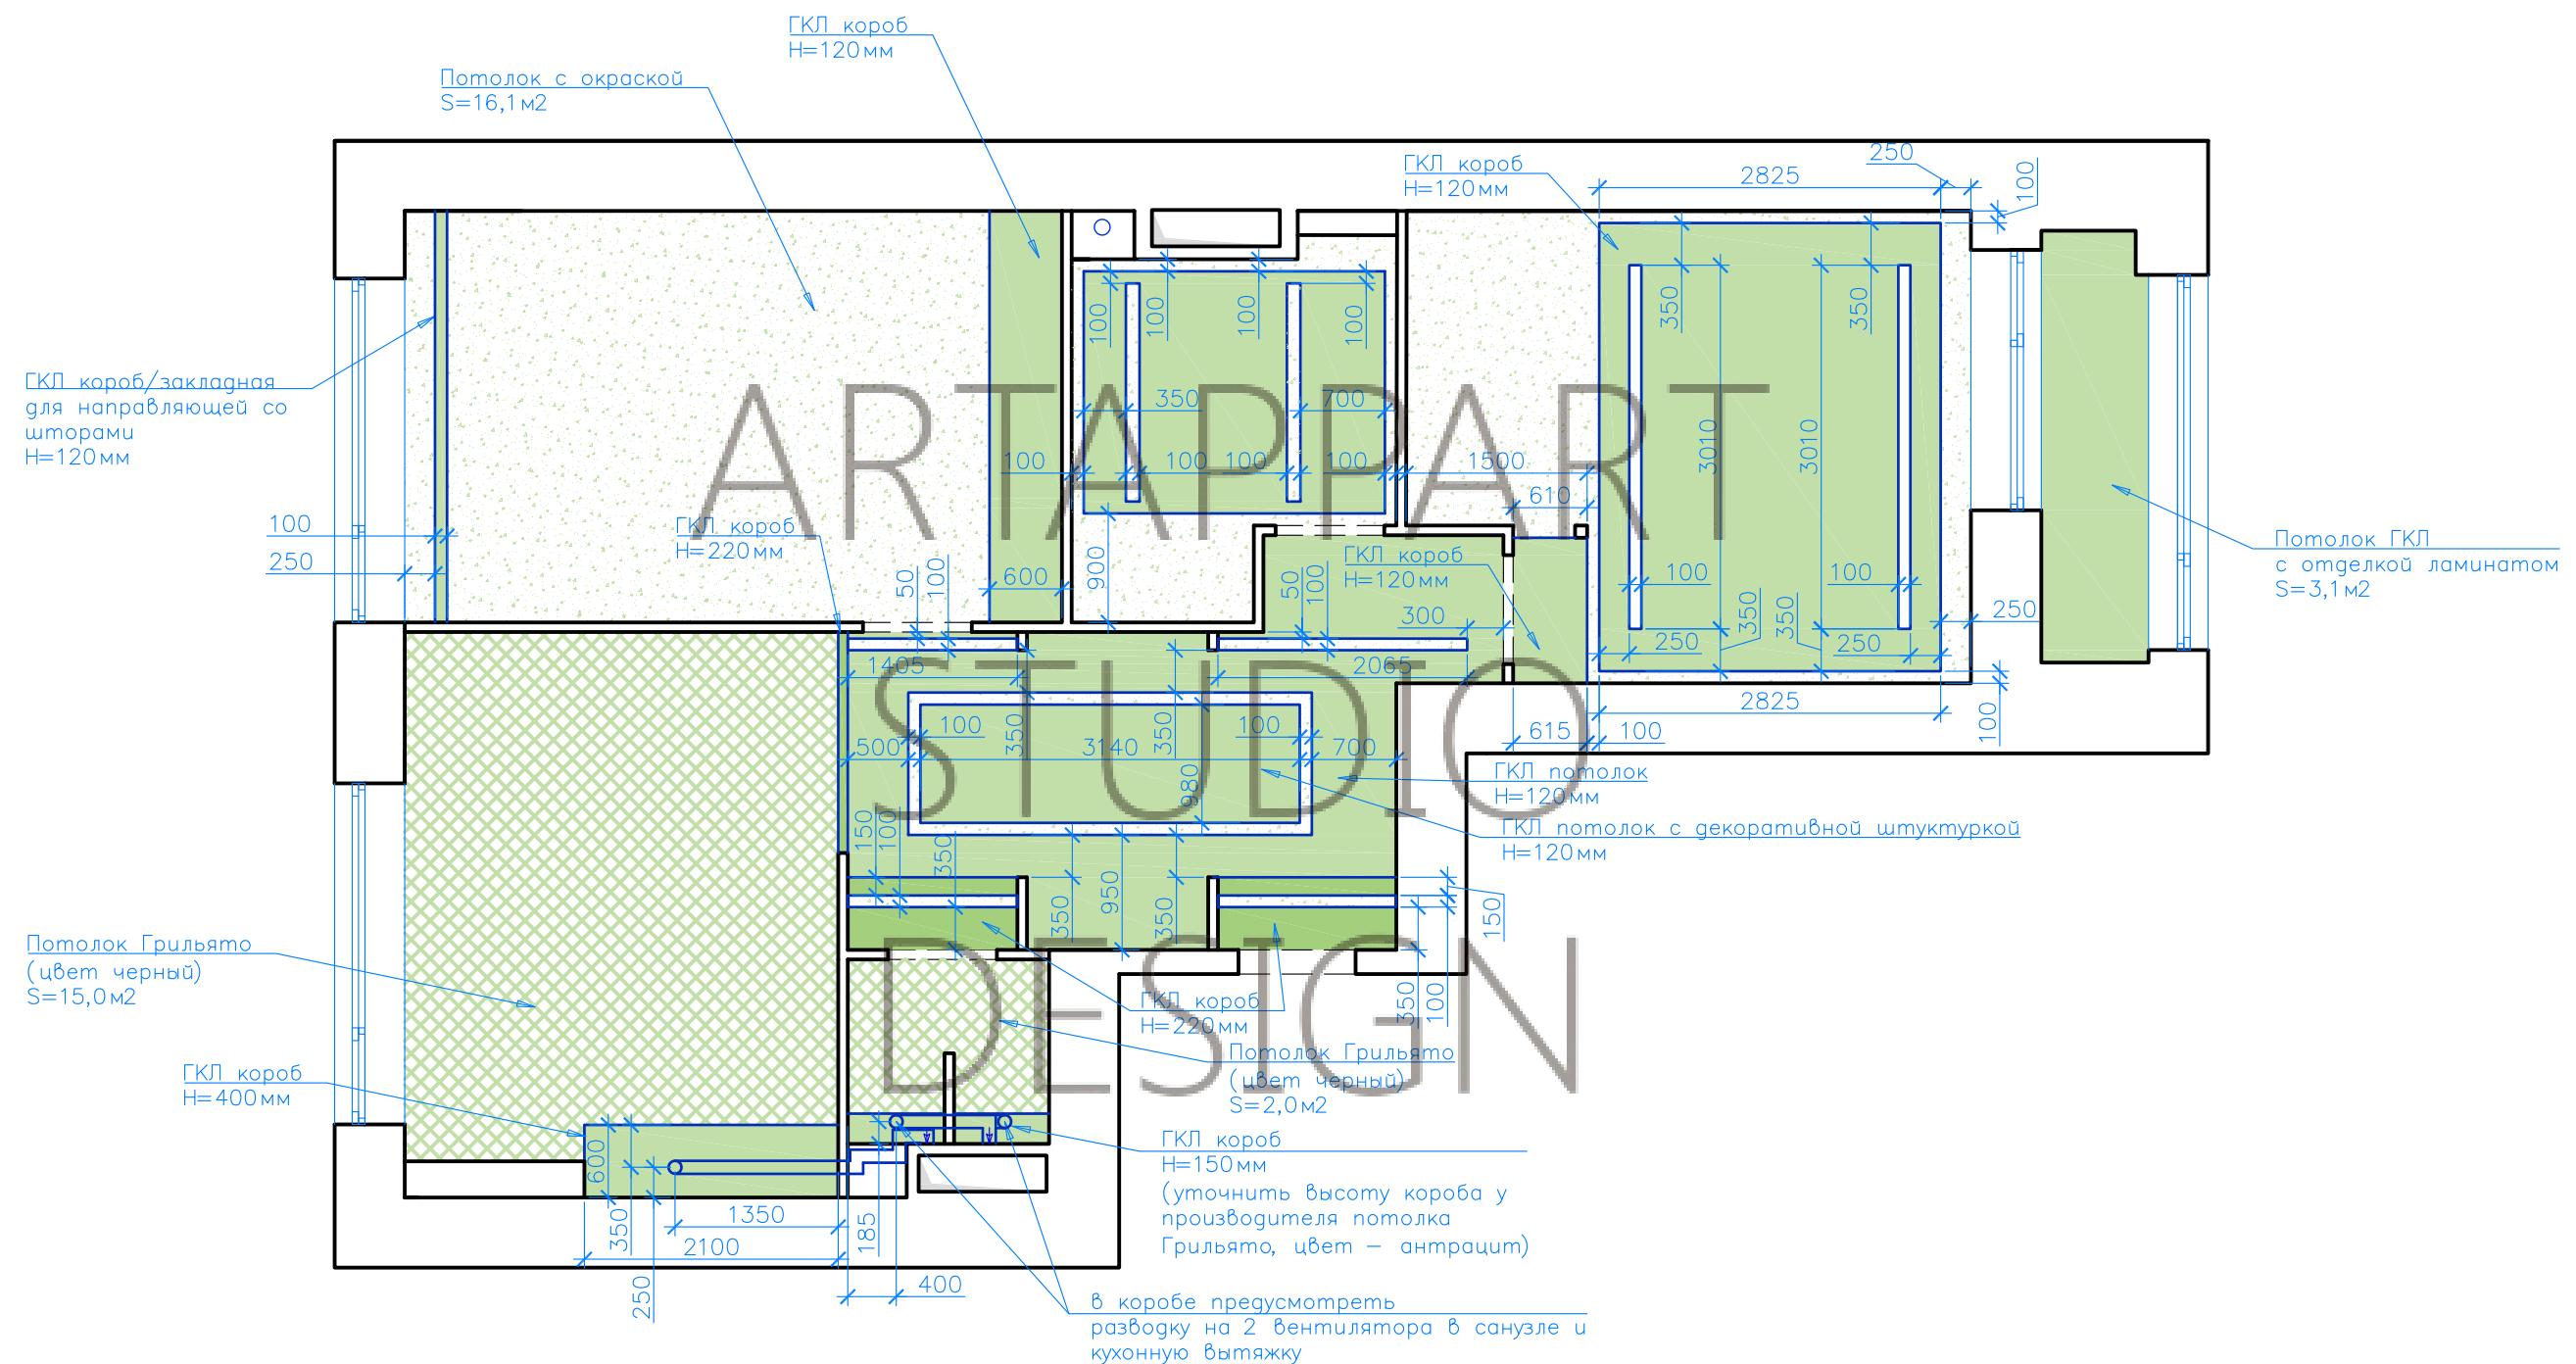

## Условные обозначения



– подшивной потолок П




— потолок с окраской



– потолок Грильят

### Примечание

1. Все покрытия белого цвета, если не указано иное
  2. За исходный уровень принят уровень потолка с учетом проведенных мероприятий по выравниванию и звукоизоляции
  3. Натяжные потолки монтируются на минимально возможном расстоянии от перекрытия, если не указано иное

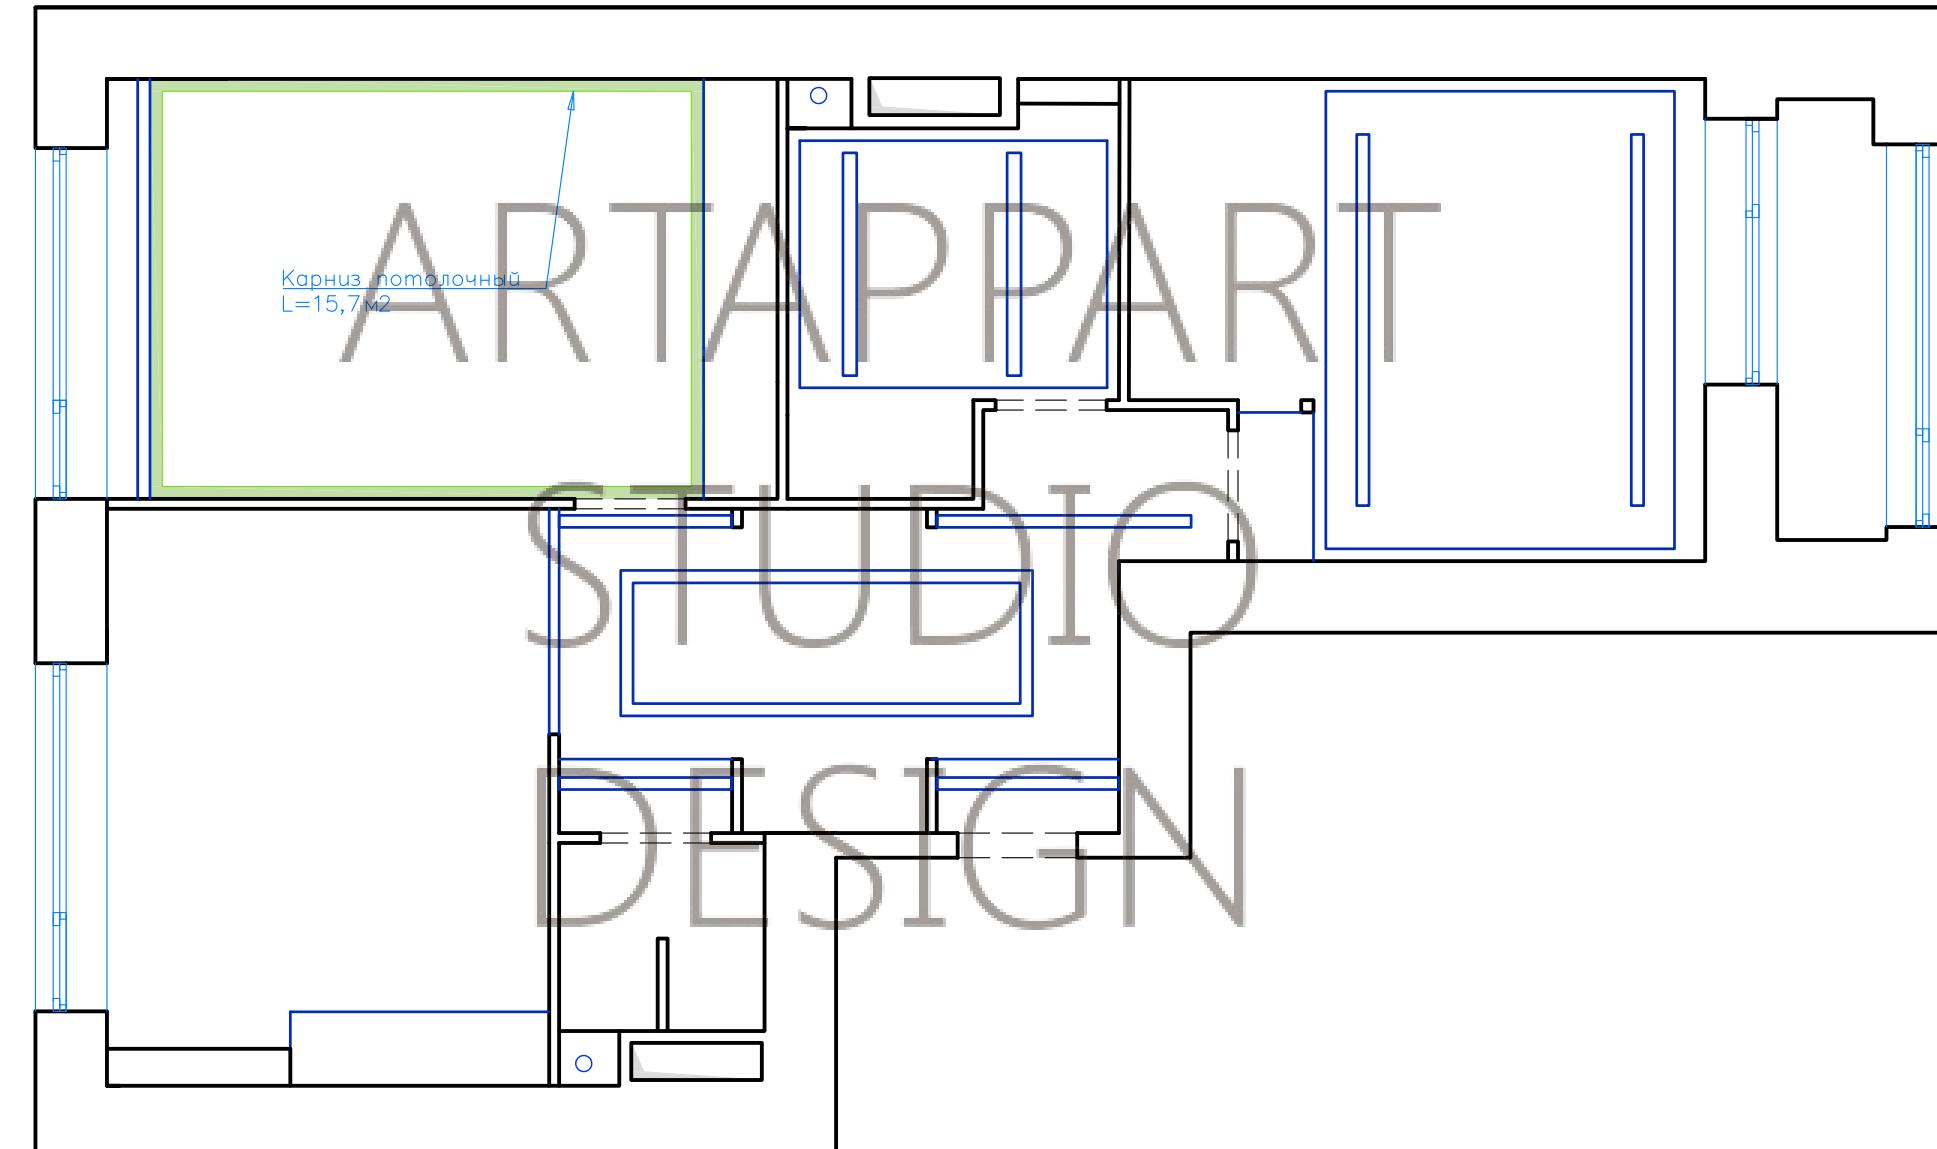

Условные обозначения:

— ППУ декор

Примечание: весь пенополиуретановый декор белого цвета, если не указано иное.

Изм.	Кол. уч.	Листм	№ док.	Подп.	Дата	Разработка дизайн-проекта квартиры	Стадия	Листм	Листов
Заказчик					2019		P		
Разработ.					2019	Схема расположения потолочного ППУ декора			
						M 1:60			



ARTAPPART  
DESIGN  
STUDIO

Согласовано

## Условные обозначени



~~✓~~ – nogβe



— бра/настен. светильни




$\mathcal{B}_1 \cup \mathcal{B}_2$




— cnom



⊕ ⊕ – встроенный помолочный стильник

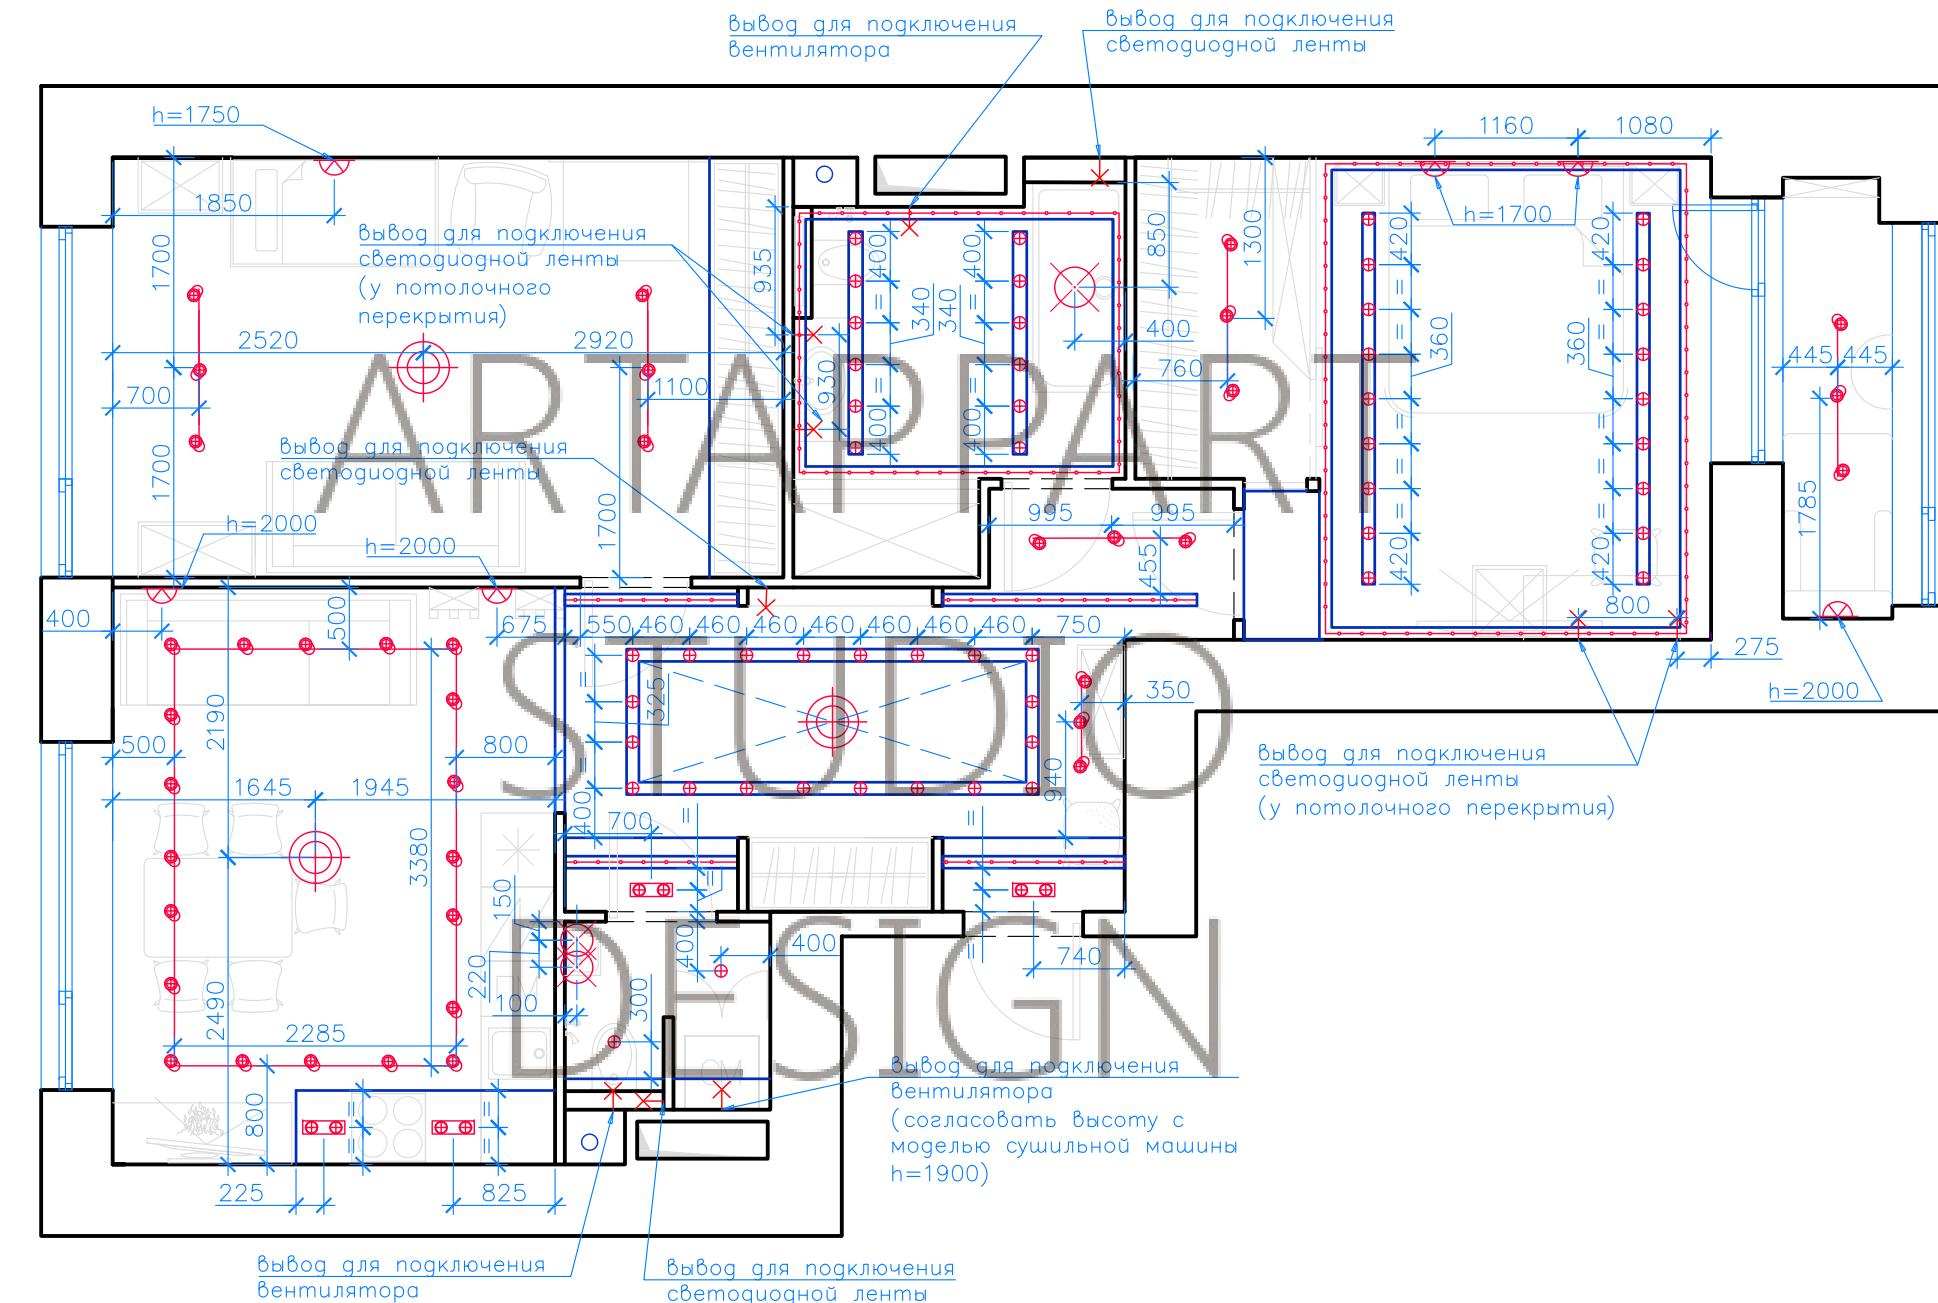

Изм.	Кол. уч.	Листм	№ док.	Погр.	Дата	Разработка дизайн-проекта квартиры	Стадия	Листм	Листов
Заказчик				2019					
Разработ				2019		План привязки освещительных приборов М 1: 60	P		

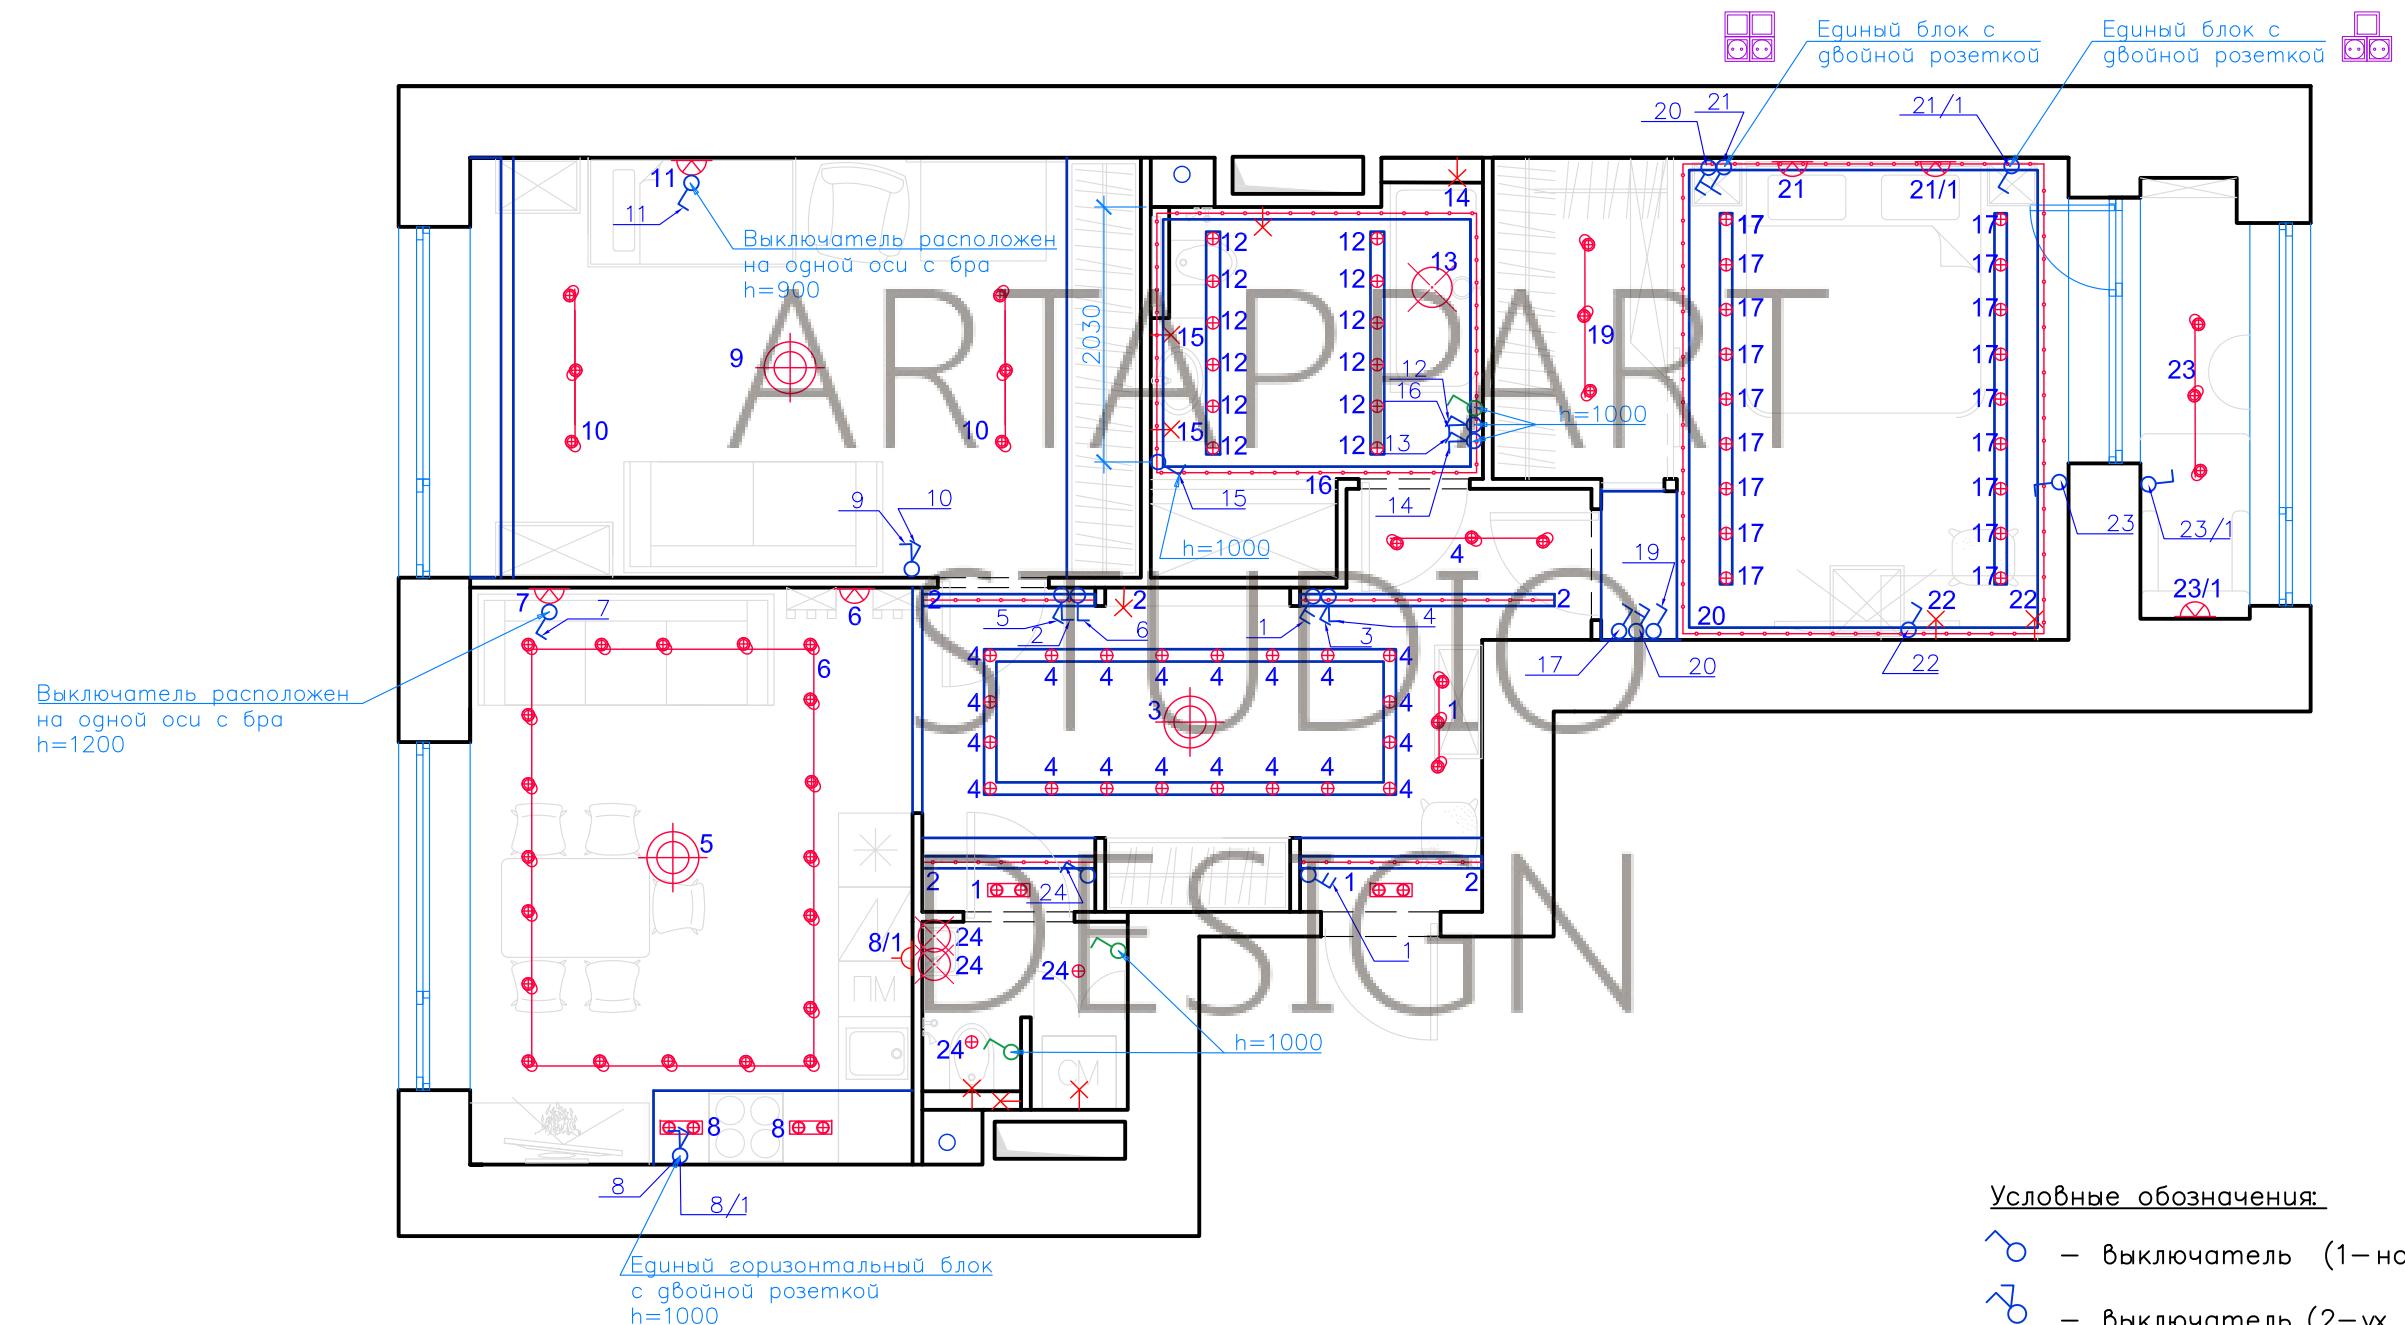

Условные обозначения:

- ↗ — выключатель (1-но клавишный)
- ↗ — выключатель (2-ух клавишный)
- ↘ — вкл. вентиляции
- ↖ — переключатель


Примечание:

1. Все выключатели установить посередине проема либо на расстоянии 250мм от угла, если не указано иное;
2. Высота до оси выключателя(—лей) 900мм от УЧП, если не указано иное;
3. Количество номеров групп светильников у выключателя определяет его тип: 1-но / 2-ух клавишный;
4. Привязки даны в мм от УЧП до осей приборов.
5. Для возможности редактирования рекомендуется оставлять выводы достаточной длины.

Изм.	Кол. уч.	Листм	№ док.	Подп.	Дата	Разработка дизайн-проекта квартиры	Стадия	Листм	Листов
Заказчик					2019				
Разработ.					2019				
						План разводки осветительных приборов на выключатели			
						M 1: 60			

Согласовано

Инв № подп Подп и дата Взам. инв

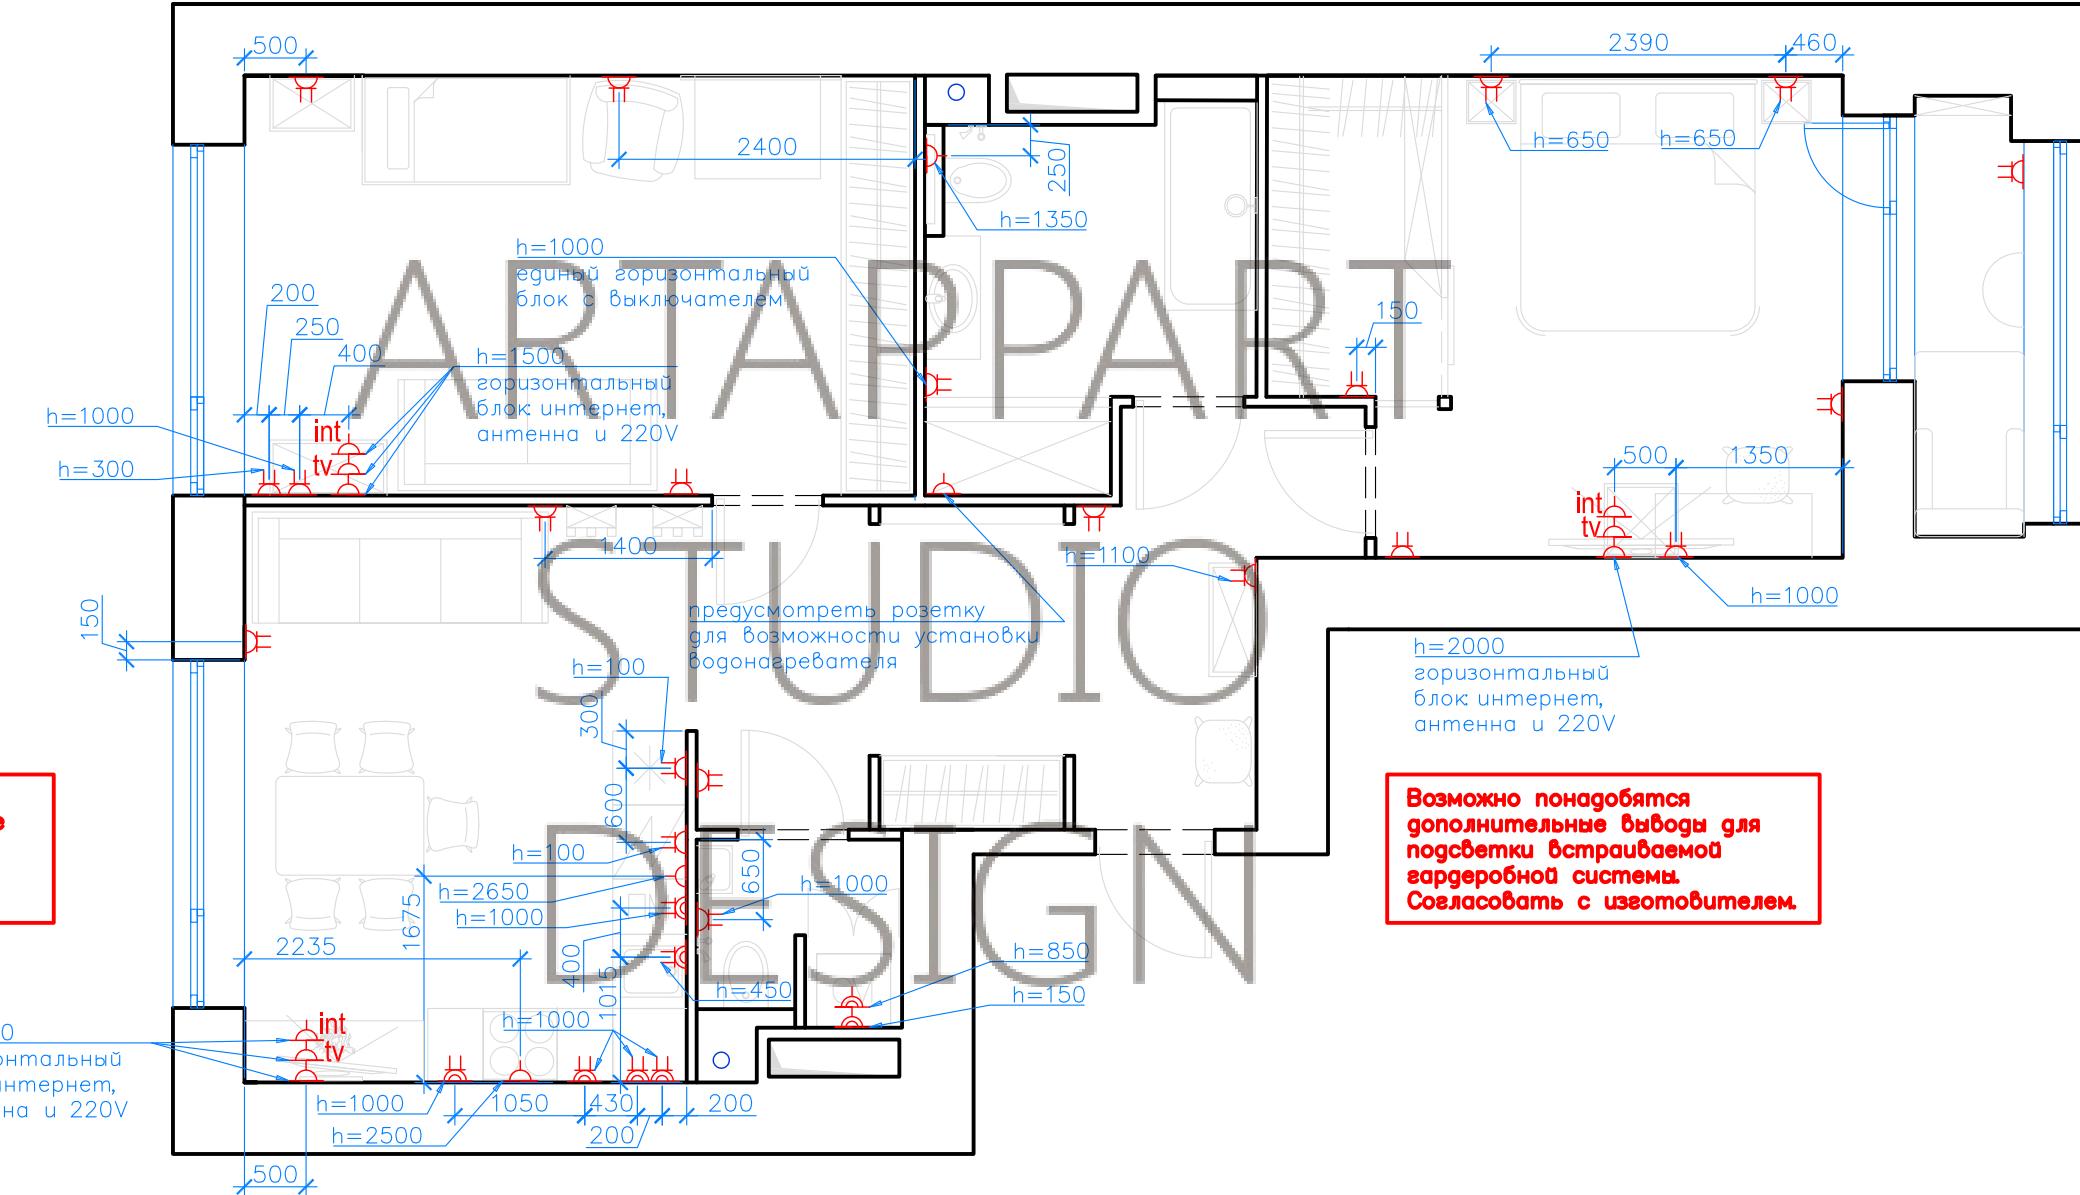

Условные обозначения:

- розетка с заземлением
- 2-я розетка с заземлением
- tv — телевизионная антenna И розетка
- int — интернет-розетка\*
- розетка с заземлением влагостойкая
- 2-я розетка с заземлением влагостойкая
- \* — эл. вывод


Примечание:

1. Все розетки, кроме обозначенных, установить на высоте 300 мм от УЧП;
2. Розетки располагать посередине просценка либо на расстоянии 250мм от угла, если привязки не указаны;
3. Привязки даны в мм от УЧП до осей приборов.
4. Для возможности редактирования рекомендуется оставлять выводы достаточной длины.

Изм.	Кол. уч.	Листм	№ док.	Подп.	Дата	Разработка дизайн-проекта квартиры	Стадия	Листм	Листов
Заказчик					2019				
Разработ.					2019				
						План электрики и электропроводов			
						M 1:60			




ARTAPPART  
DESIGN  
STUDIO


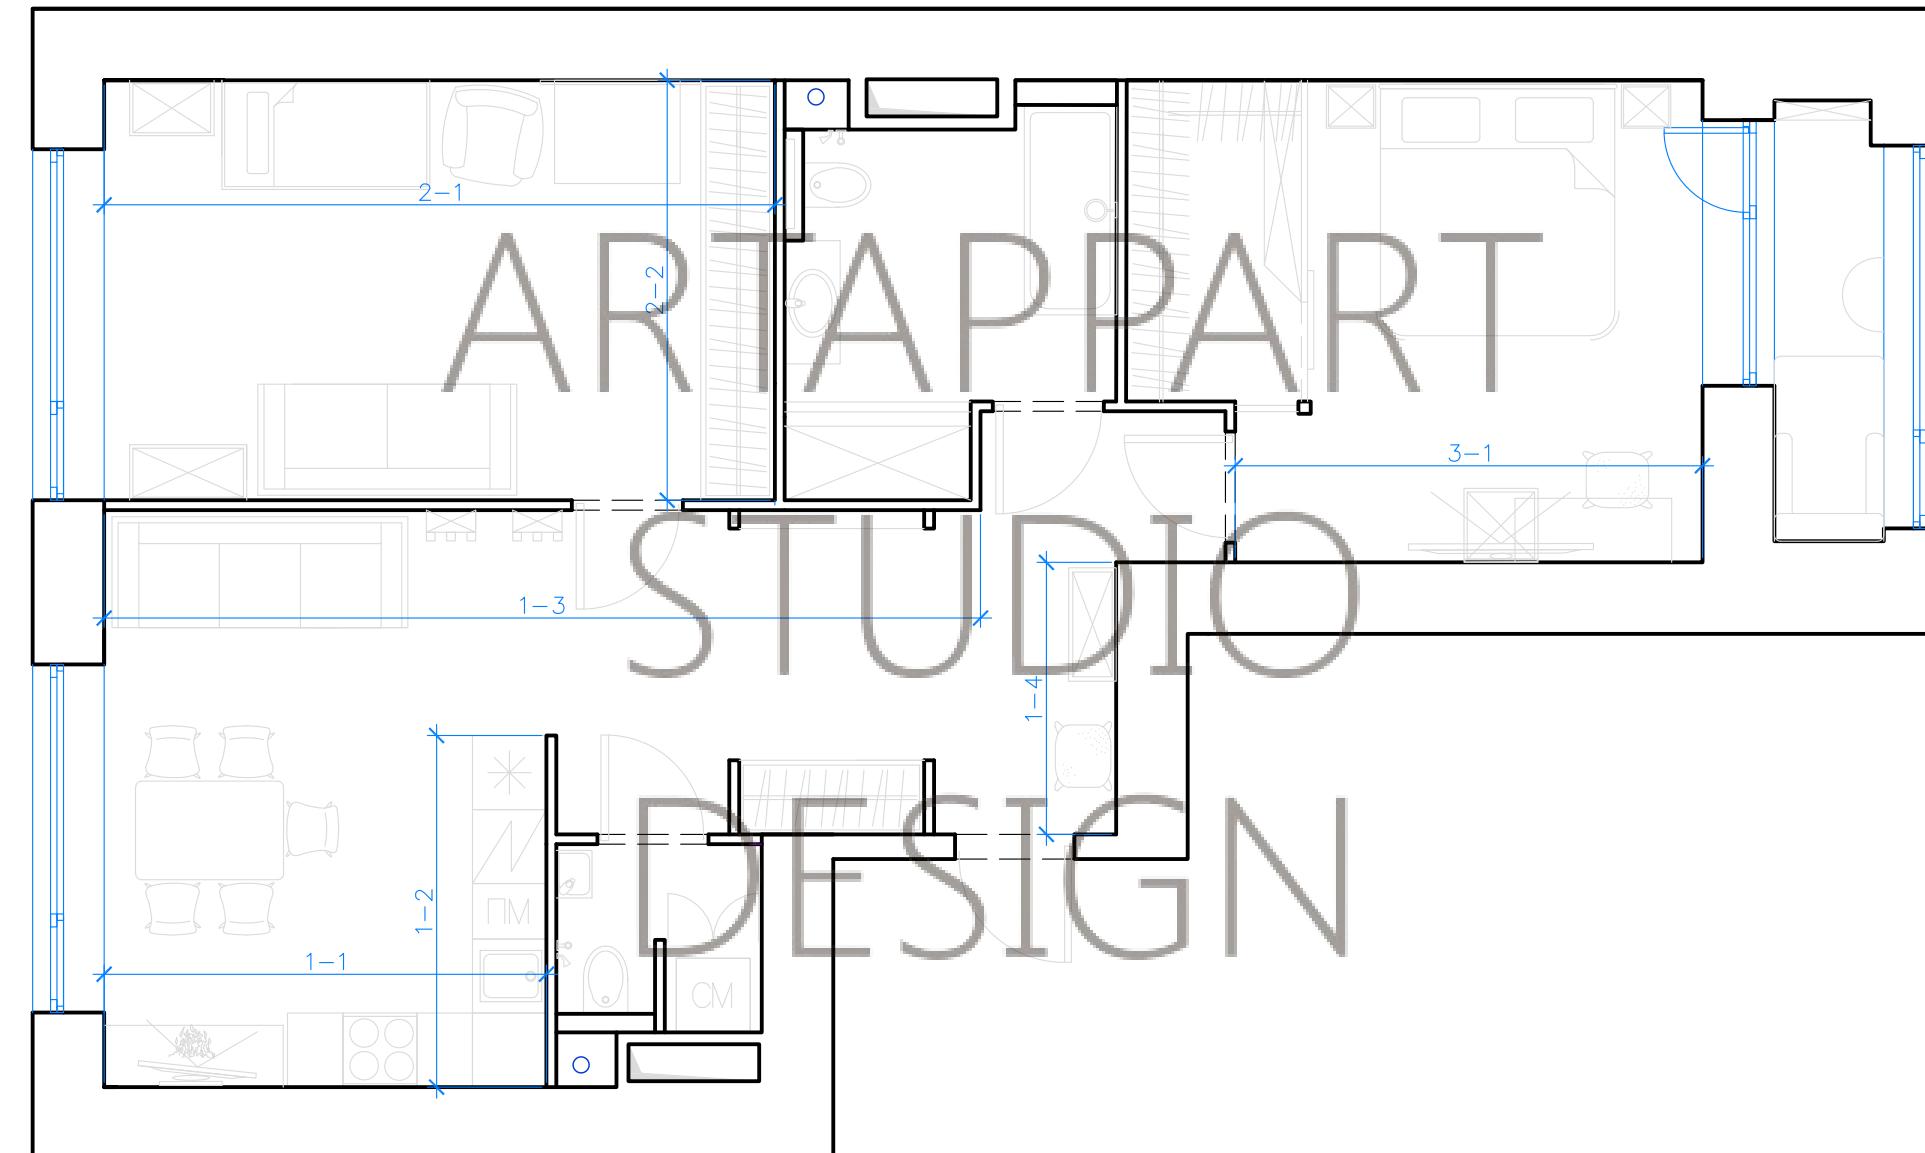


Согласовано

Инф. № подл.	Подп. и дата	Взам. инф.
--------------	--------------	------------

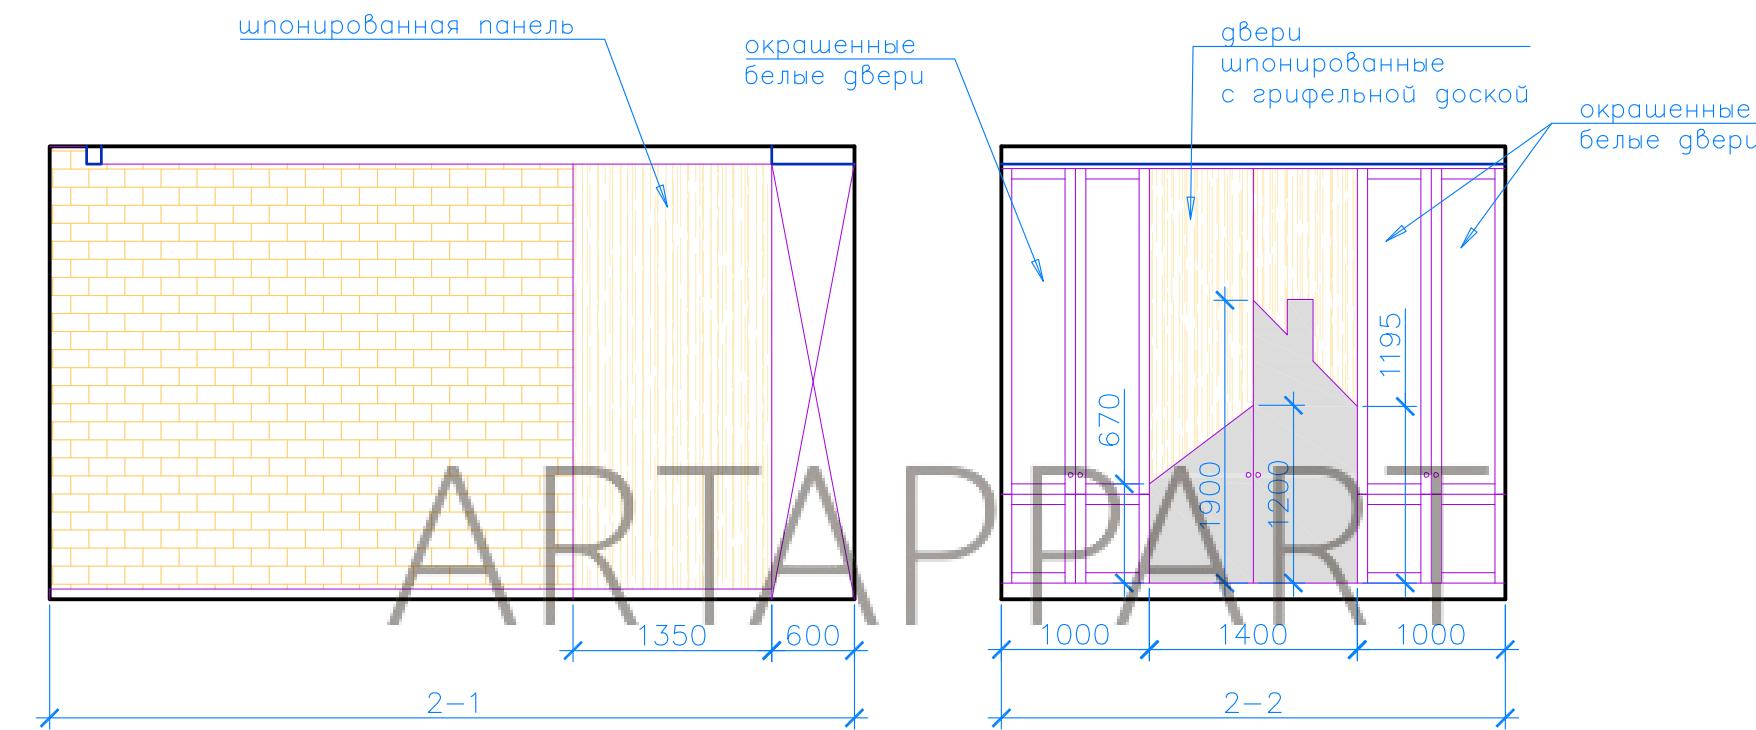

ARTAPPART  
STUDIO

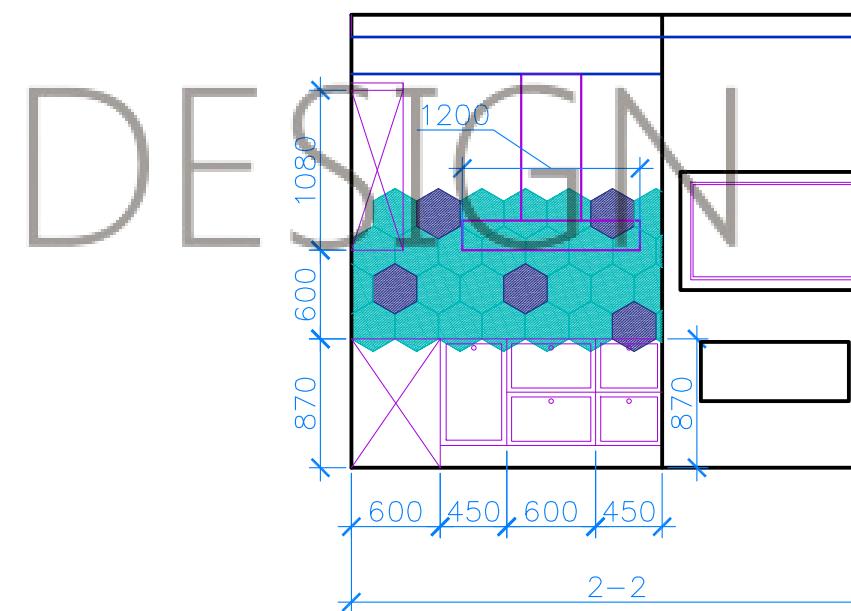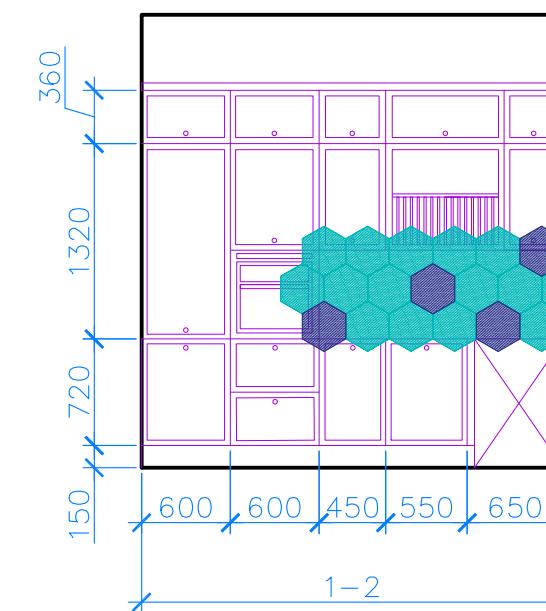


Плитка Azzuro Mare Esagona  
Плитка Giada Esagona

Инв. № подп.	Подп. и дата	Взам. инв.

Изм.	Кол. уч.	Листм	№ док.	Подп.	Дата	Разработка дизайн-проекта квартиры	Стадия	Листм	Листмов
Заказчик					2019				
Разработ.					2019				

Развертки по стенам  
М 1: 50

ARTAPPART  
DESIGN  
STUDIO

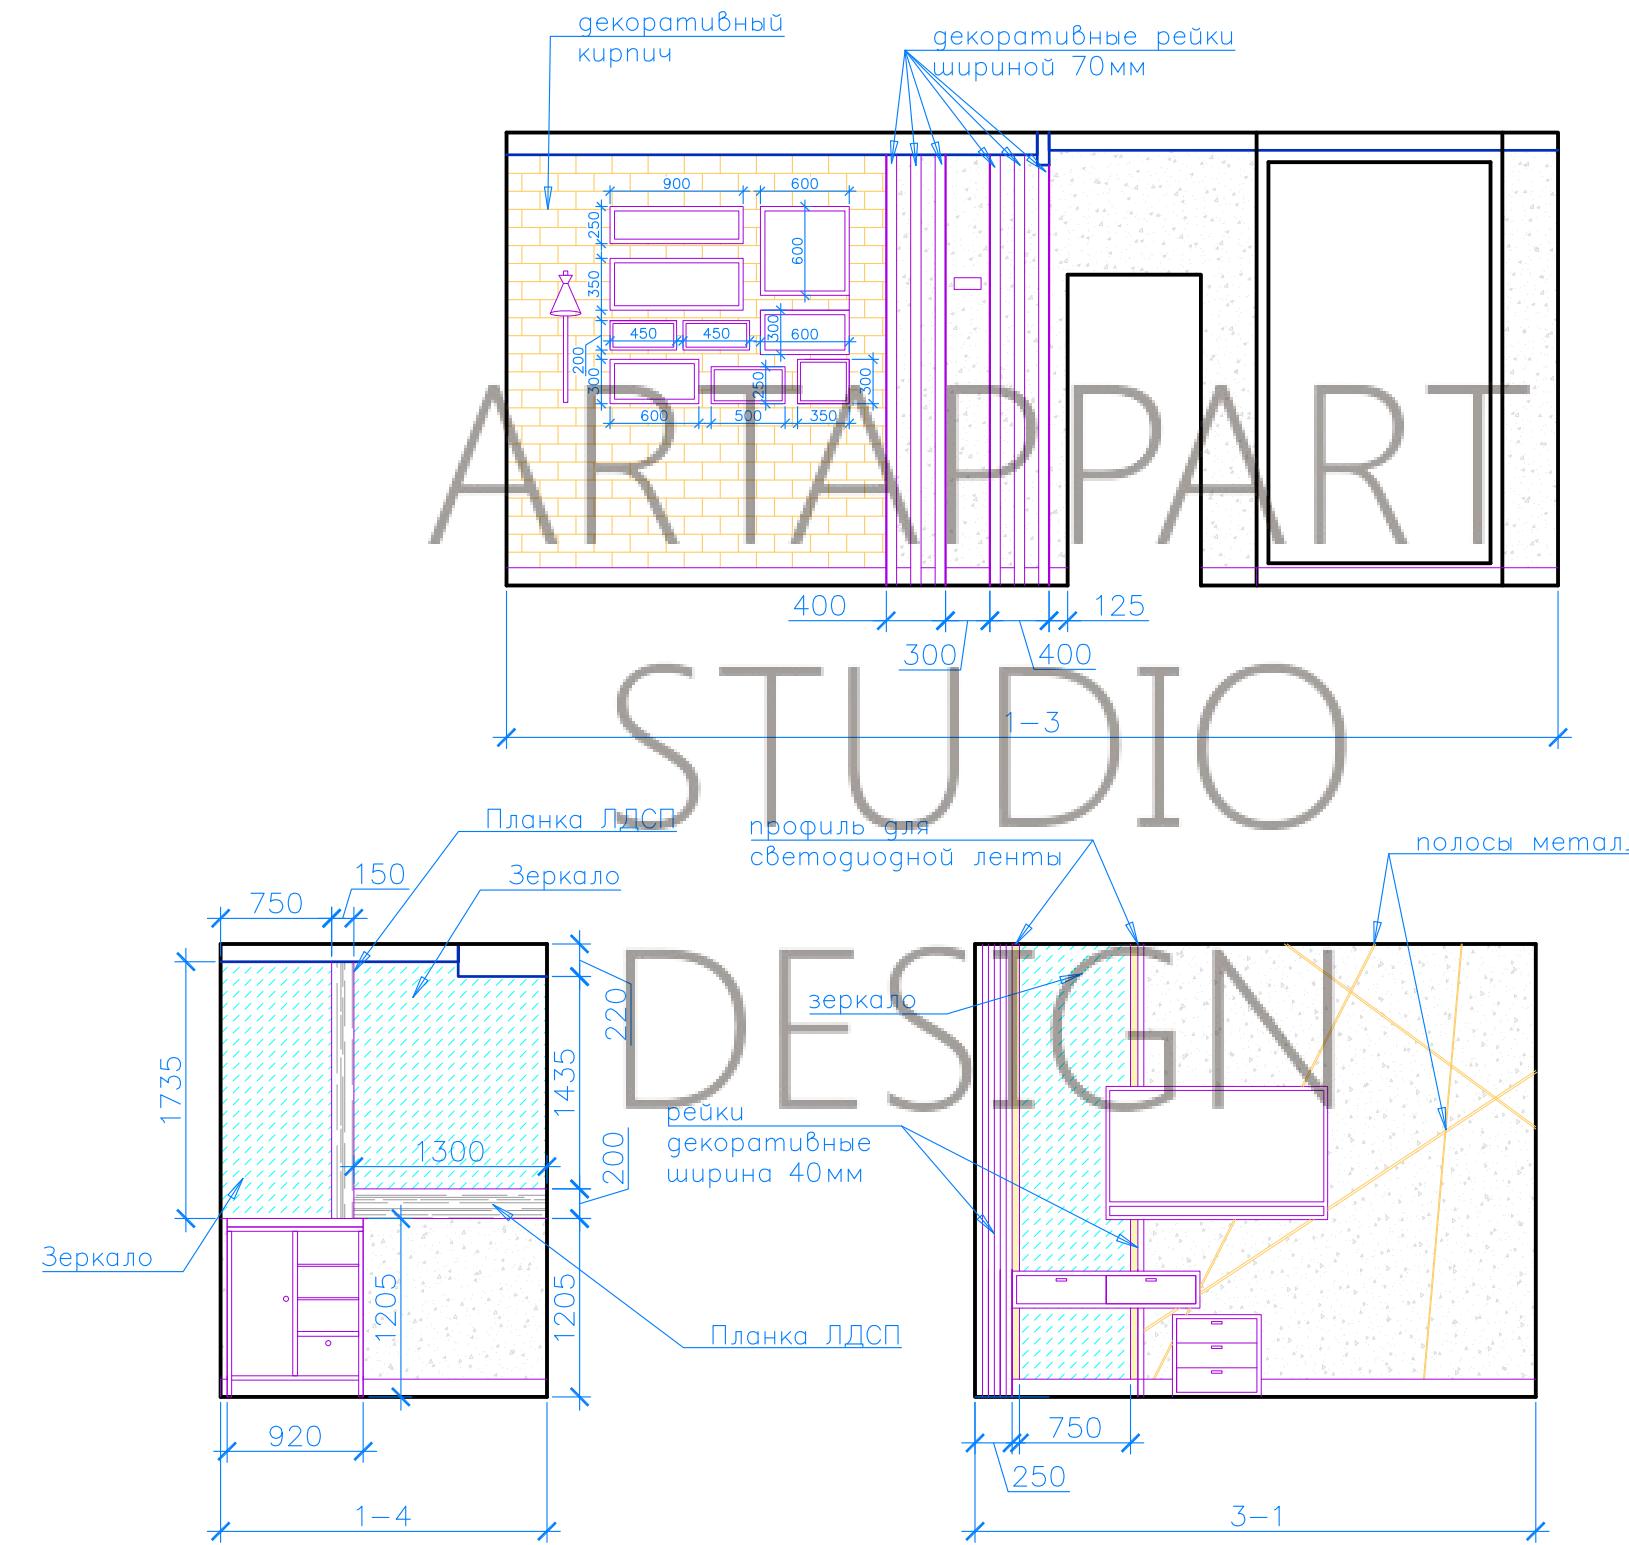

Инв. № подп.	Подп. и дата	Взам. инв.


Изм.	Кол. уч.	Листм	№ док.	Подп.	Дата	Разработка дизайн-проекта квартиры	Стадия	Листм	Листмов
Заказчик					2019		P		
Разработ.					2019				

Развертки по стенам  
М 1: 50

ARTAPPART  
DESIGN  
STUDIO

Инв. № подп.	Подп. и дата	Взам. инв.



Согласовано

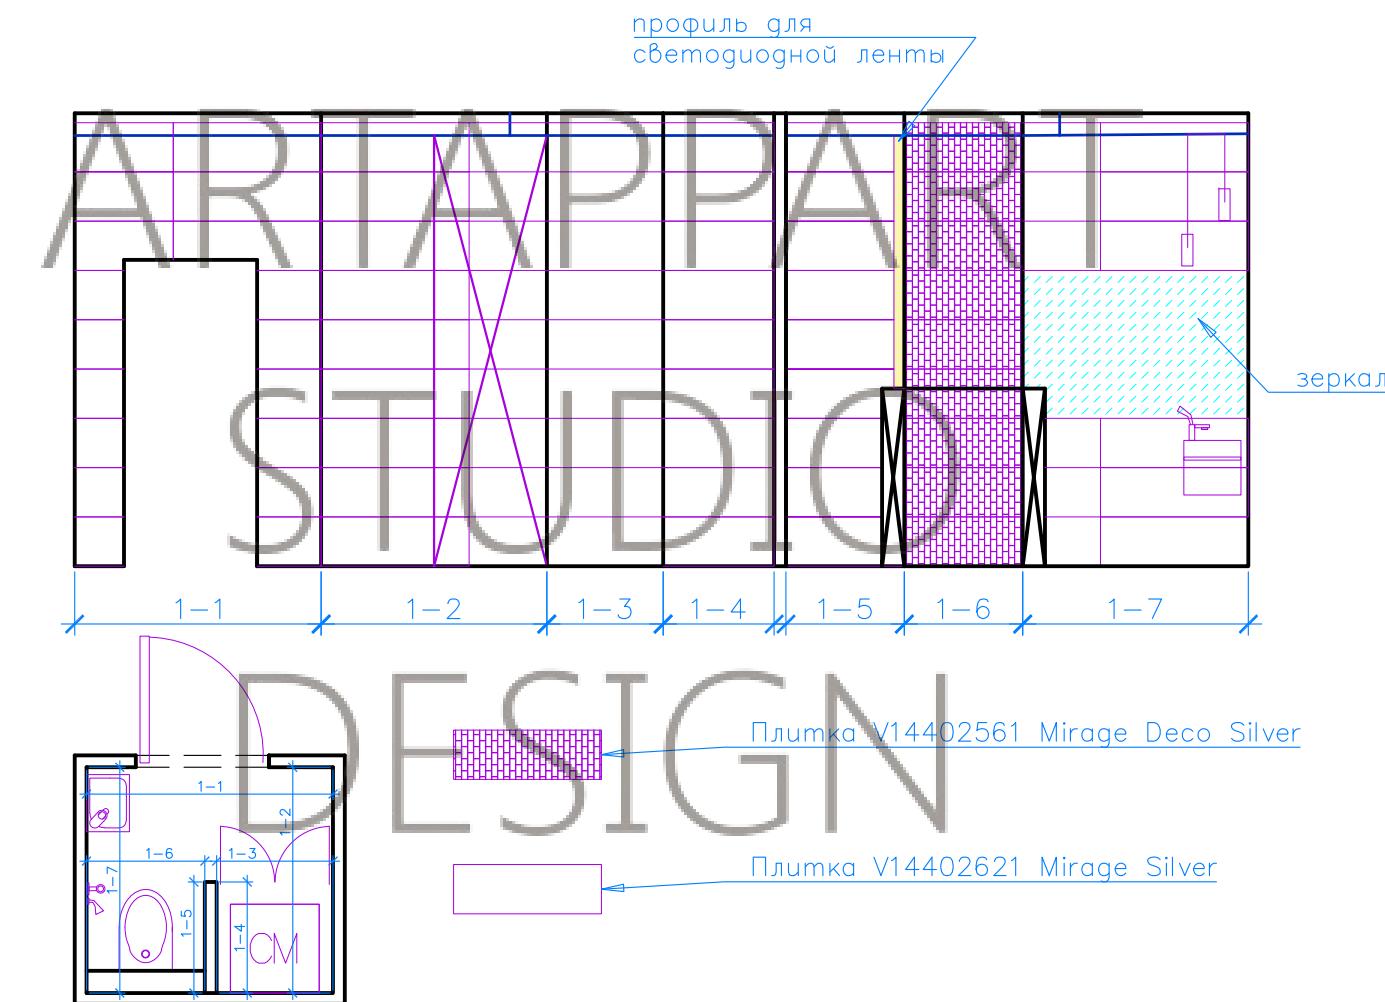

Изм.	Кол. уч.	Листм	№ док.	Подп.	Дата	Разработка дизайн-проекта квартиры	Стадия	Листм	Листмов
Заказчик					2019		P		
Разработ.					2019	Развертки по стенам ванной комнаты			
						M 1: 50			



ARTAPPART  
DESIGN  
STUDIO

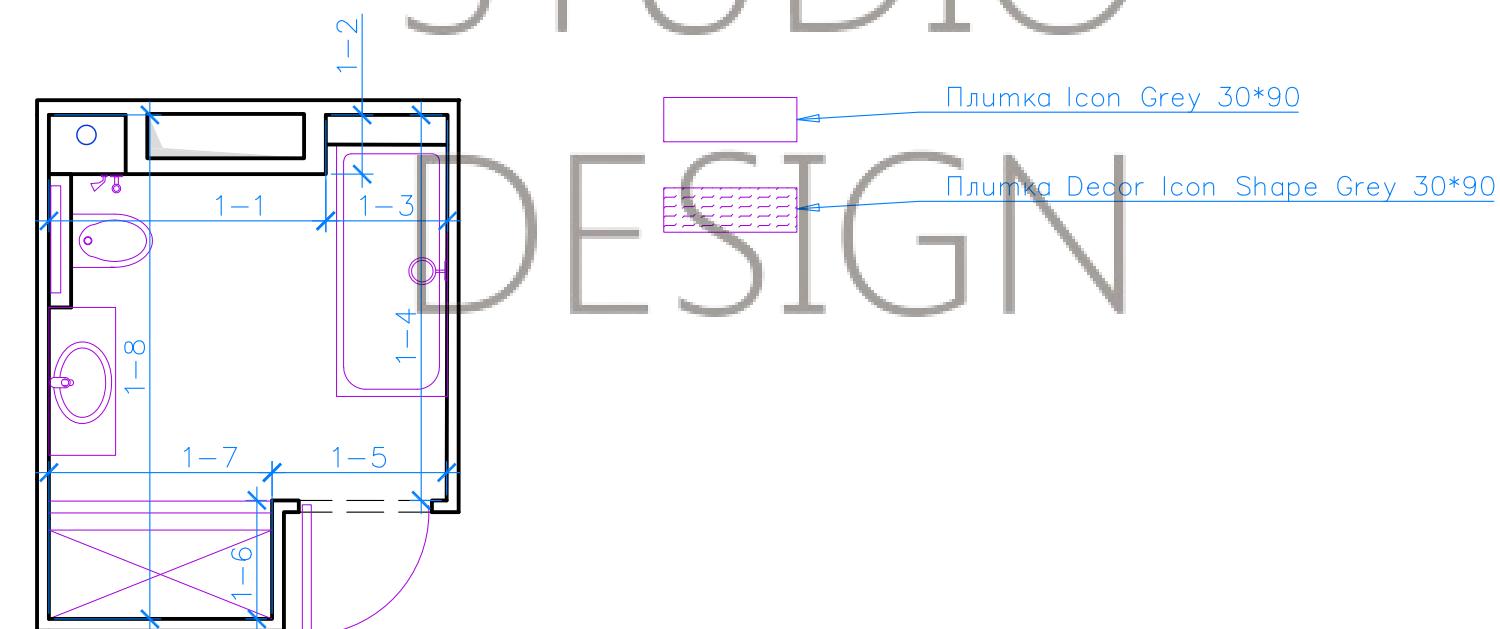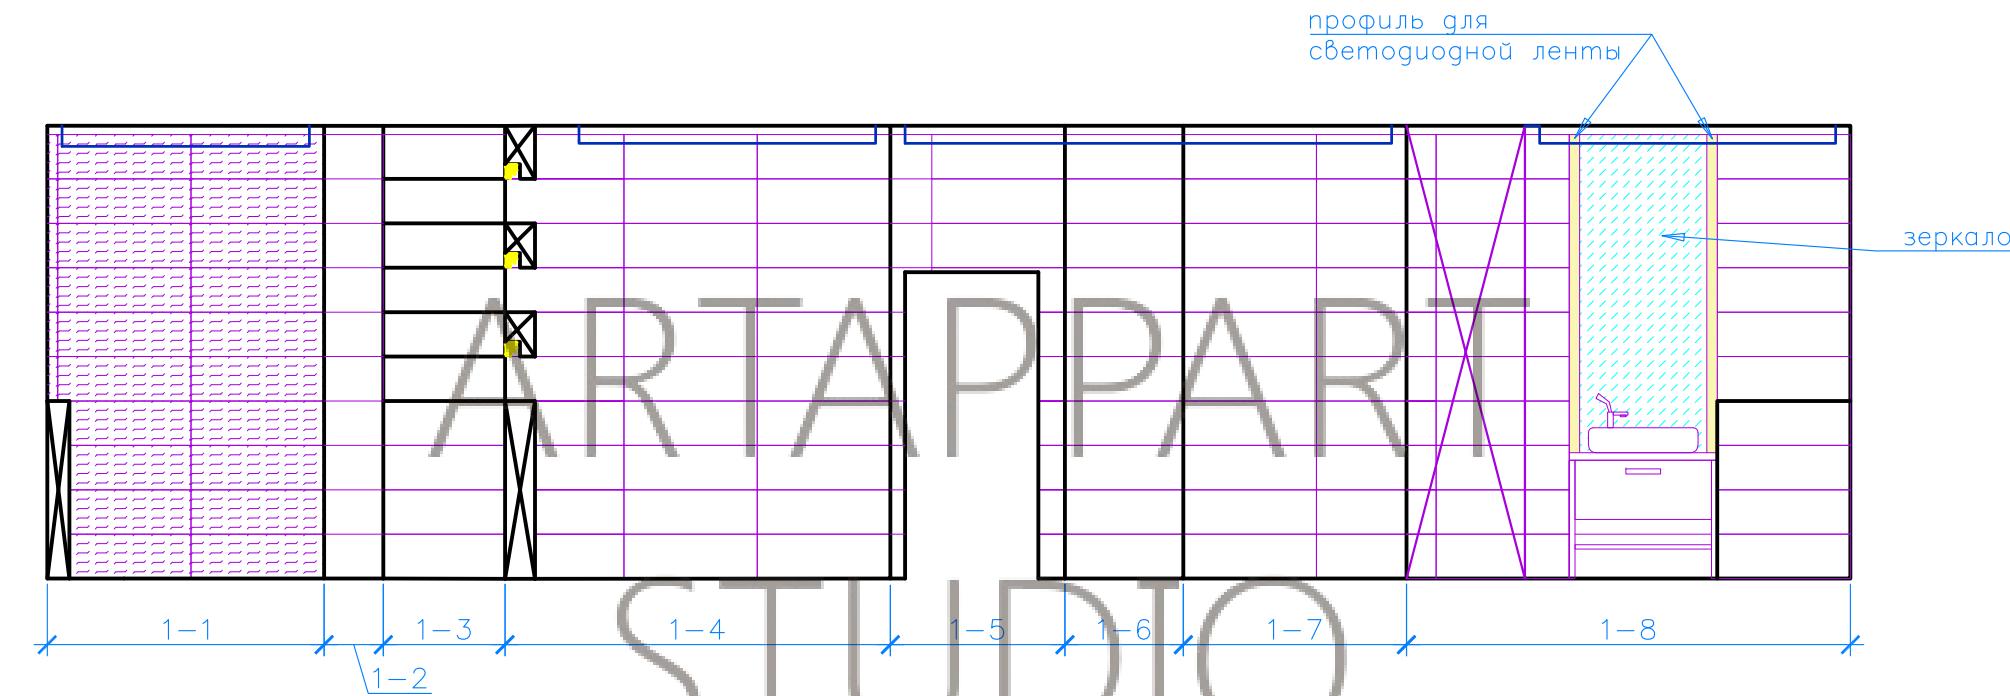

Инв. № подп.	Подп. и дата	Взам. инв.

Изм.	Кол. уч.	Листм	№ док.	Подп.	Дата	Разработка дизайн-проекта квартиры	Стадия	Листм	Листмов
Заказчик					2019				
Разработ.					2019	Развертки по стенам санузла	P		
						M 1:50			



ARTAPPART  
DESIGN  
STUDIO

Ведомость отделки помещений

Наименование и номер помещения	Вид отделки элементов интерьера						Примечание
	Пол	S, м <sup>2</sup>	Стены или перегородки	S, м <sup>2</sup>	Потолок	S, м <sup>2</sup>	
1 – Кухня–гостиная	Керамогранит Плинтус напольн	16,5 8,8 мп	Декоративная штукатурка Декоративный кирпич Плитка на кухонном фартуке, бирюзовая Плитка на кухонном фартуке, синяя Керамогранит на коробе с биокамином	11,3 15,8 40 9 5,4	Потолок Грильято Короб ГКЛ с окраской	15,0 2,6	S=16,5 кв. м
2 – Коридор – прихожая	Ламинат Керамогранит Плинтус напольн	9,8 0,9 11,0 мп	Декоративная штукатурка Роспись/фотообои Окраска (в зоне шкафа–купе и зекала)	22,8 4,0 11,8	Потолок ГКЛ с окраской Потолок ГКЛ с декоративной штукатуркой	10,6 3,0	S=10,7 кв. м
3 – Детская комната	Ламинат Плинтус напольн	18,5 12,2 мп	Фотообои Декоративный кирпич Окраска	11,4 10,5 4,1	Потолок с окраской Короб ГКЛ с окраской	16,1 3,1	S=18,5 кв. м

Согласовано

№ подп. подп. дата взм. инв.

Примечание:

Площади покрытий даны без учета запаса.

Изм.	Кол. уч.	Листм	№ док.	Подп.	Дата	Разработка дизайн–проекта квартиры	Стадия	Листм	Листмов				
Заказчик					2019		P						
Разработ.					2019	Ведомость отделки							



Ведомость отделки помещений

Наименование и номер помещения	Вид отделки элементов интерьера						Примечание
	Пол	S, м <sup>2</sup>	Стены или перегородки	S, м <sup>2</sup>	Потолок	S, м <sup>2</sup>	
4 – Спальня	Ламинат Плинтус напольн	17,0 13,9 мп	Декоративная штукатурка Декоративный кирпич Окраска (в зоне зеркала)	29,2 9,3 2,6 шт	Потолок с окраской Потолок ГКЛ с окраской	5,8 10,7	S=17,0 кв. м
5 – Лоджия	Керамогранит Плинтус напольн	3,1 3,2 мп	Декоративная штукатурка Декоративный кирпич	22,8 9,3	Потолок ГКЛ с отделкой ламинатом	3,1	S=3,1 кв. м
6 – Ванная комната	Керамогранит	7,3	Керамогранит Керамогранит декор Окраска (в зоне зеркала)	28,8 5,5 2,0	Потолок с окраской Короб ГКЛ с окраской	2,5 4,6	S=7,3 кв. м
7 – Санузел	Керамогранит	2,3	Керамогранит Керамогранит декор Окраска (в зоне зеркала)	17,5 2,5 1,5	Потолок Грильято Короб ГКЛ с окраской	2,0 0,8	S=2,5 кв. м

Согласовано

№ подп. подп. и дата взм. инв.

Примечание:

Площади покрытий даны без учета запаса.

Изм.	Кол. уч.	Листм	№ док.	Подп.	Дата	Разработка дизайн-проекта квартиры	Стадия	Листм	Листмов				
Заказчик					2019		P						
Разработ.					2019	Ведомость отделки							



Согласовано			

1 вариант



Плитка декор  
Cifre Ceramica Sea  
Размер: 200x200



Плитка декор  
Cifre Ceramica Sea  
Размер: 200x200

3 вариант



Плитка напольная  
EQUIPE Terra - Орех  
Размер: 200x200

Плитка настенная  
Керама Marazzi Арабески  
Размер: 260x300



Плитка настенная  
Керама Marazzi Арабески  
Размер: 260x300

ARTAPPART  
STUDIO

2 вариант



Плитка напольная  
EQUIPE Terra - Орех  
Размер: 200x200



[www.NovaCeramics.ru](http://www.NovaCeramics.ru)

Плитка настенная  
Керама Marazzi Арабески  
Размер: 260x300



Плитка декор  
Керама Marazzi Арабески  
Размер: 260x300

Примечание:

Данные коллажи представлены для примера, не относятся к приложенной рабочей документации.

Инв. № подл.	Подп.	и дата	Взам. инв.	Листм	№ док	Подп.	Дата	Разработка дизайн-проекта квартиры	Стадия	Листм	Листмов				
Заказчик						2019									
Разработ.				2019											

Согласовано			
Инв. № подл.	Подп. и дата	Взам. инв.	



Примечание:  
Данные коллажи представлены для примера, не относятся к приложенной рабочей документации.

Изм.	Кол. уч.	Листн	№ док.	Подп.	Дата	Разработка дизайн-проекта квартиры	Стадия	Лист	Листов
Заказчик					2019		P		
Разработ.					2019				